


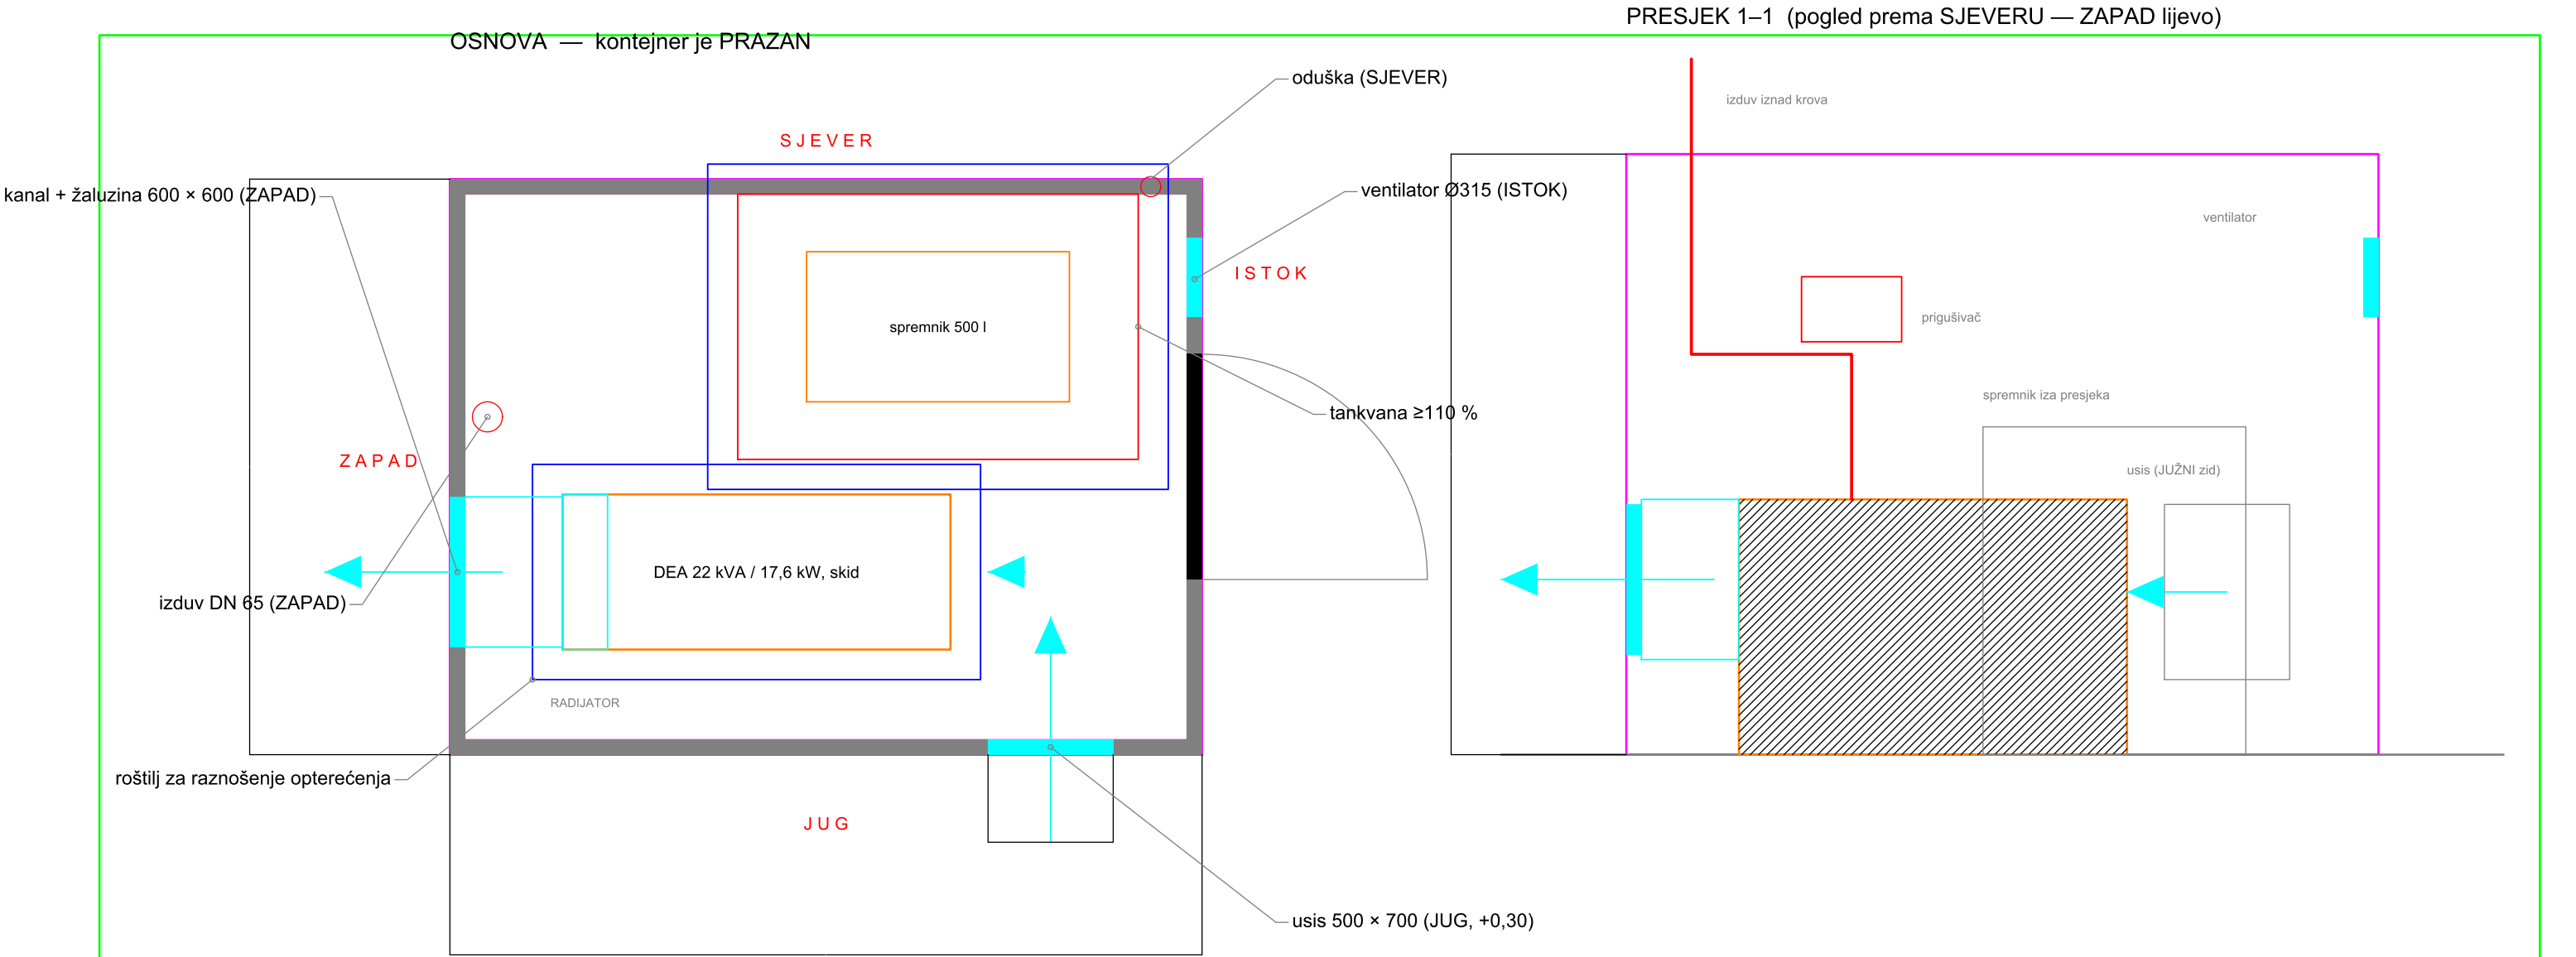

NAPOMENE:

- 1 FG Wilson P22-6 (Skid), TL 2019-08-14: hladnjak 1980 m³/h, sagorijevanje 90 m³/h, toplota u prostor 7,1 kW, maks. vanjski otpor 125 Pa.
- 2 Žaluzine zadovoljavaju: usis 500 × 700 (Δp≈16 Pa) + izlaz 600 × 600 (≈15 Pa) + kanal < 125 Pa.
- 3 Ventilator 1200 m³/h je DOPUNSKA ventilacija (min. 120 m³/h); protok hlađenja daje ventilator hladnjaka.
- 4 Izduv DN 65 usvojen (NO 50 zadovoljava protutlak, ali radi pri 33 m/s).
- 5 Pod je dimenzionisan na 10,00 kN/m² ravnomjerno raspodijeljeno (projekat lokacije, 4.4.2.3). Agregat 3,93 i pun spremnik 9,2 kN/m² su KONCENTRISANI — roštilj za raznošenje je OBAVEZAN.
- 6 RASPORED: usis JUG (+0,30), kanal/izlaz i izduv ZAPAD, oduška SJEVER, ventilator ISTOK; ≥3 m između usisa, izduva i oduške. Ništa ne izbacuje prema ormarima na SJEVERU.
- 7 UNOS: skid 620 mm kroz vrata 900 mm. Kontejner je PRAZAN.

bh BH TELECOM d.d. SARAJEVO Izvršna direkcija za tehnologiju i razvoj servisa		
Investitor: BH Telecom d.d. Sarajevo, Franca Lehara 7, Sarajevo		
Objekat: BS SJEDNICA (Bileća) — autonomni hibridni sistem napajanja		
Faza: Tenderska dokumentacija — Prilog III		šifra projekta: BHT-SJEDNICA-2026
Naziv crteža: DEA u postojećem kontejneru — osnova i presjek		razmjera: 1:25
Projektant: Rusmir Skopljak, dipl. ing. el.	ovjerio: Rusmir Skopljak, dipl. ing. el.	godina / broj crteža: 2026. M-01