


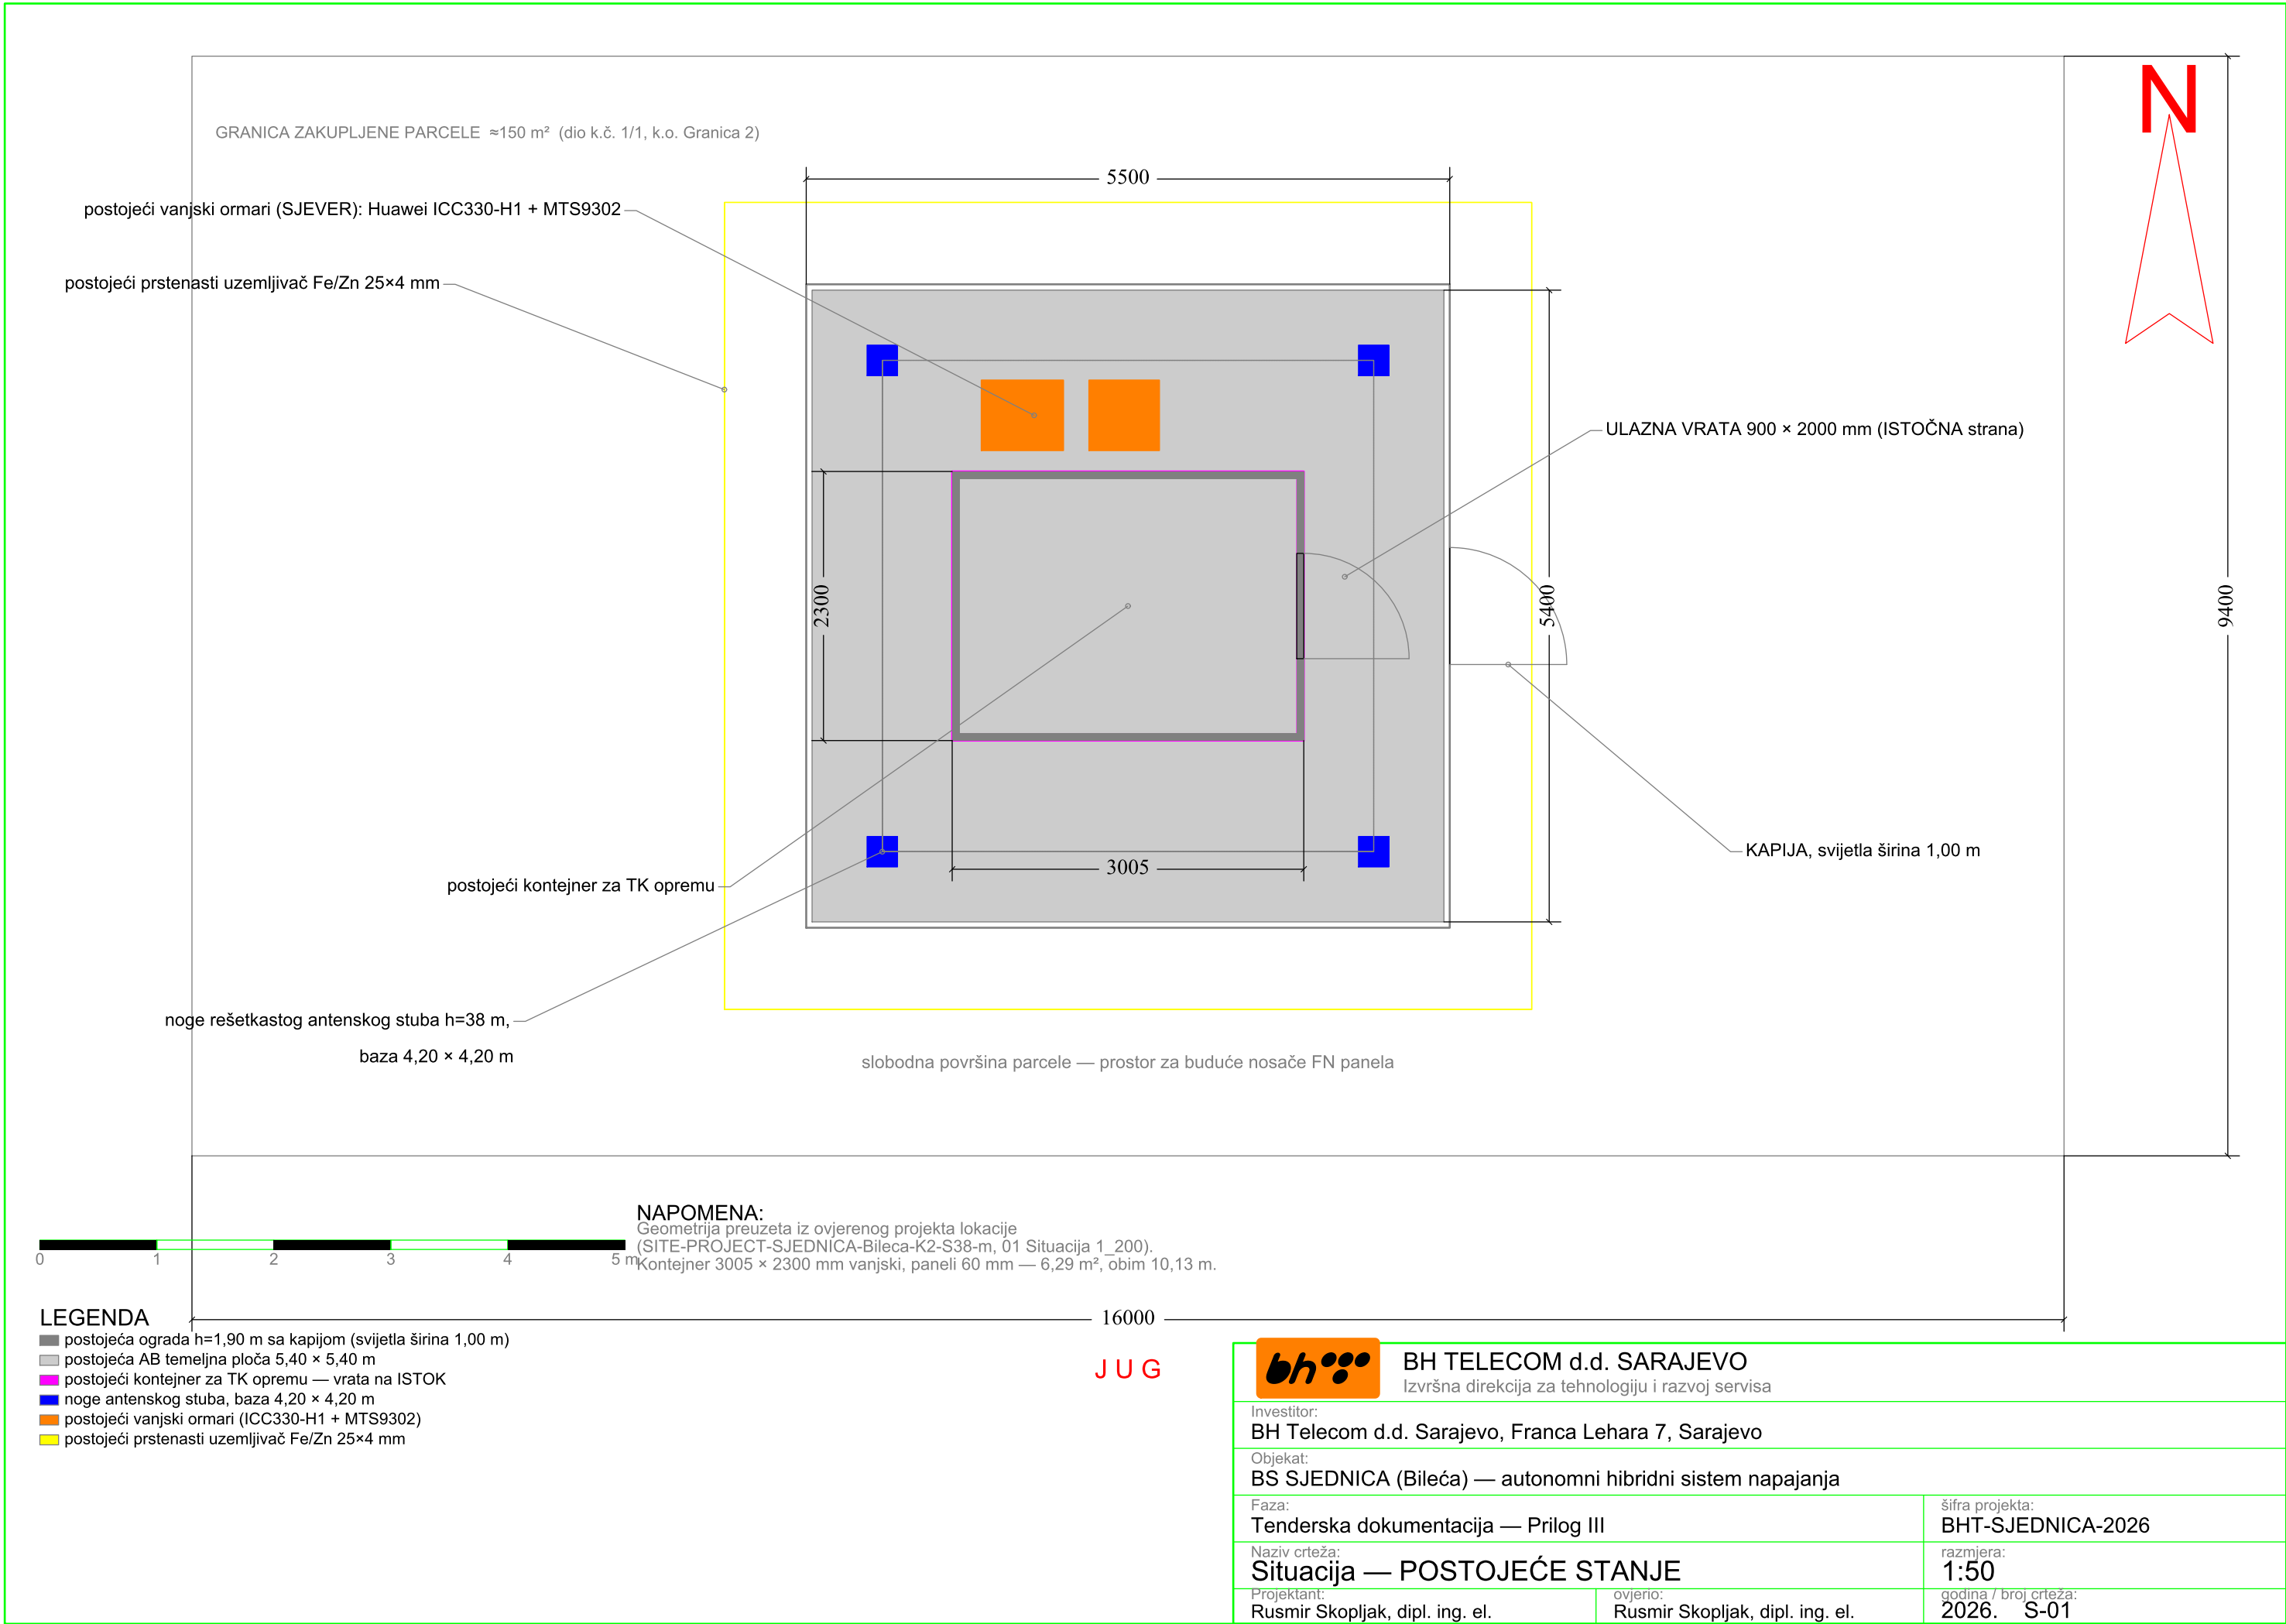

BH TELECOM d.d. SARAJEVO Izvršna direkcija za tehnologiju i razvoj servisa		
Investitor: BH Telecom d.d. Sarajevo, Franca Lehara 7, Sarajevo		
Objekat: BS SJEDNICA (Bileća) — autonomni hibridni sistem napajanja		
Faza: Tenderska dokumentacija — Prilog III		šifra projekta: BHT-SJEDNICA-2026
Naziv crteža: Situacija — POSTOJEĆE STANJE		razmjera: 1:50
Projektant: Rusmir Skopljak, dipl. ing. el.	ovjerio: Rusmir Skopljak, dipl. ing. el.	godina / broj crteža: 2026. S-01