


OBJAŠNJENJA:

1 Polje FN panela: 2 reda × 2 modula 585 Wp u portretu — širina polja 2305 mm, dužina po nagibu 4576 mm (2 × 2278 mm), horizontalna projekcija 3236 mm pri 45° (nepromijenjeno — isti broj redova po nagibu kao ranija izvedba 2×3).
ISPRAVLJENO (istorija): raniji nacrt je projekciju izvodio iz uzdužne grede 3656 mm (2590 mm), što nije dužina polja modula — vidjeti F.2 u proračunu.

2 Dvije temeljne trake po nosaču, 450 × 3300 mm, dubina 900 mm, razmak 1600 mm, beton C25 na podlozi C10; dubina i armatura prema ovjerenom proračunu.

3 Donja ivica podignuta na +1,50 m (bilo +0,50 m uz 2×6 izvedbu) — iskorišten prostor dobijen manjim opterećenjem vjetra po nosaču (3×4 umjesto 2×6, v. F.6). Gornja ivica +4,74 m, 2,84 m iznad kote ograde h=1,90 m.

4 CUSTOM IZRADA prema qp ≥ 1,20 kN/m² (sail 10,55 m²/nosaču, ULS uzgon 18,1 kN, moment 62,8 kNm) — vidjeti napomenu na listu S-02 i proračun F.6.

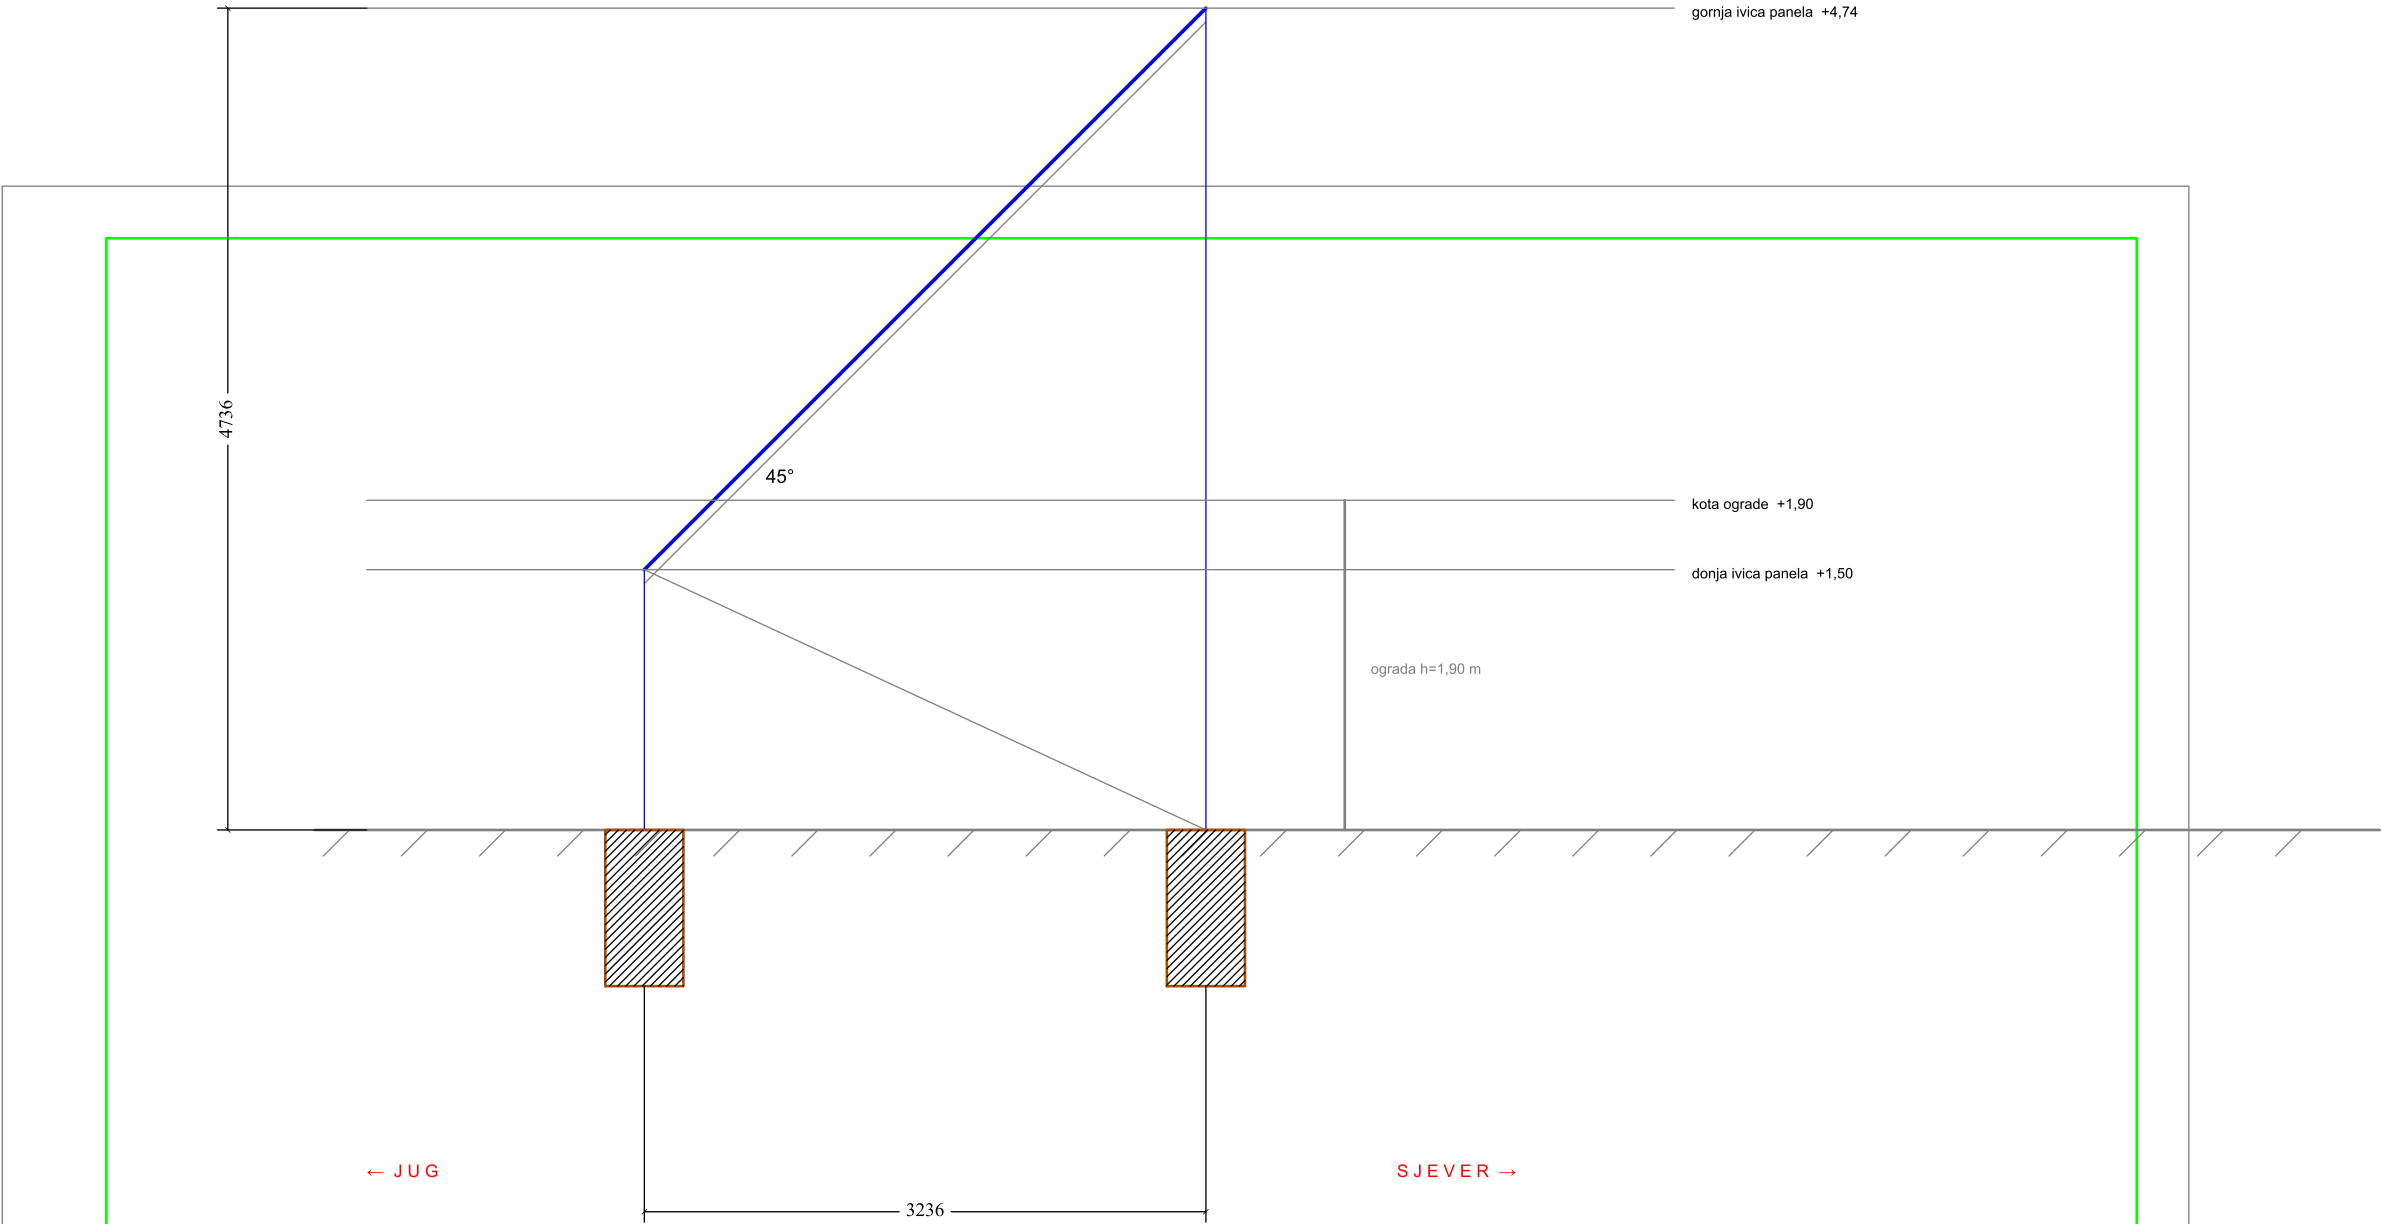

bh BH TELECOM d.d. SARAJEVO Izvršna direkcija za tehnologiju i razvoj servisa		
Investitor: BH Telecom d.d. Sarajevo, Franca Lehara 7, Sarajevo		
Objekat: BS SJEDNICA (Bileća) — autonomni hibridni sistem napajanja		
Faza: Tenderska dokumentacija — Prilog III	Šifra projekta: BHT-SJEDNICA-2026	
Naziv crteža: Presjek A–A kroz nosač FN panela	razmjera: 1:30	
Projektant: Rusmir Skopljak, dipl. ing. el.	ovjereni: Rusmir Skopljak, dipl. ing. el.	godina / broj crteža: 2026. S-03