
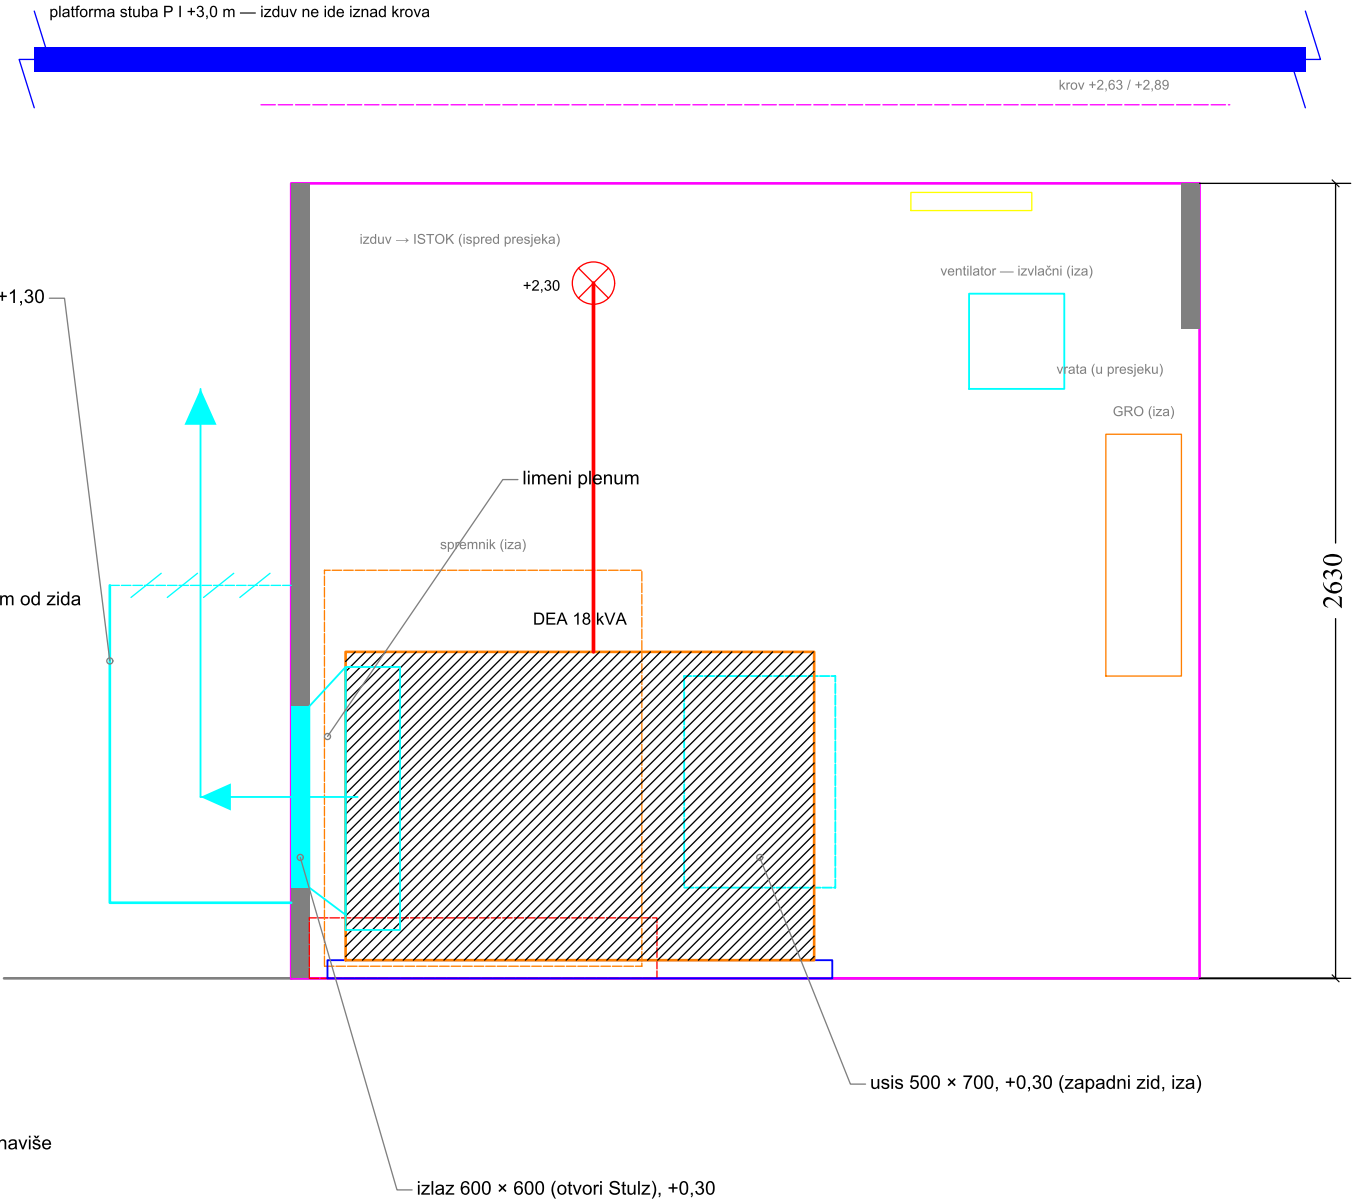


OSNOVA — kontejner je PRAZAN; klima-uređaj Stulz se demontira

PRESJEK 1–1 (os agregata — pogled prema ZAPADU, JUG lijevo)

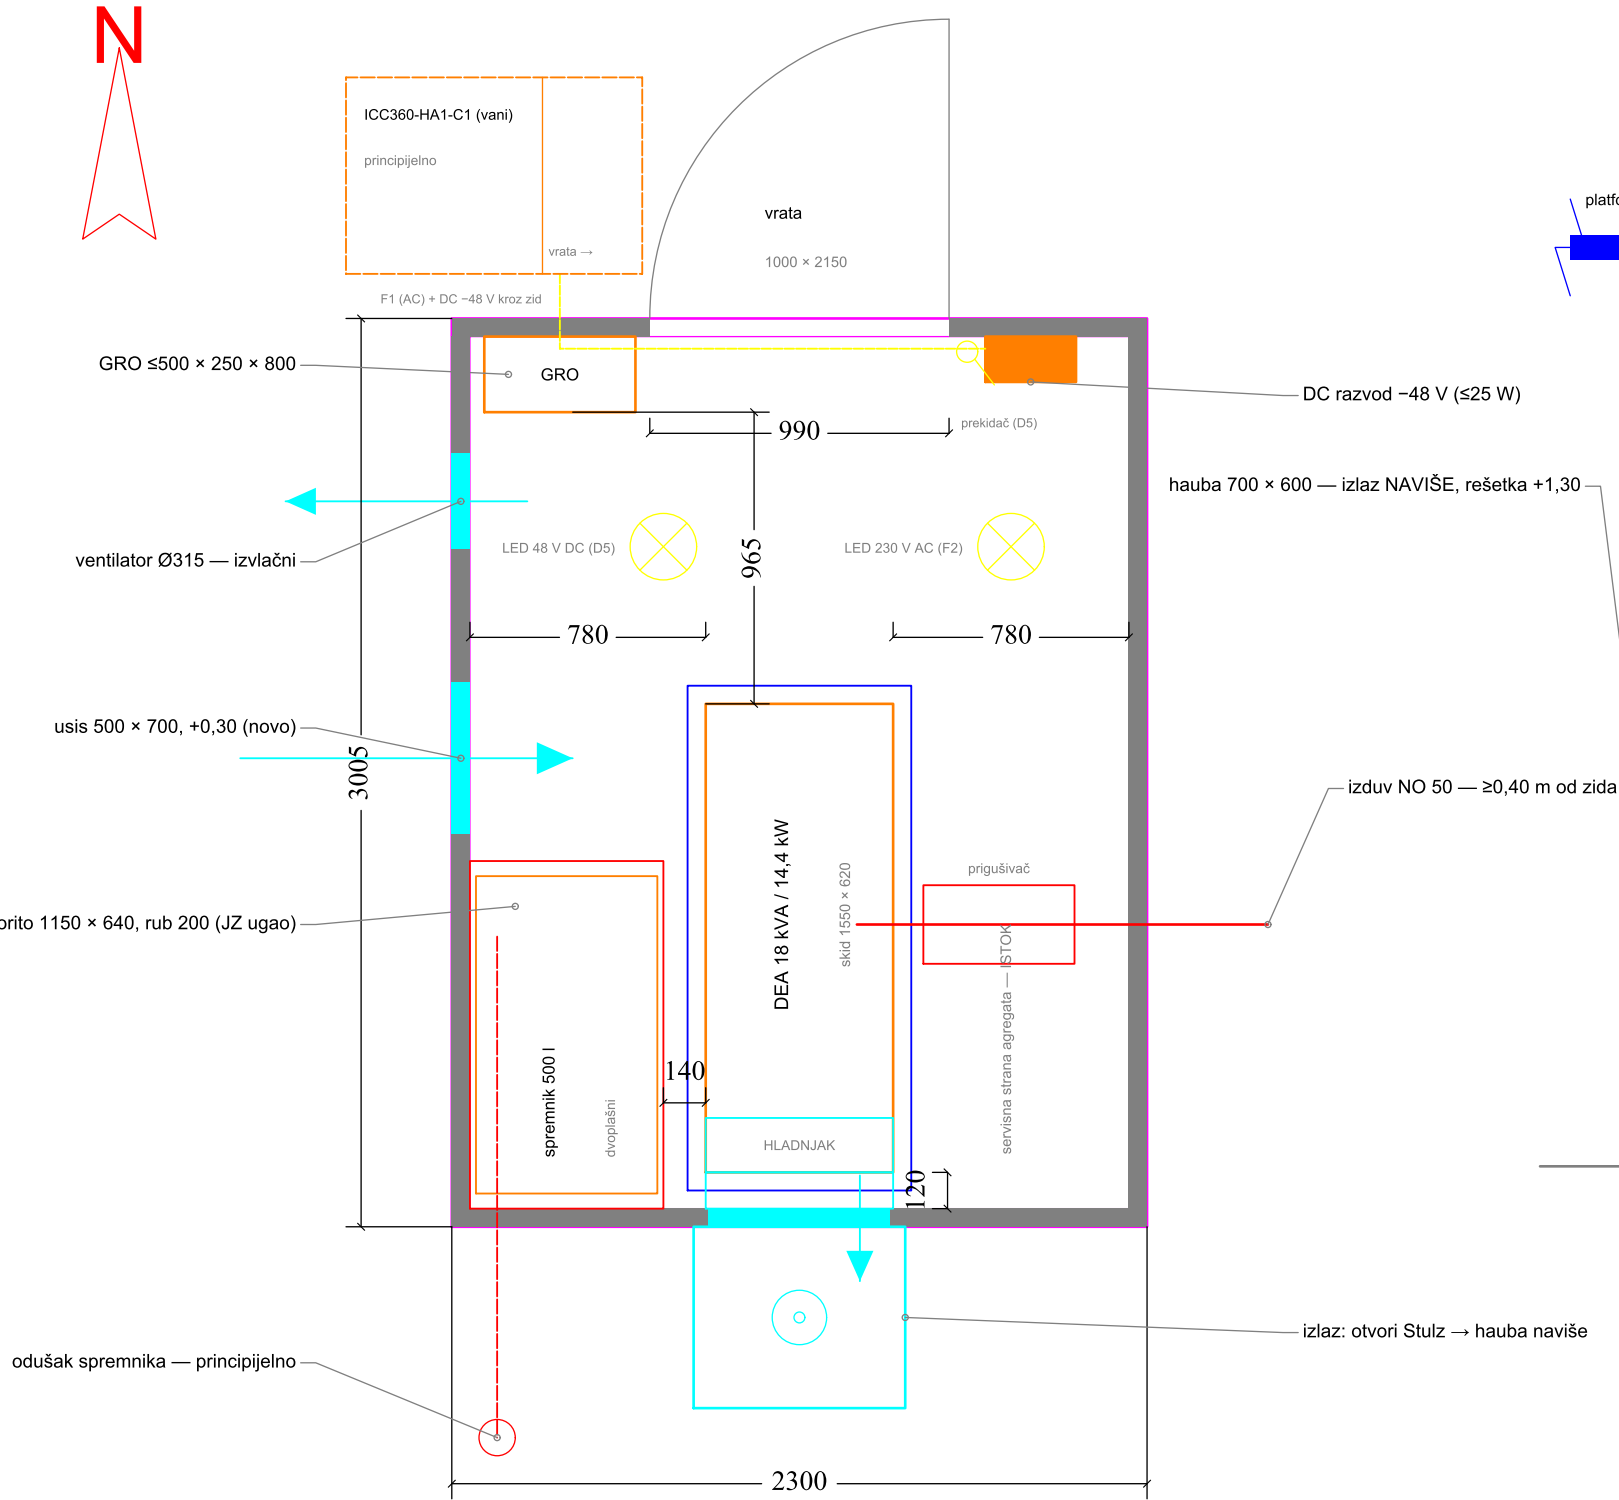

- NAPOMENE:**
- 1 DEA FG Wilson P18-6 (Skid) ili ekv., 18 kVA / 14,4 kW, pobuda PMG ili AREP/AUX; os SJEVER–JUG u sredini, hladnjak JUG.
 - 2 RASPORED (obavezujući): Stulz je u sredini JUŽNOG zida — izlaz zraka hladnjaka kroz njegove otvore, spojene/proširene na $\geq 0,36$ m² bruto (npr. 600 × 600), limeni plenum; višak otvora zatvoriti panelom 60 mm.
 - 3 Vani hauba 700 × 600, zatvorenih bočnih strana, rešetka na vrhu (+1,30); topli zrak ide NAVIŠE, ne na FN polje.
 - 4 Usis 500 × 700 ZAPAD (+0,30, novo, uz alternator). Izduv NO 50 kroz ISTOČNI zid na $\approx +2,30$ m, ispod platforme stuba; prigušivač u istočnom prolazu, hvatač iskri, kapa; završetak $\geq 0,40$ m od zida (3,21 m od usisa).
 - 5 GRO $\leq 500 \times 250 \times 800$ mm na SJEVERNOM zidu zapadno od vrata (zid 595 mm); roštilj OBAVEZAN pod skidom i koritom.
 - 6 Spremnik 500 l DVOPLAŠNI u koritu 1150 × 640, rub 200 mm, u JUGOZAPADNOM uglu.
 - 7 SERVIS: istočna strana 780 mm (servisna), sjeverni kraj 965 mm do GRO, zapadna 780 mm (uz korito 140 mm).
 - 8 Unos: skid 620 mm kroz vrata svijetle širine 990 mm, pravo po osi; najprije spremnik, zatim agregat.
 - 9 Ventilator Ø315 ZAPAD gore je IZVLAČNI (EC 48 V DC, D4). ICC360-HA1-C1 vani (SJEVER) — principijelno.
 - 10 Odušak spremnika kroz JUŽNI zid — principijelno: 3,10 m od izduva, 3,11 m od usisa; konačno prema elaboratu ZOP.
 - 11 DC razvod ~48 V $\approx 300 \times 200 \times 150$ istočno od vrata: rasvjeta prepreke, vatrodiojava, punjač aku., ventilator, predgrijač, D5.
 - 12 Rasvjeta: LED 230 V AC iz GRO (F2, radi dok DEA radi) i LED 48 V DC (D5) sa prekidačem uz vrata.
 - 13 Raspored je principijelan — Ponuđač ga potvrđuje na licu mjesta (mjere otvora Stulz, servisne tačke agregata).

bh BH TELECOM d.d. SARAJEVO Izvršna direkcija za tehnologiju i razvoj servisa		
Investitor: BH Telecom d.d. Sarajevo, Franca Lehara 7, Sarajevo		
Objekat: BS HAMZIĆI (ČITLUK) — autonomni hibridni sistem napajanja		
Faza: Tenderska dokumentacija — Prilog III		šifra projekta: BHT-HAMZICI-2026
Naziv crteža: Agregat u kontejneru — osnova i presjek 1–1		razmjera: 1:25
Projektant: Rusmir Skopljak, dipl. ing. el.	ovjerio: Rusmir Skopljak, dipl. ing. el.	godina / broj crteža: 2026. H-04