


PRESJEK A–A (osa zapadne trake nosača PV-2 — pogled prema ZAPADU)

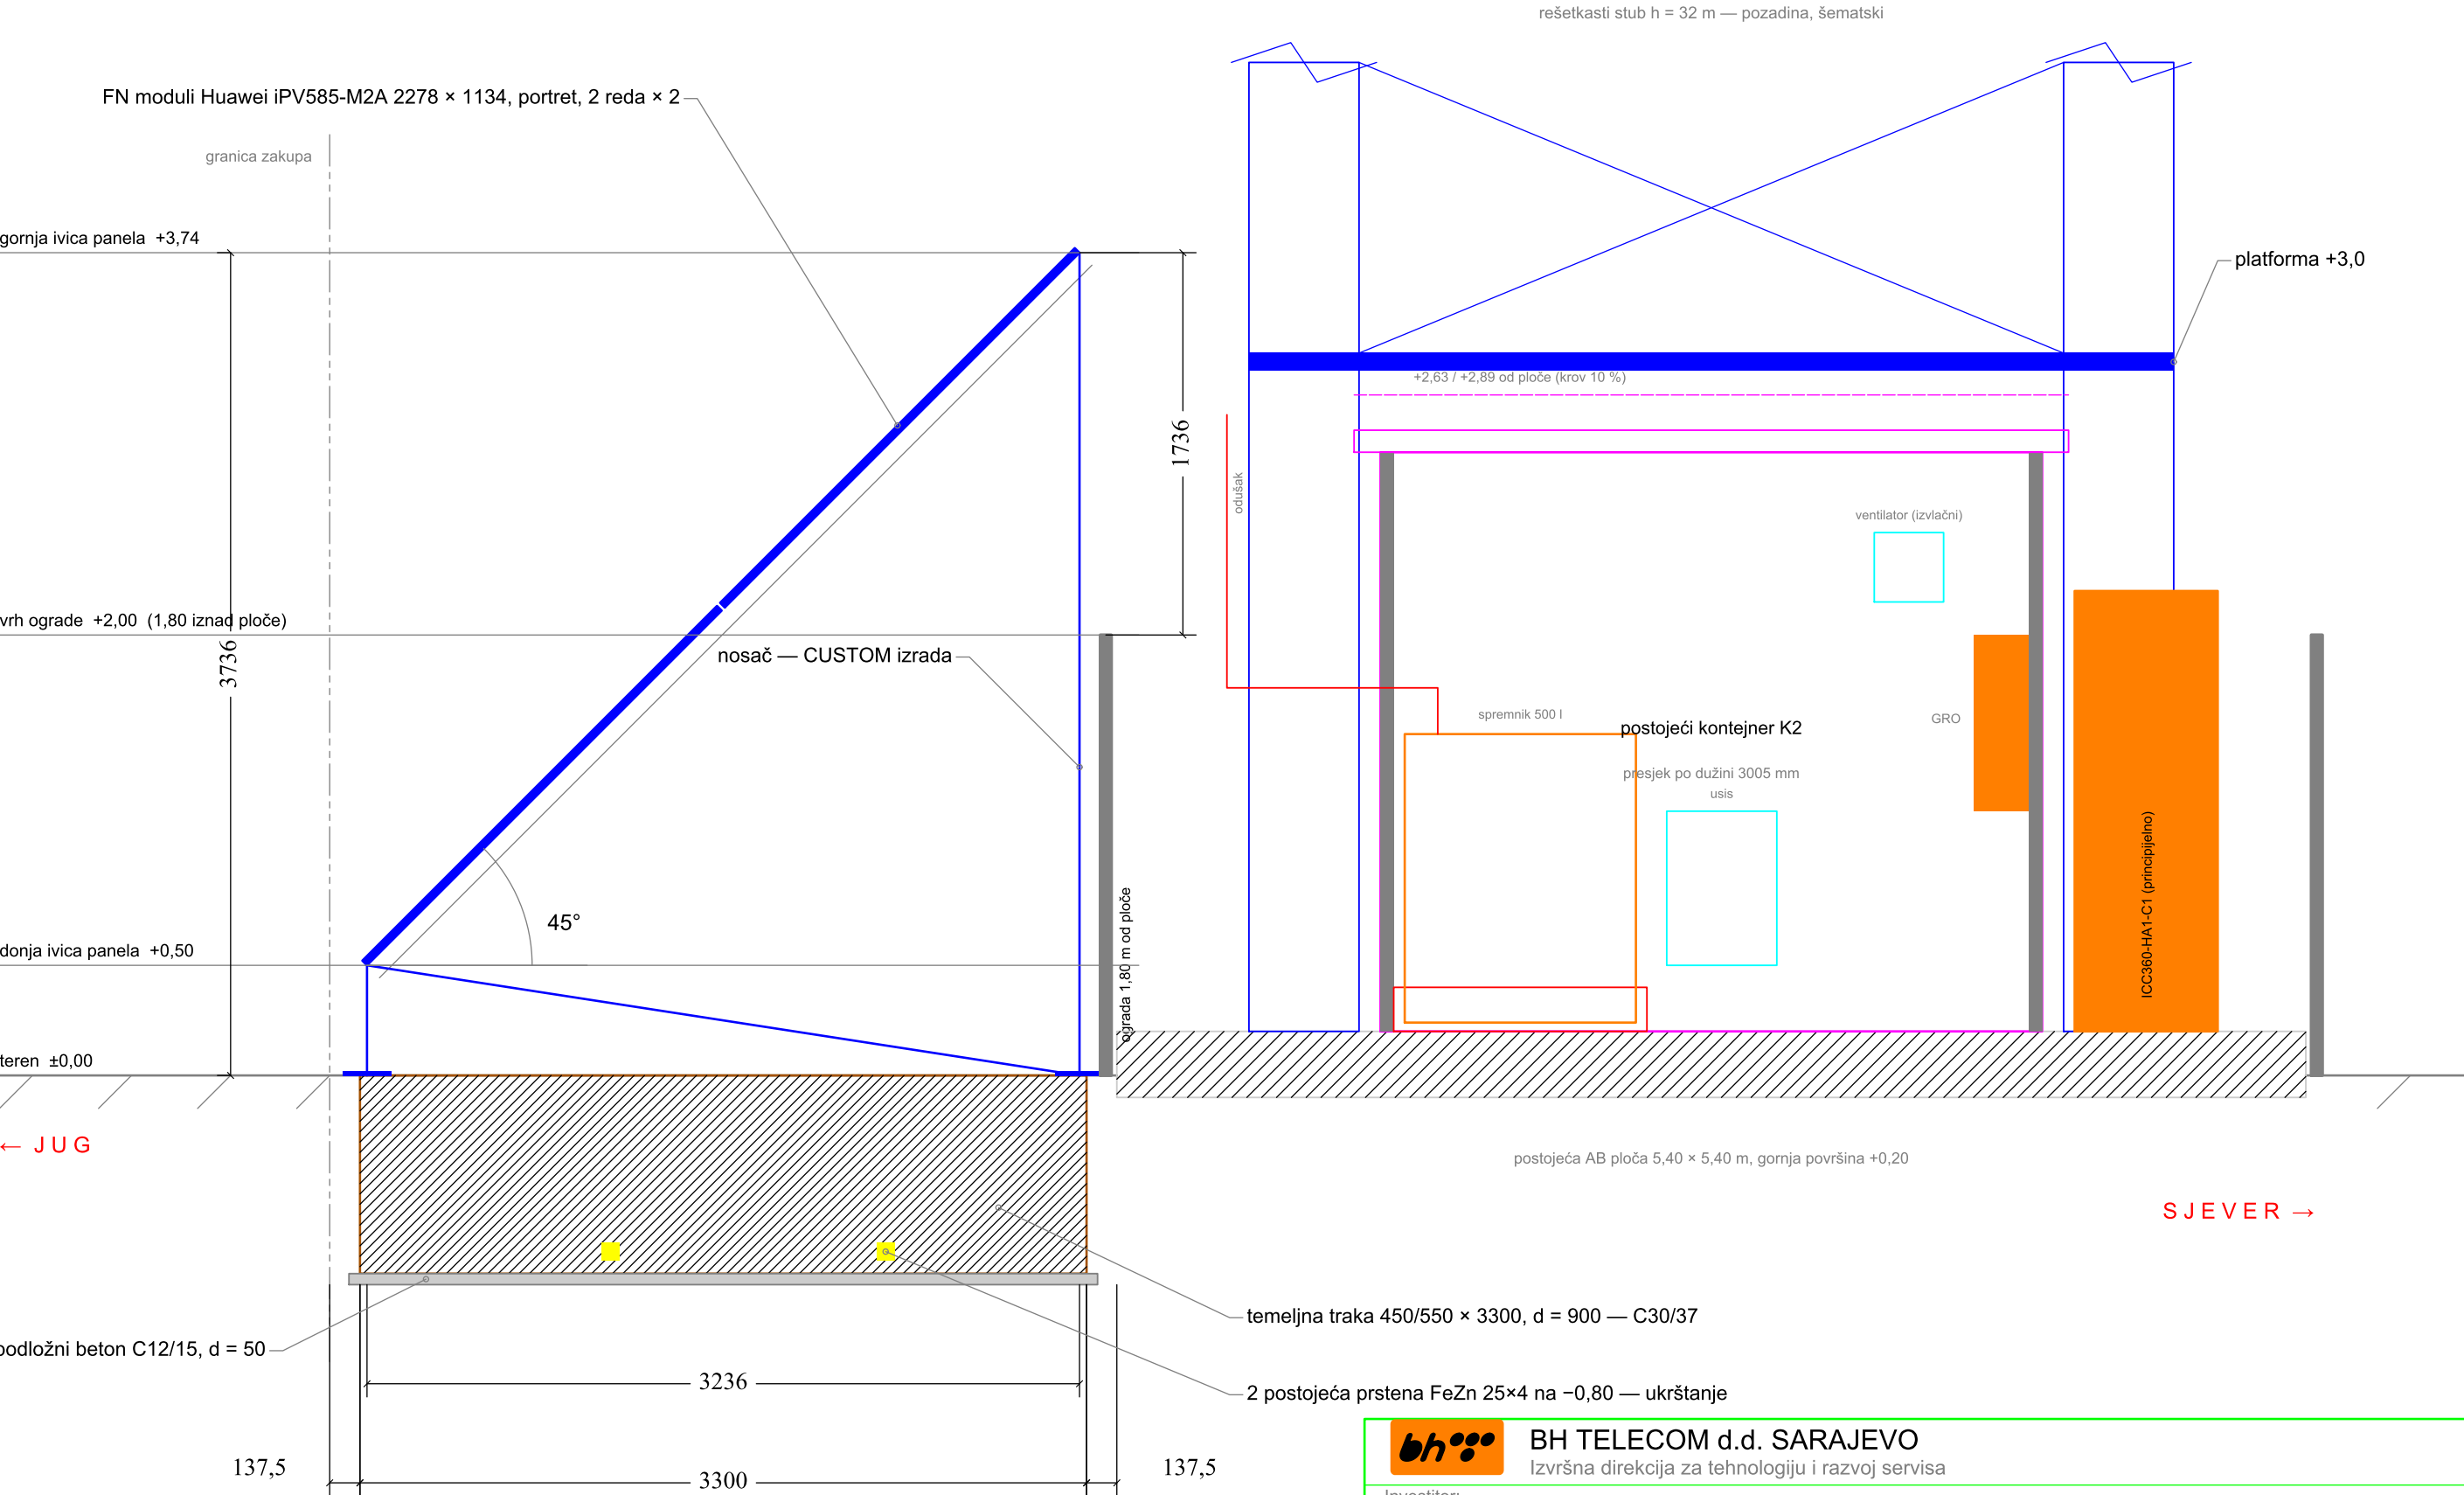

- OBJAŠNJENJA:**
- Polje: 2 reda × 2 modula 585 Wp (2278 × 1134 mm), portret; nagib 45°, horizontalna projekcija 3236 mm.
 - Dvije temeljne trake po nosaču 450/550 × 3300 mm, dubina 900 mm, razmak 1600 mm (druga iza ravni presjeka); beton C30/37 (XC4+XF3), armatura B500B, na podložnom betonu C12/15 d = 50 mm.
 - Kote od terena uz FN polje; teren je −0,20 m ispod ploče (04_Ograda). Donja ivica panela +0,50, gornja +3,74; vrh ograde +2,00 (1,80 m iznad ploče) — gornja ivica je 1,74 m iznad ograde.
 - Postojeći prsteni uzemljivača na 0,8 m presijecaju traku: lociranje, otkopavanje i premještanje ili premoštavanje prstena (LOT 1).
 - Trake su 137,5 mm od granice zakupa (JUG) i od ploče (SJEVER); položaj presjeka na H-02.
 - Stub, platforma P I (+3,0 m od ploče), kontejner i ormar ICC360 prikazani su šematski.

bh BH TELECOM d.d. SARAJEVO Izvršna direkcija za tehnologiju i razvoj servisa		
Investitor: BH Telecom d.d. Sarajevo, Franca Lehara 7, Sarajevo		
Objekat: BS HAMZIĆI (ČITLUK) — autonomni hibridni sistem napajanja		
Faza: Tenderska dokumentacija — Prilog III		šifra projekta: BHT-HAMZICI-2026
Naziv crteža: Presjek A–A kroz FN polje		razmjera: 1:30
Projektni: Rusmir Skopljak, dipl. ing. el.	ovjerio: Rusmir Skopljak, dipl. ing. el.	godina / broj crteža: 2026. H-03