





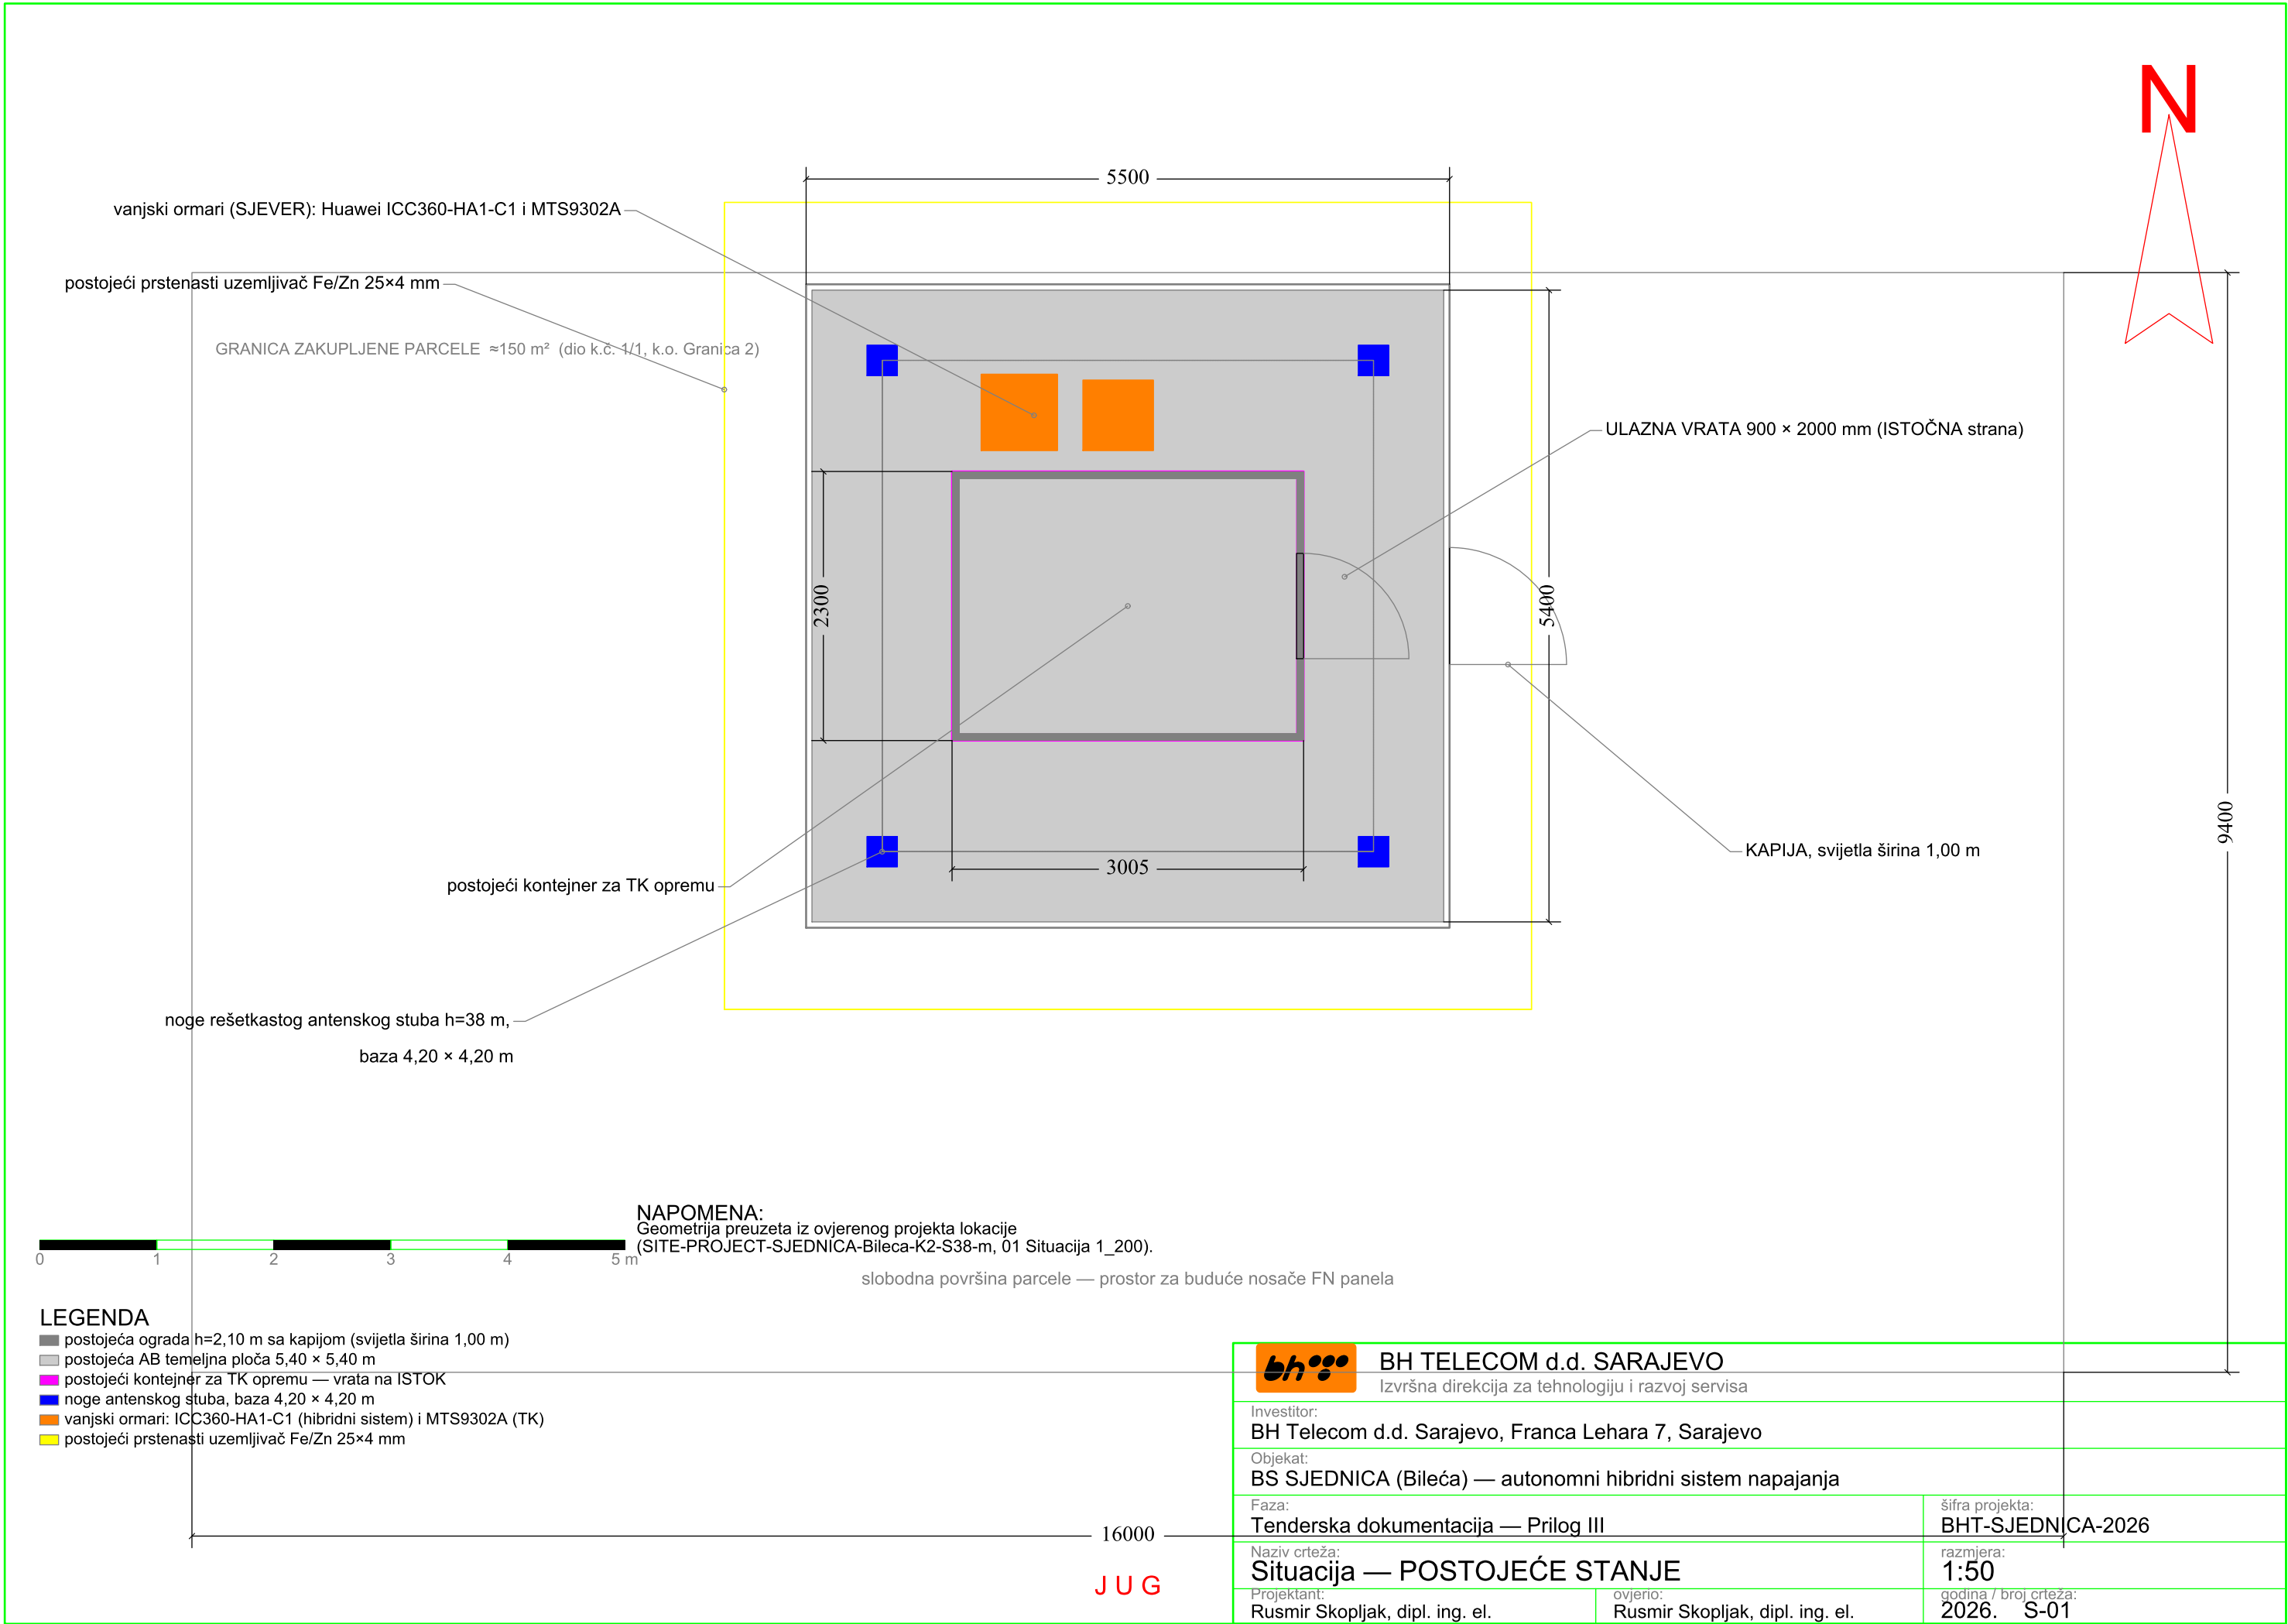

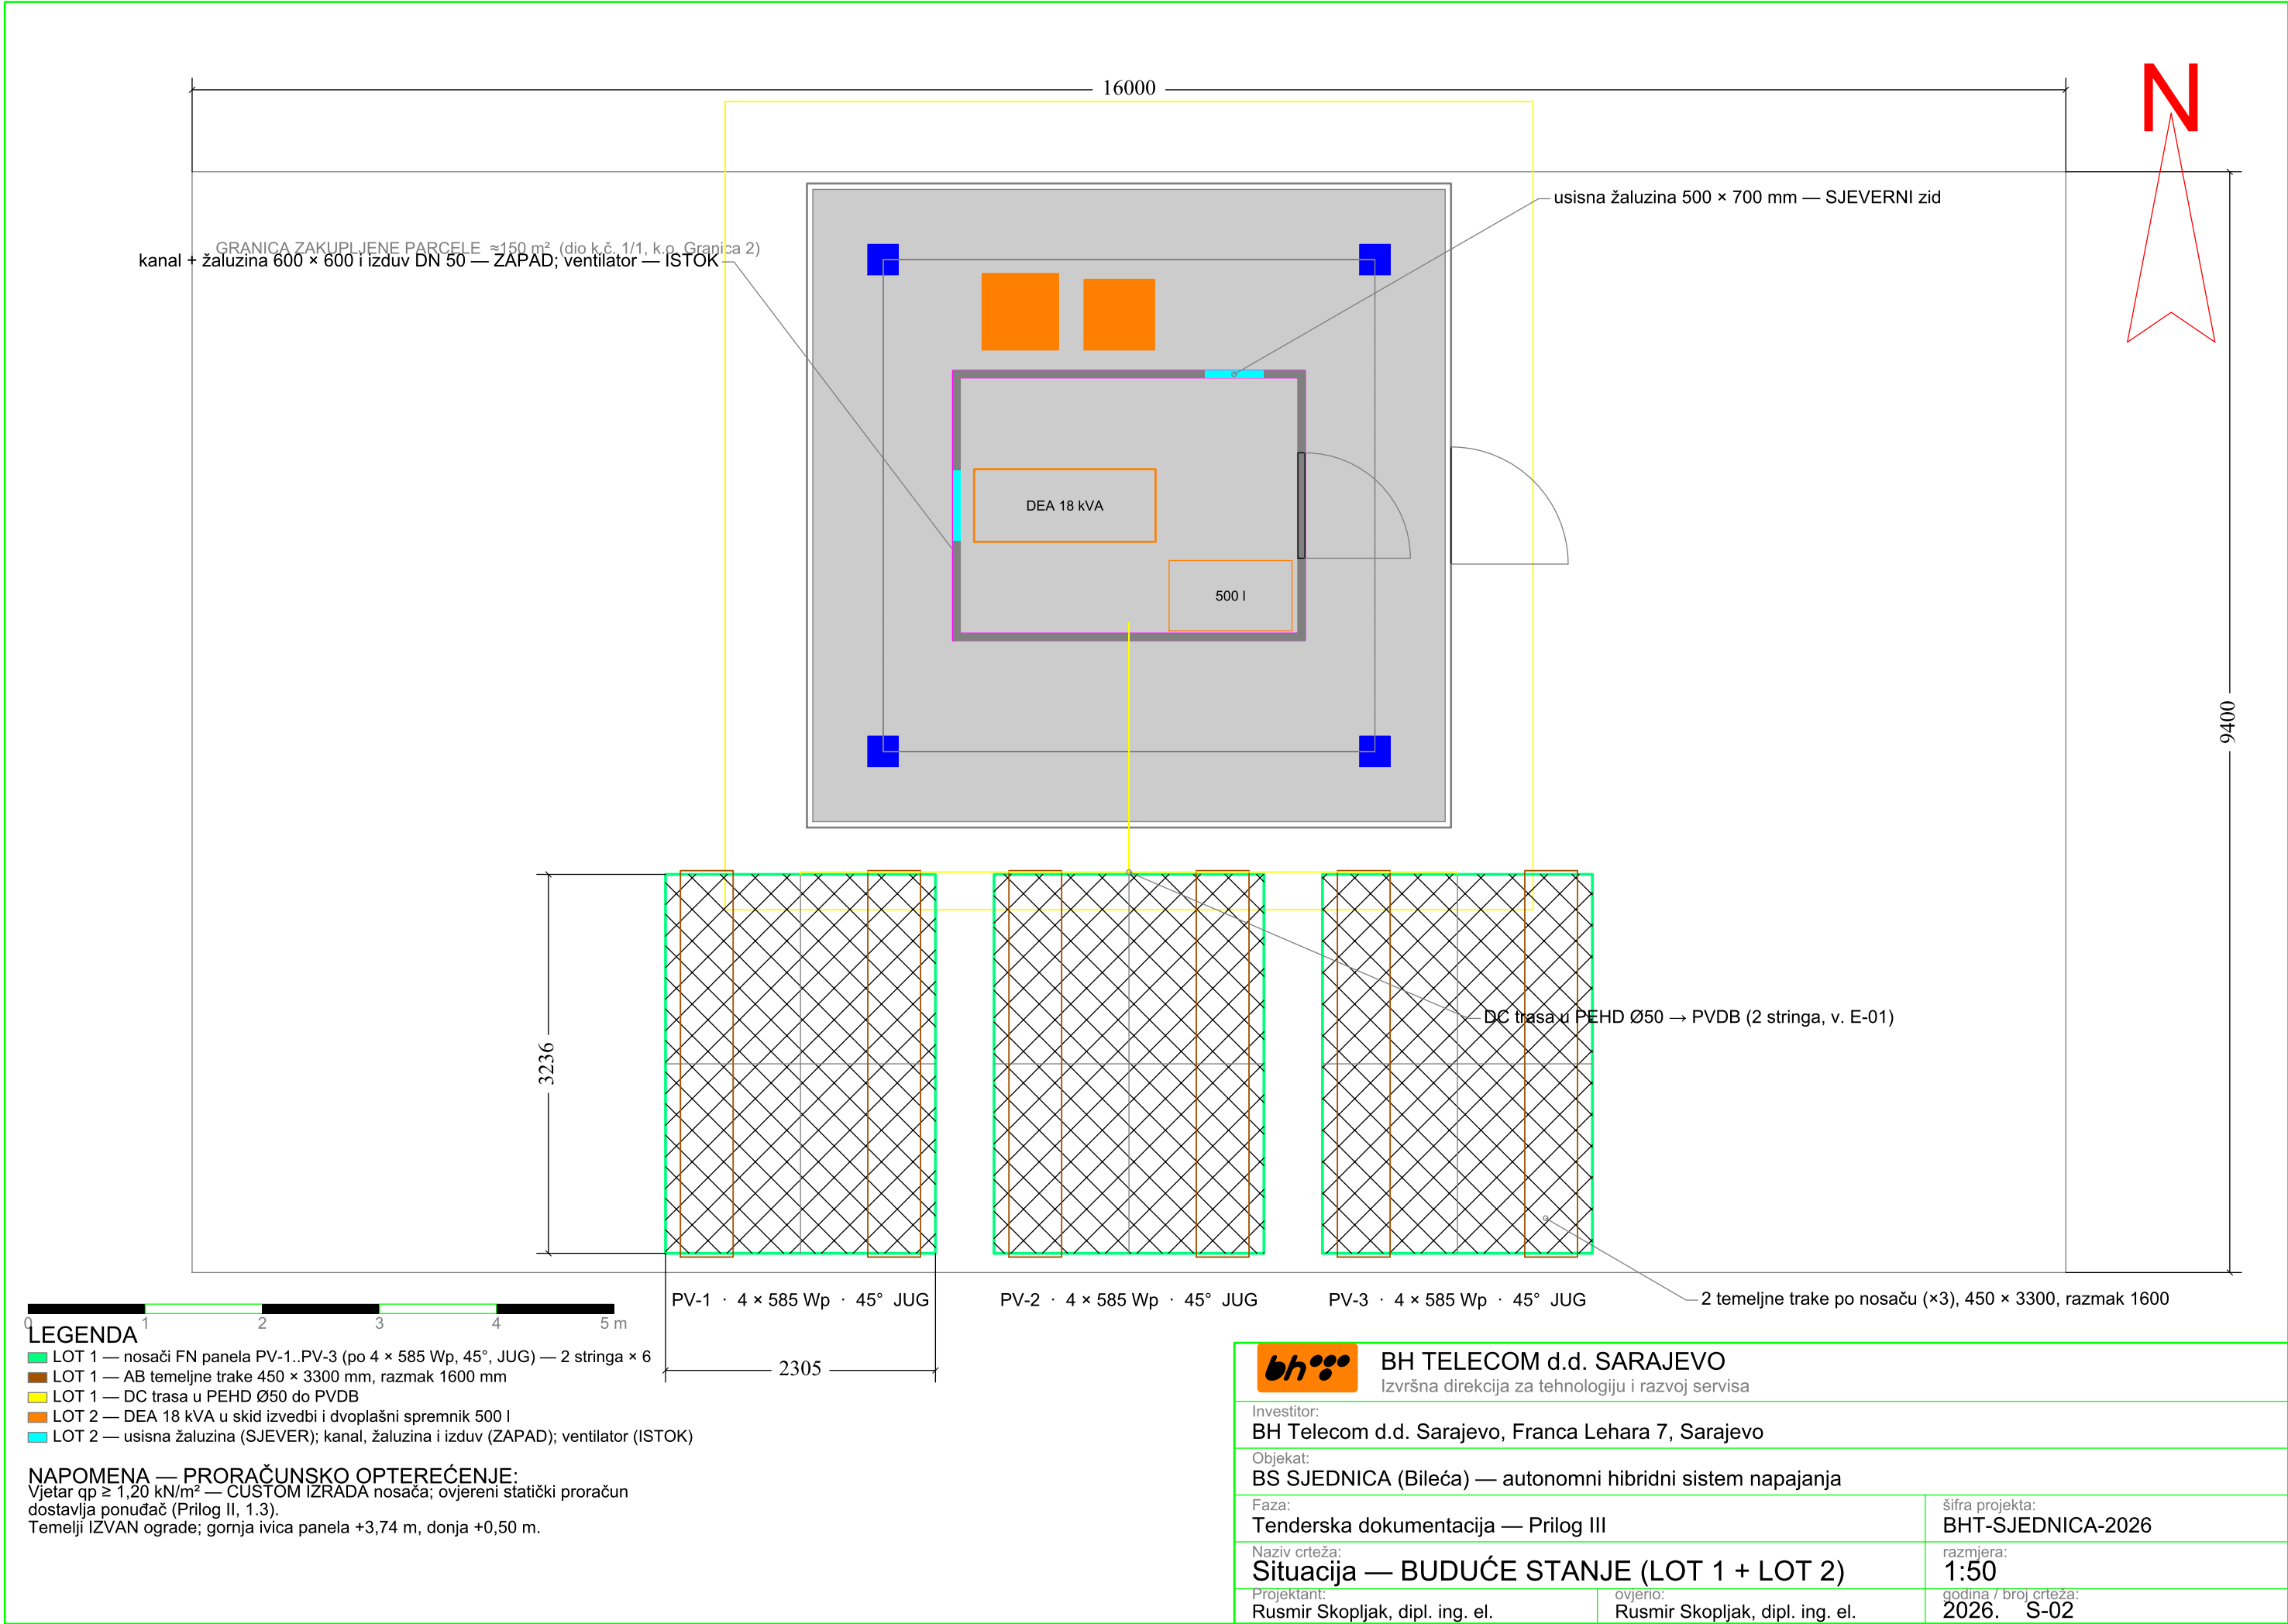

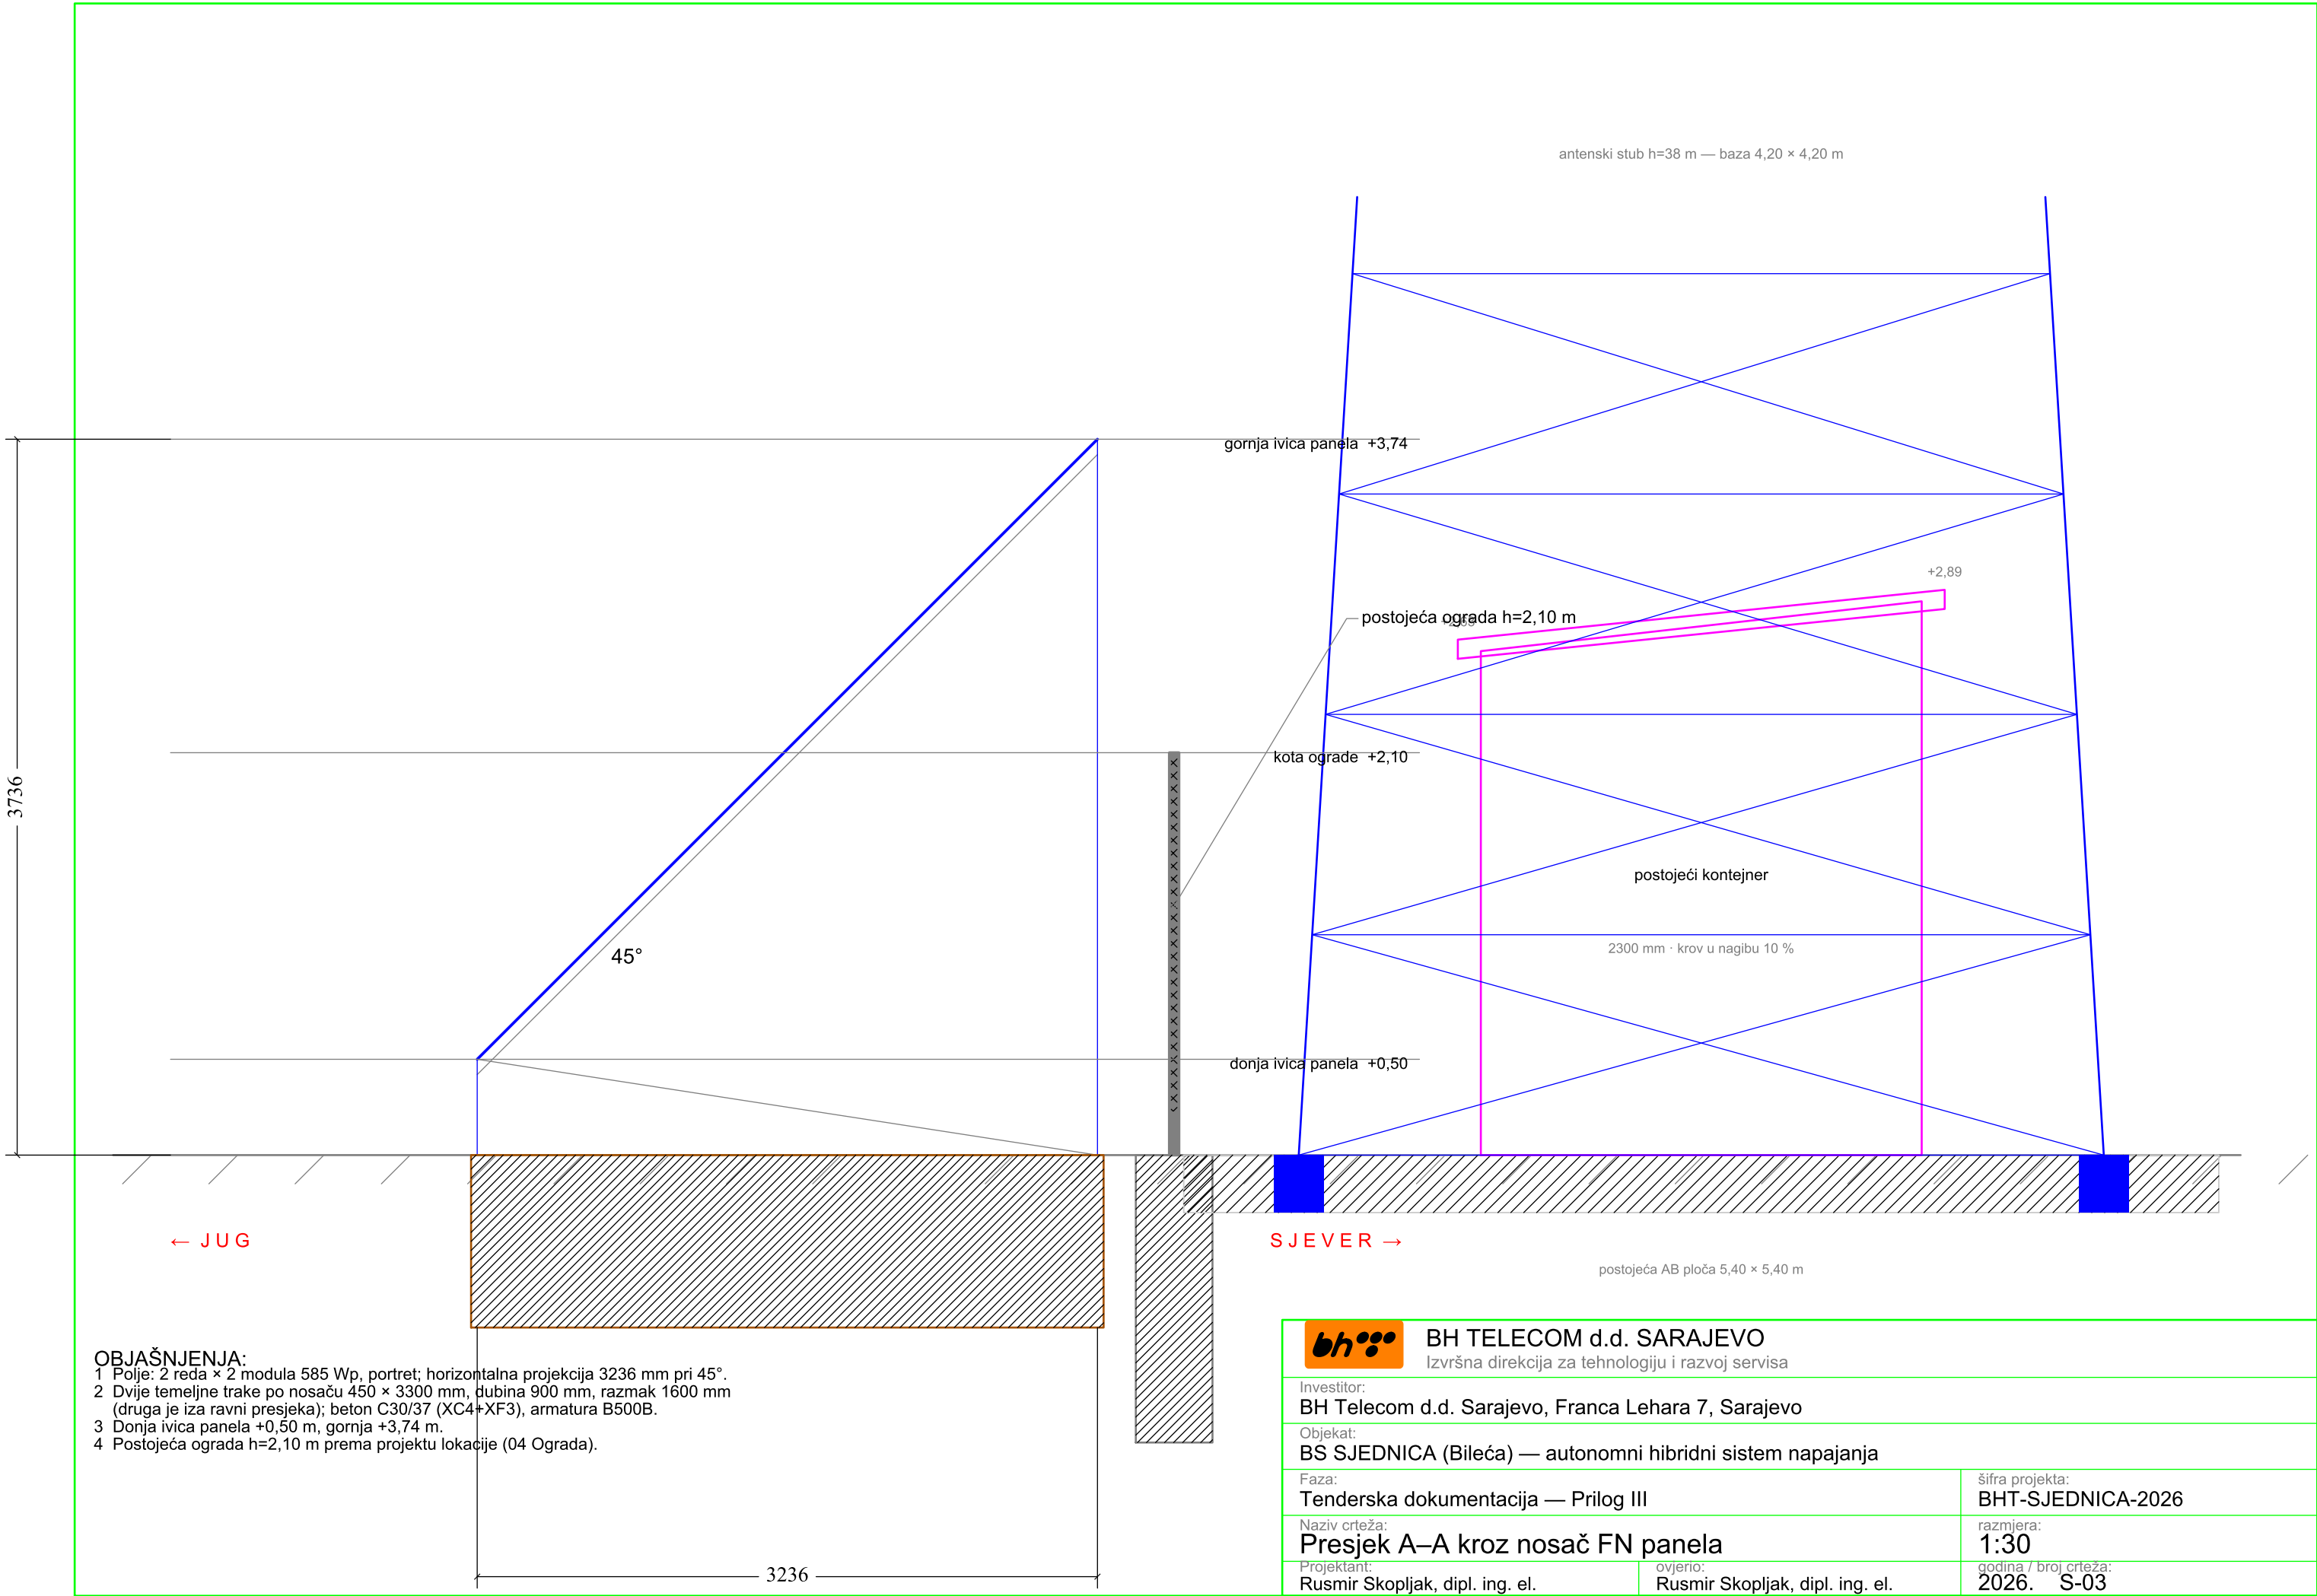

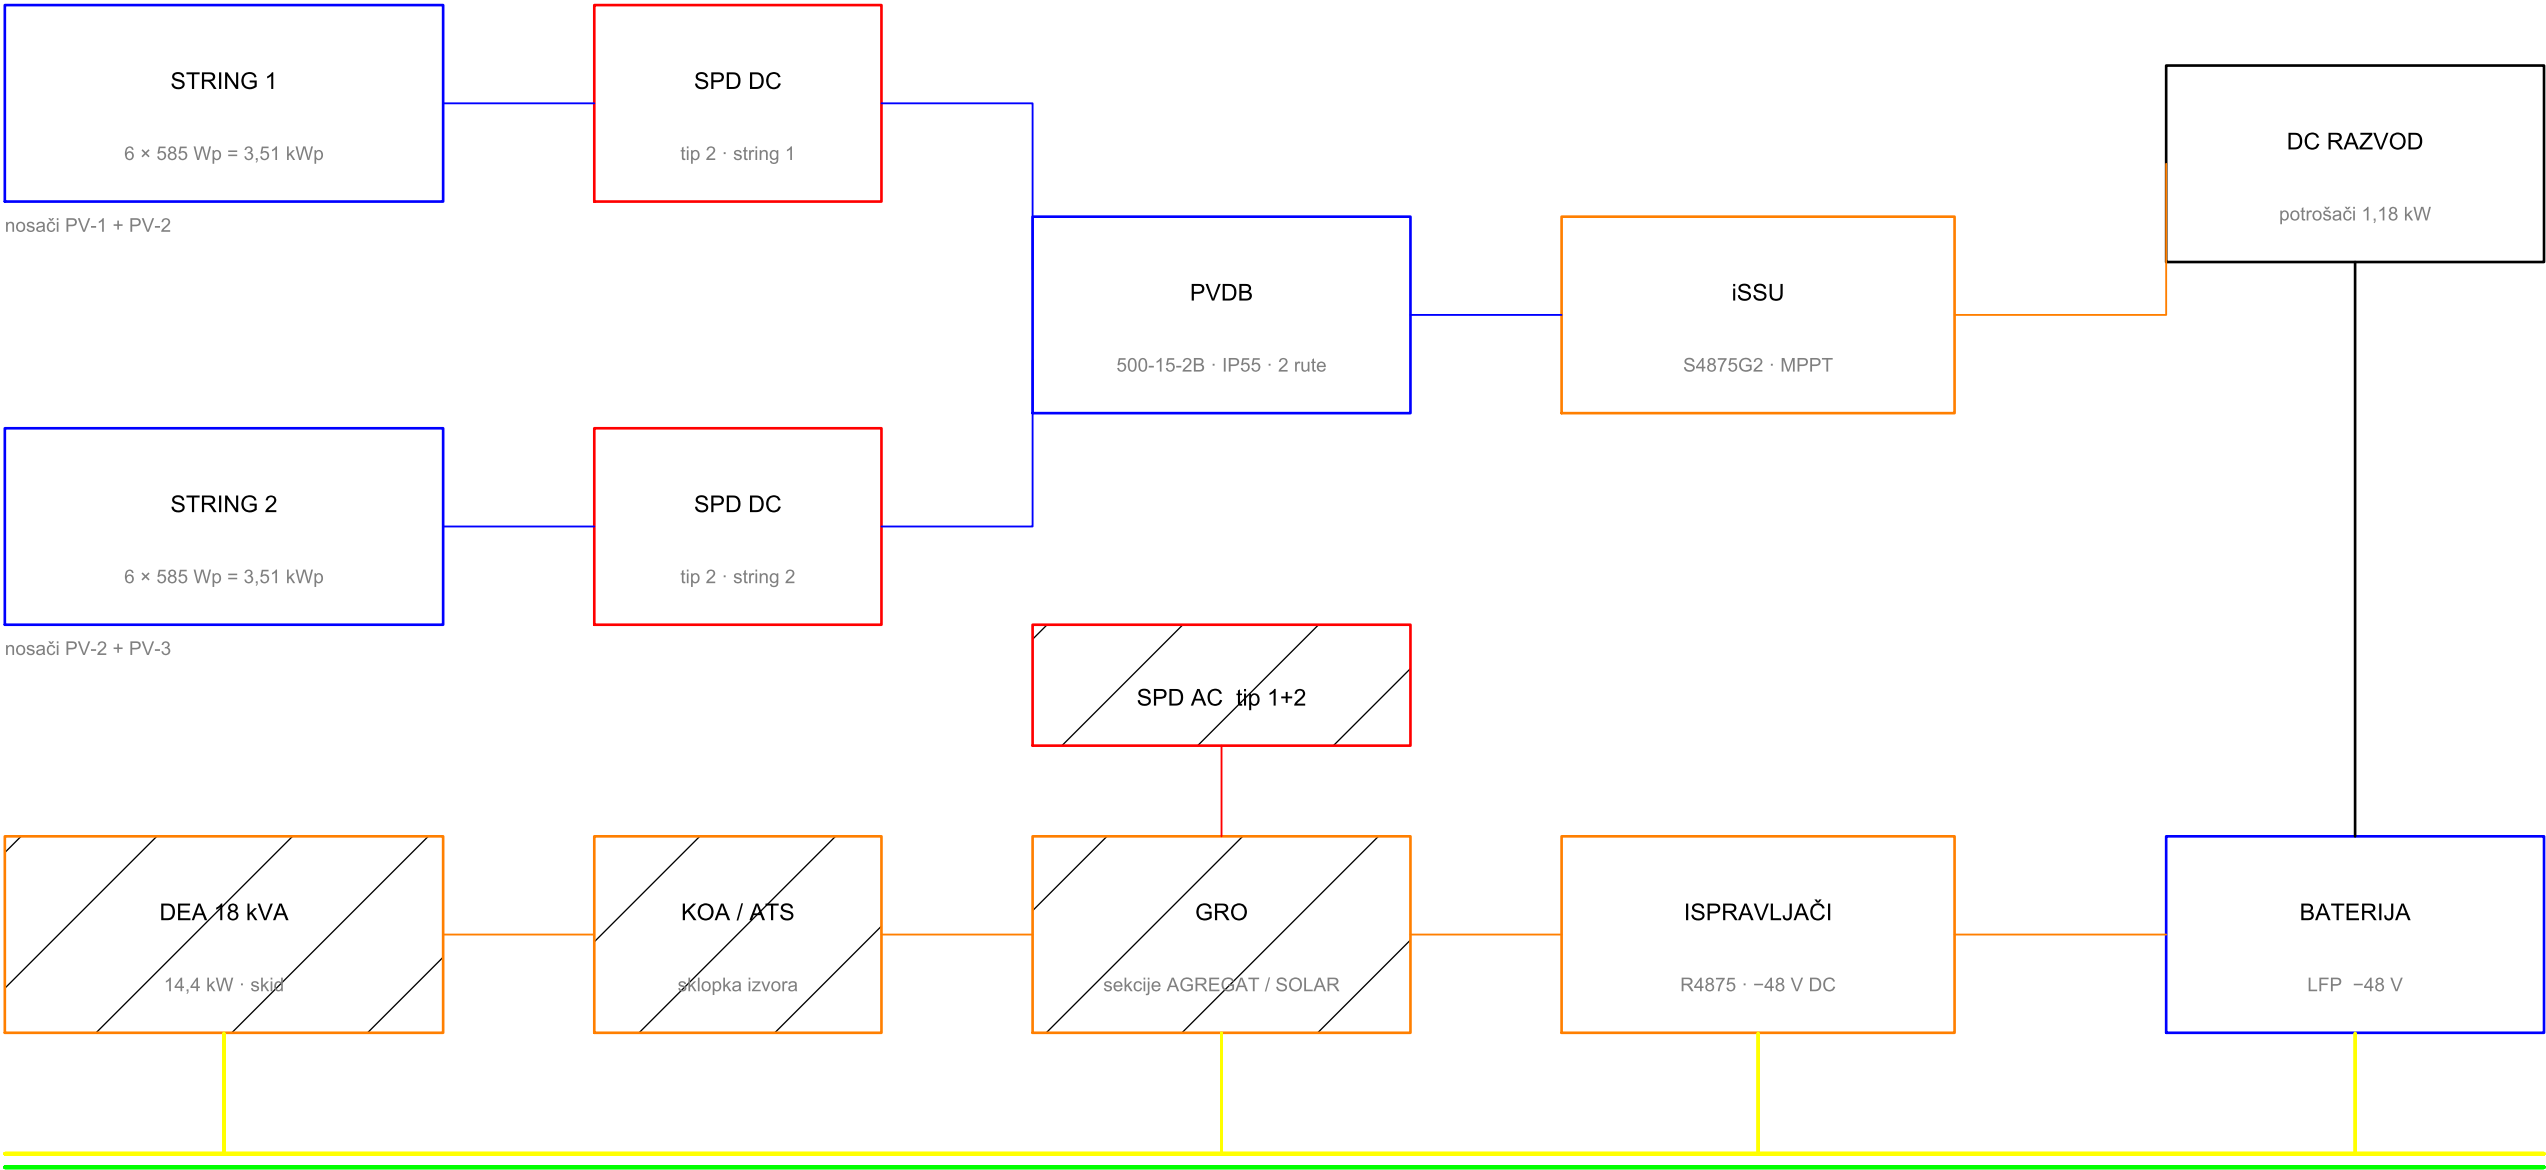

postojeći prstenasti uzemljivač Fe/Zn 25×4 · R ≤ 10 Ω · nosači FN vezani bakrenim užetom 50 mm² preko bimetalnih spojeva

- NAPOMENE:**
- 1 Lokacija NIJE na mreži — DEA je jedini AC izvor; KOA/ATS je sklopka izvora.
 - 2 Uzemljenje TN-S: spoj N-PE samo u novom GRO.
 - 3 Odvodnici: AC tip 1+2, DC tip 2 po stringu, signalni vodovi EN 61643-21.
 - 4 12 modula = 2 stringa × 6; PVDB ima 2 rute.

 isporuka i montaža — LOT 2



BH TELECOM d.d. SARAJEVO
Izvršna direkcija za tehnologiju i razvoj servisa

Investitor:
BH Telecom d.d. Sarajevo, Franca Lehara 7, Sarajevo

Objekat:
BS SJEDNICA (Bileća) — autonomni hibridni sistem napajanja

Faza:
Tenderska dokumentacija — Prilog III

Naziv crteža:
Jednopolna shema — hibridni sistem napajanja

Projektant:
Rusmir Skopljak, dipl. ing. el.

ovjerio:
Rusmir Skopljak, dipl. ing. el.

šifra projekta:
BHT-SJEDNICA-2026

razmjera:
—

godina / broj crteža:
2026. E-01