



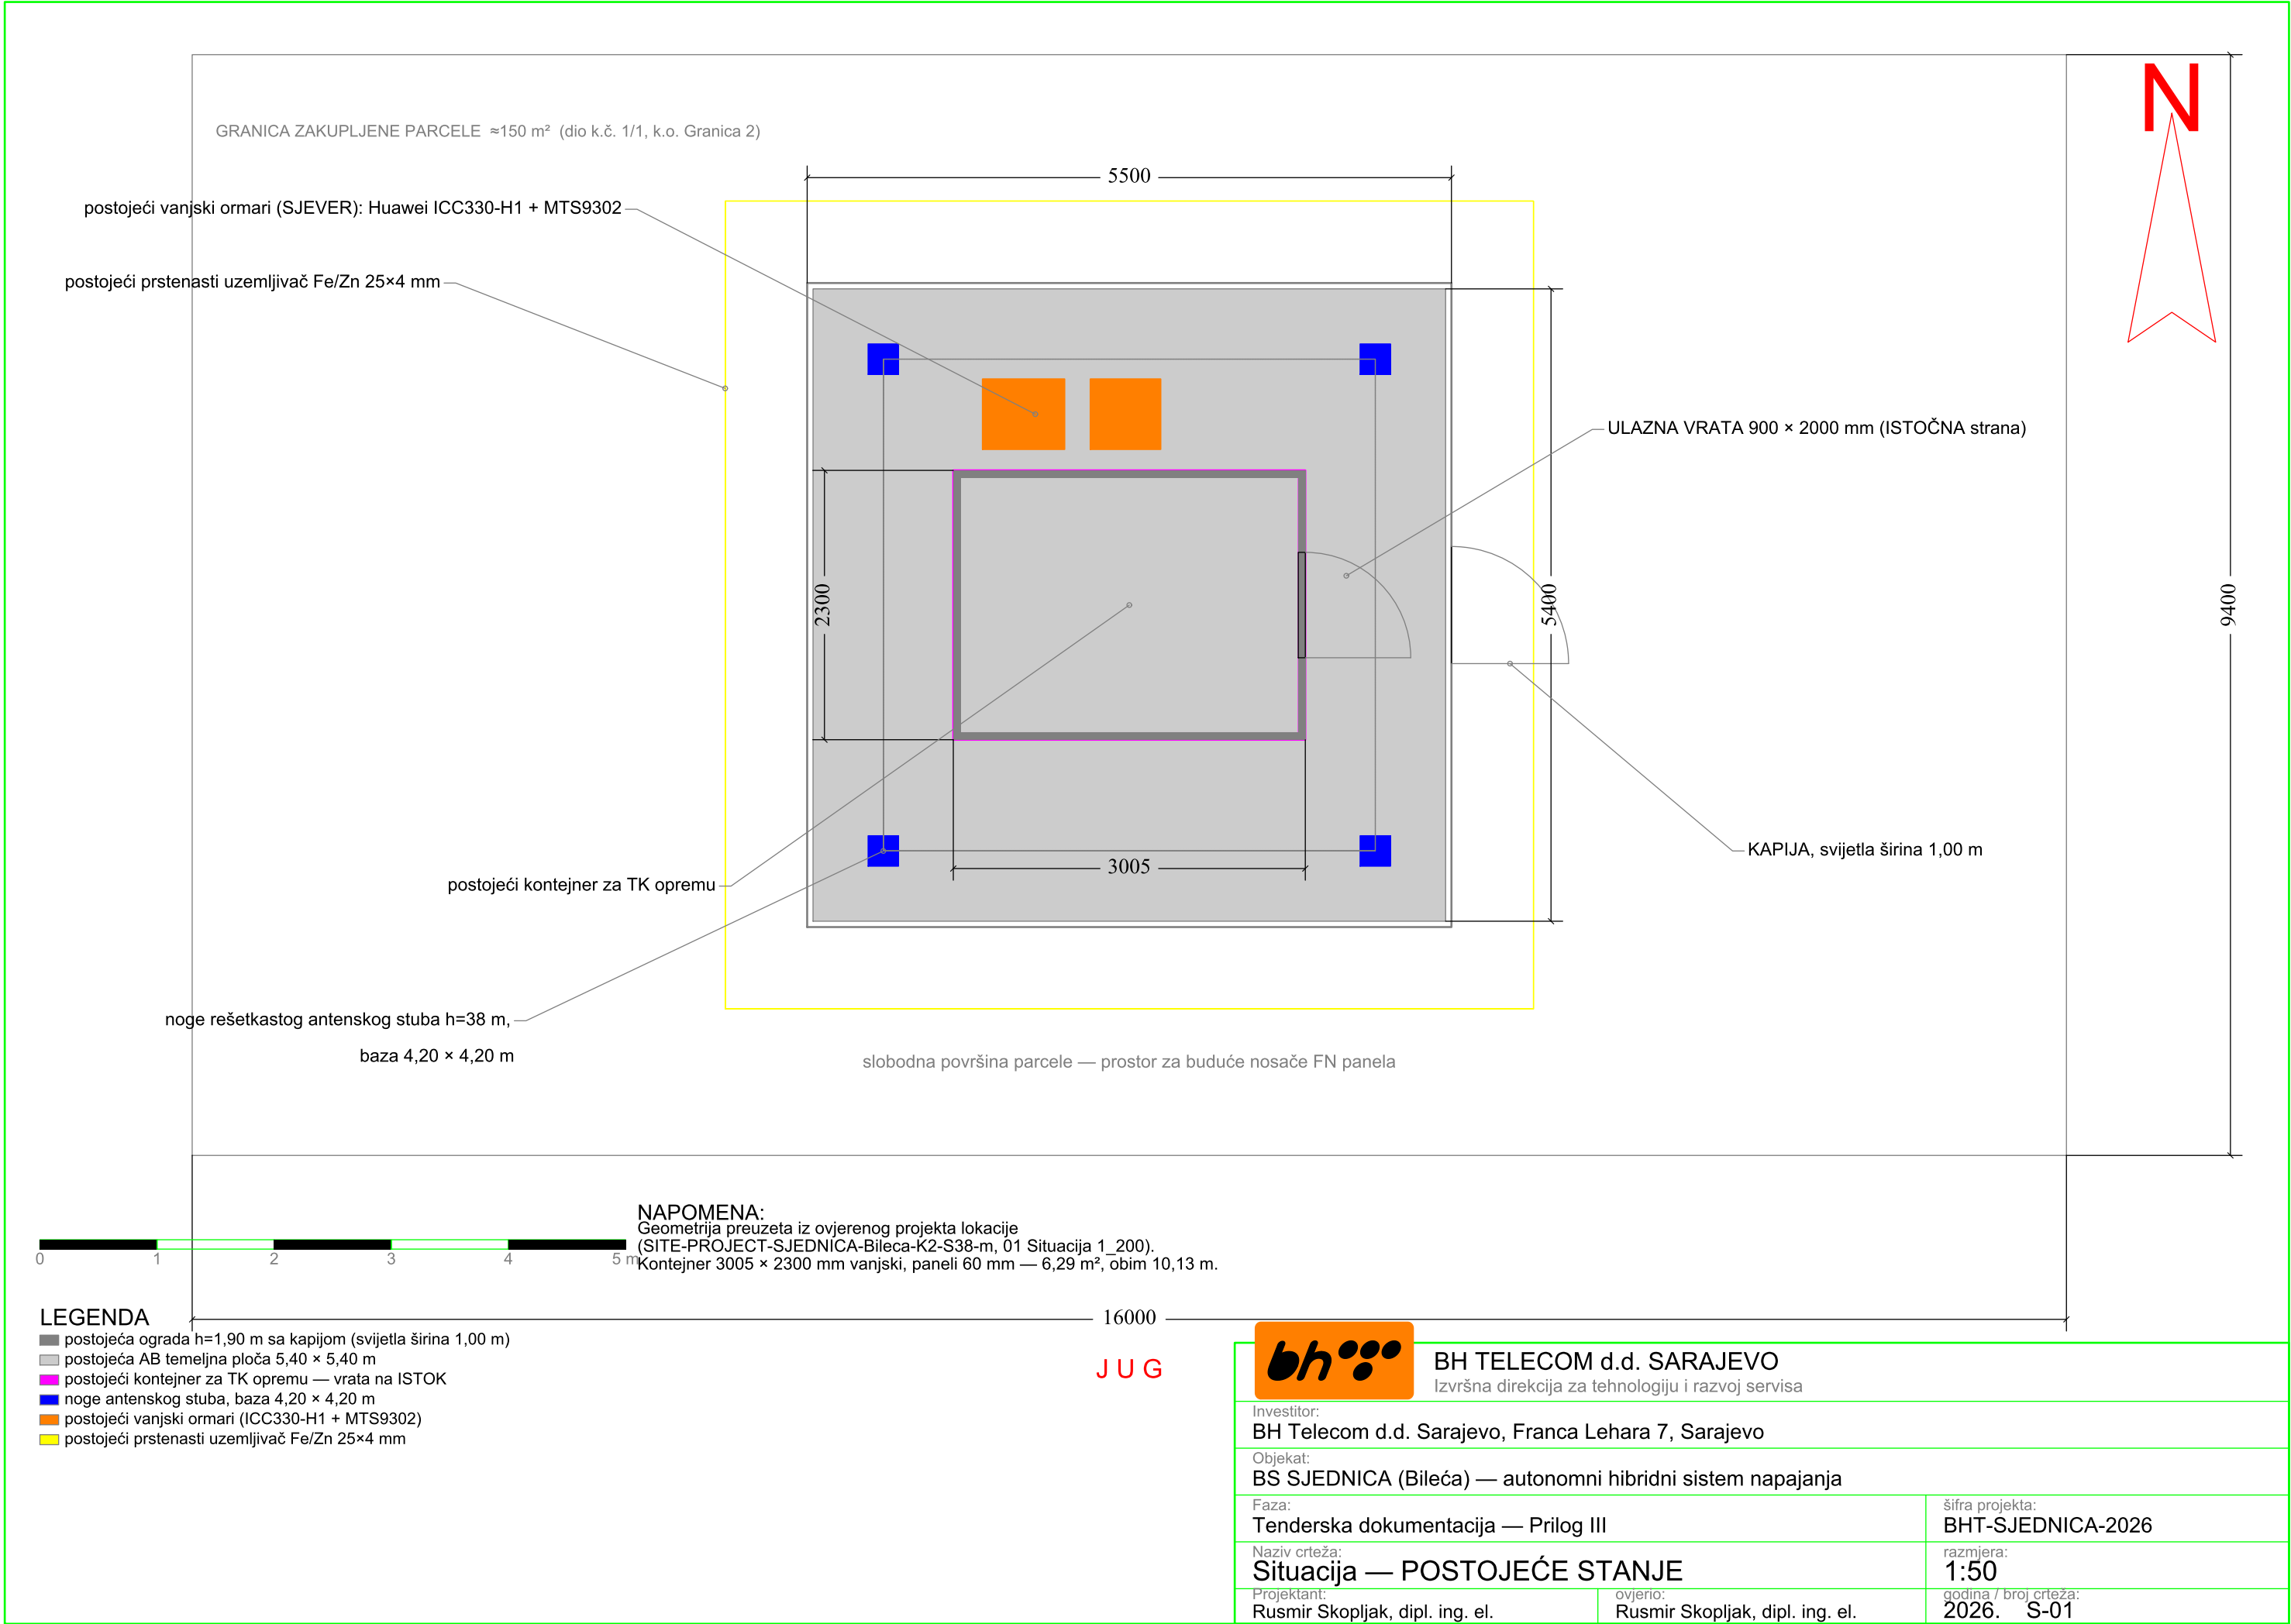

BH TELECOM d.d. SARAJEVO
Izvršna direkcija za tehnologiju i razvoj servisa

Investitor: BH Telecom d.d. Sarajevo, Franca Lehara 7, Sarajevo	
Objekat: BS SJEDNICA (Bileća) — autonomni hibridni sistem napajanja	
Faza: Tenderska dokumentacija — Prilog III	šifra projekta: BHT-SJEDNICA-2026
Naziv crteža: Situacija — POSTOJEĆE STANJE	razmjera: 1:50
Projektant: Rusmir Skopljak, dipl. ing. el.	godina / broj crteža: 2026. S-01
ovjerio: Rusmir Skopljak, dipl. ing. el.	

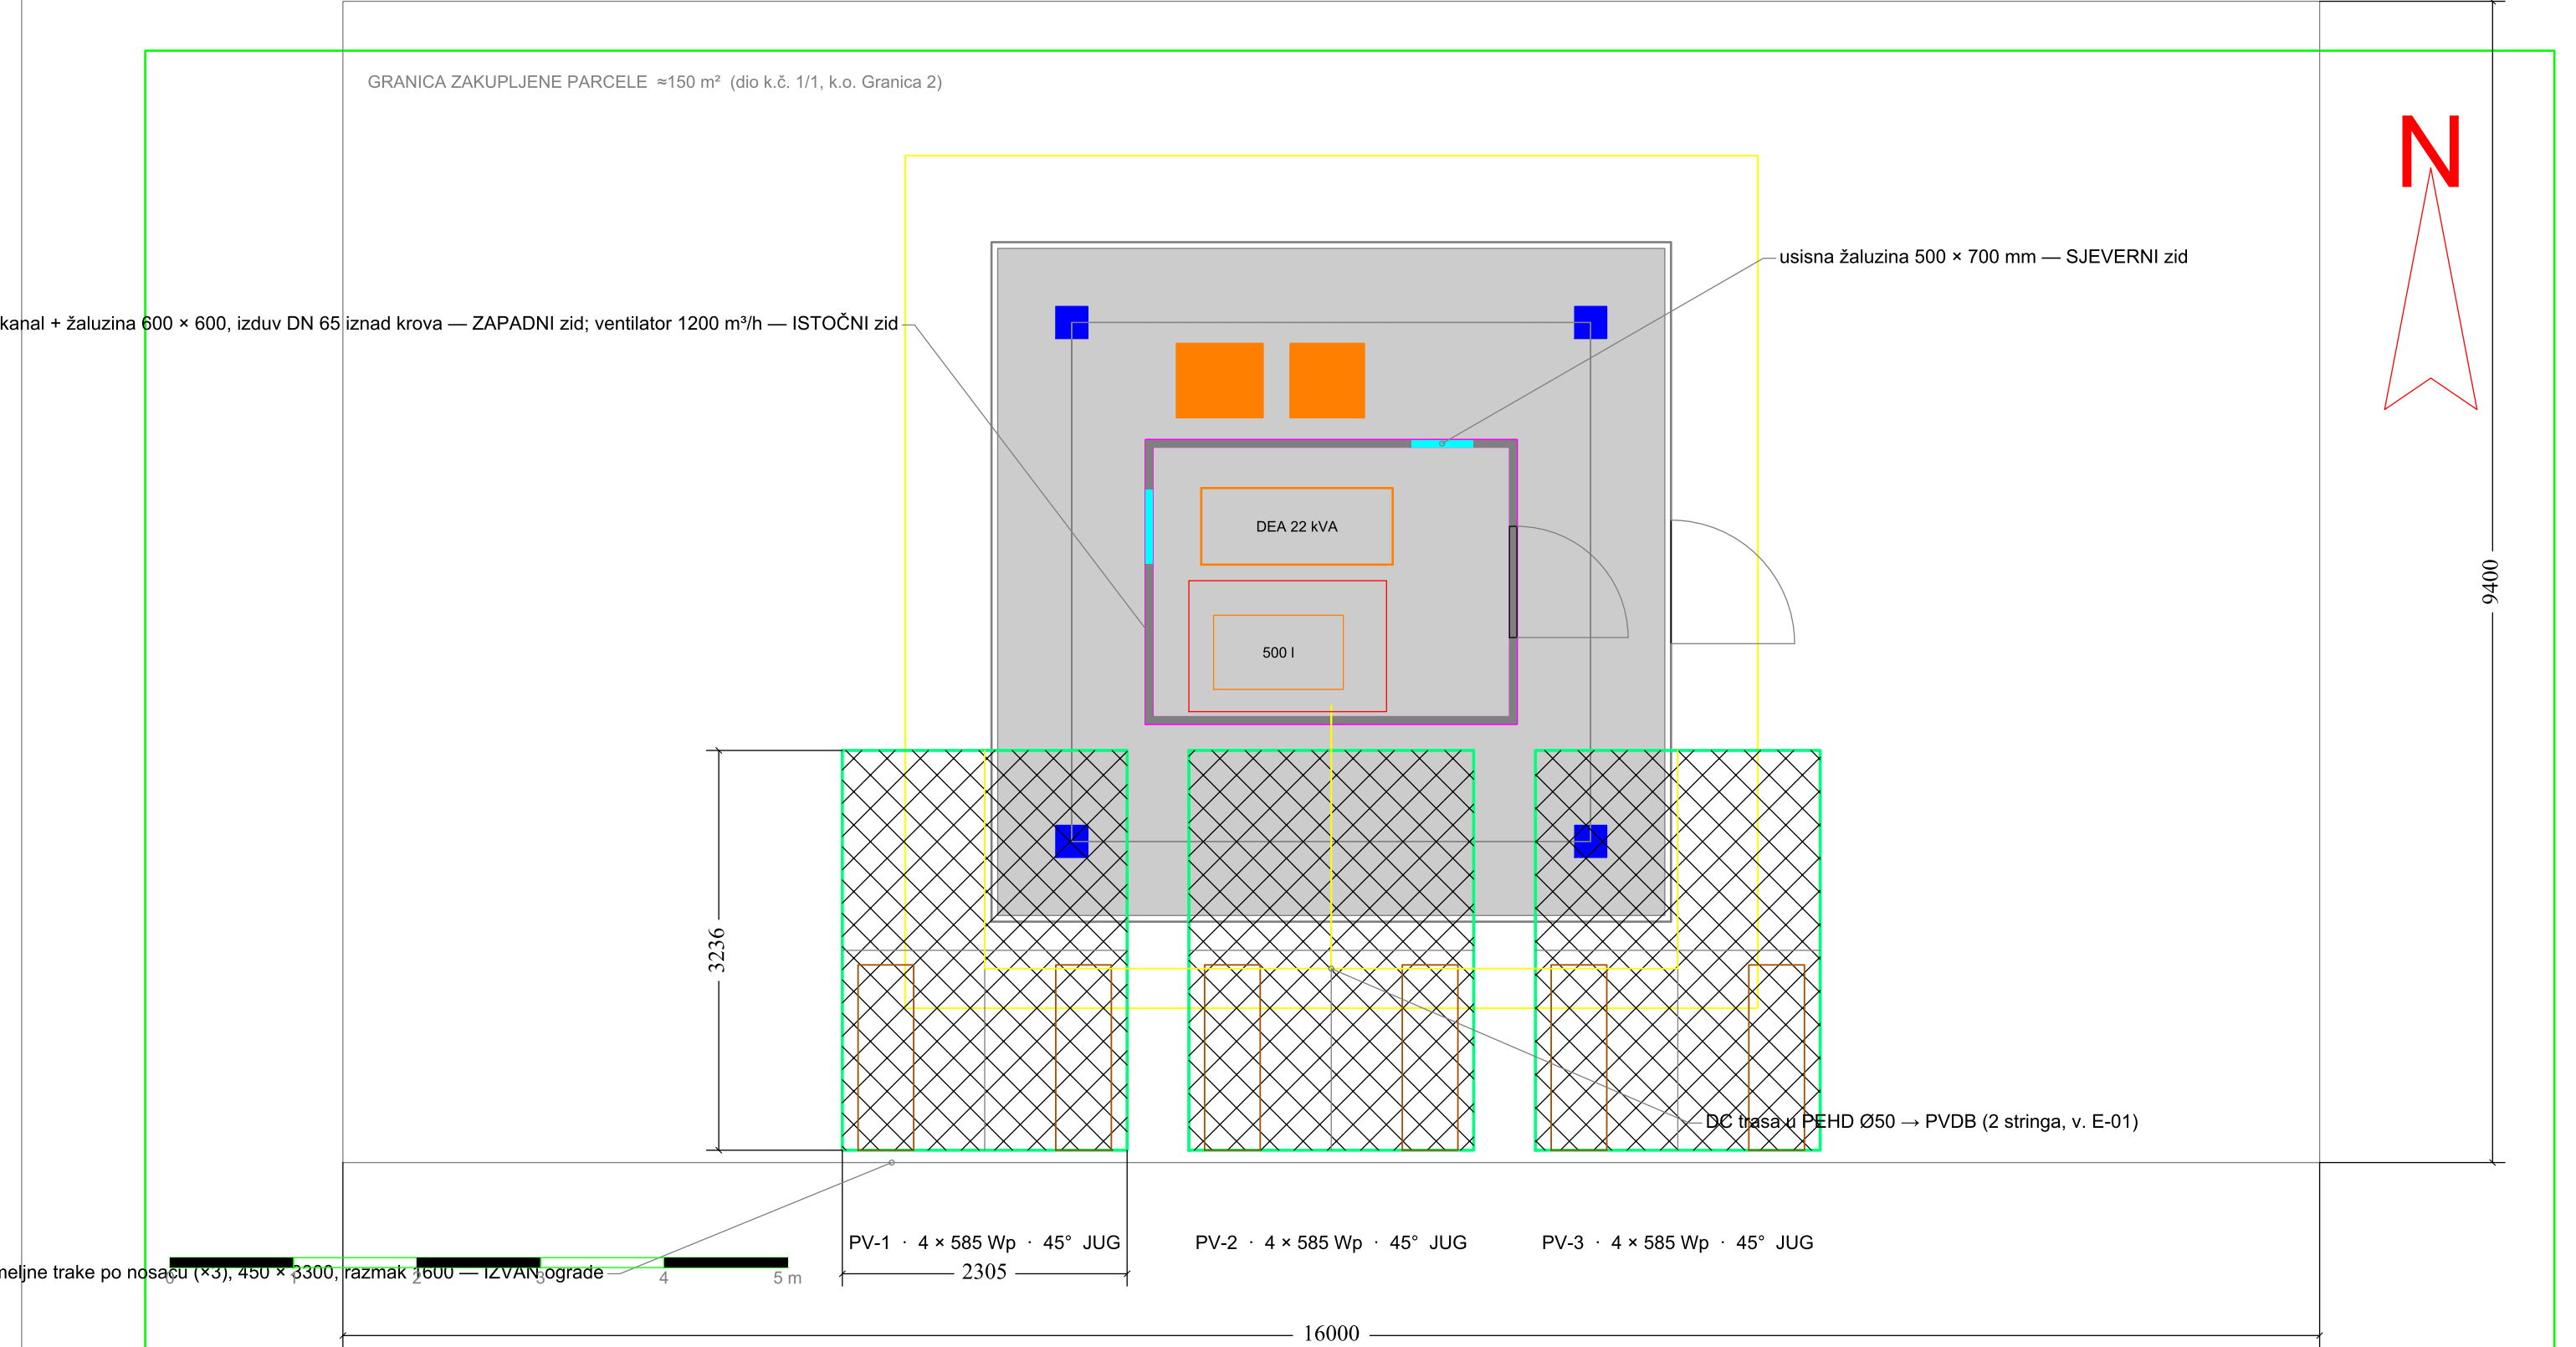

LEGENDA

- LOT 1 — nosači FN panela PV-1..PV-3 (po 4 × 585 Wp, 45°, JUG) — 2 stringa × 6
- LOT 1 — AB temeljne trake 450 × 3300 mm, razmak 1600 mm
- LOT 1 — DC trasa u PEHD Ø50 do PVDB
- LOT 2 — DEA 22 kVA u skid izvedbi i spremnik 500 l
- LOT 2 — usisna žaluzina (SJEVER); kanal, žaluzina i izduv (ZAPAD); ventilator (ISTOK)

NAPOMENA — PRORAČUNSKO OPTEREĆENJE:


Vjetar $q_p \geq 1,20 \text{ kN/m}^2$ (udar 3 s $\approx 45 \text{ m/s}$) — iznad kapaciteta kataloškog nosača tipa A, stoga CUSTOM IZRADA: sail 10,55 m²/nosaču, ULS uzgon 18,1 kN, moment prevrtanja 62,8 kNm; ovjerava ponuđač (Prilog II, 1.3).
Temelji IZVAN ograde (400 mm od kote ograde); gornja ivica panela 2836 mm iznad ograde. Kontejner je PRAZAN.




BH TELECOM d.d. SARAJEVO

Izvršna direkcija za tehnologiju i razvoj servisa

Investitor: BH Telecom d.d. Sarajevo, Franca Lehara 7, Sarajevo	
Objekat: BS SJEDNICA (Bileća) — autonomni hibridni sistem napajanja	
Faza: Tenderska dokumentacija — Prilog III	šifra projekta: BHT-SJEDNICA-2026
Naziv crteža: Situacija — BUDUĆE STANJE (LOT 1 + LOT 2)	
Projektant: Rusmir Skopljak, dipl. ing. el.	ovjerio: Rusmir Skopljak, dipl. ing. el.
godina / broj crteža: 2026. S-02	

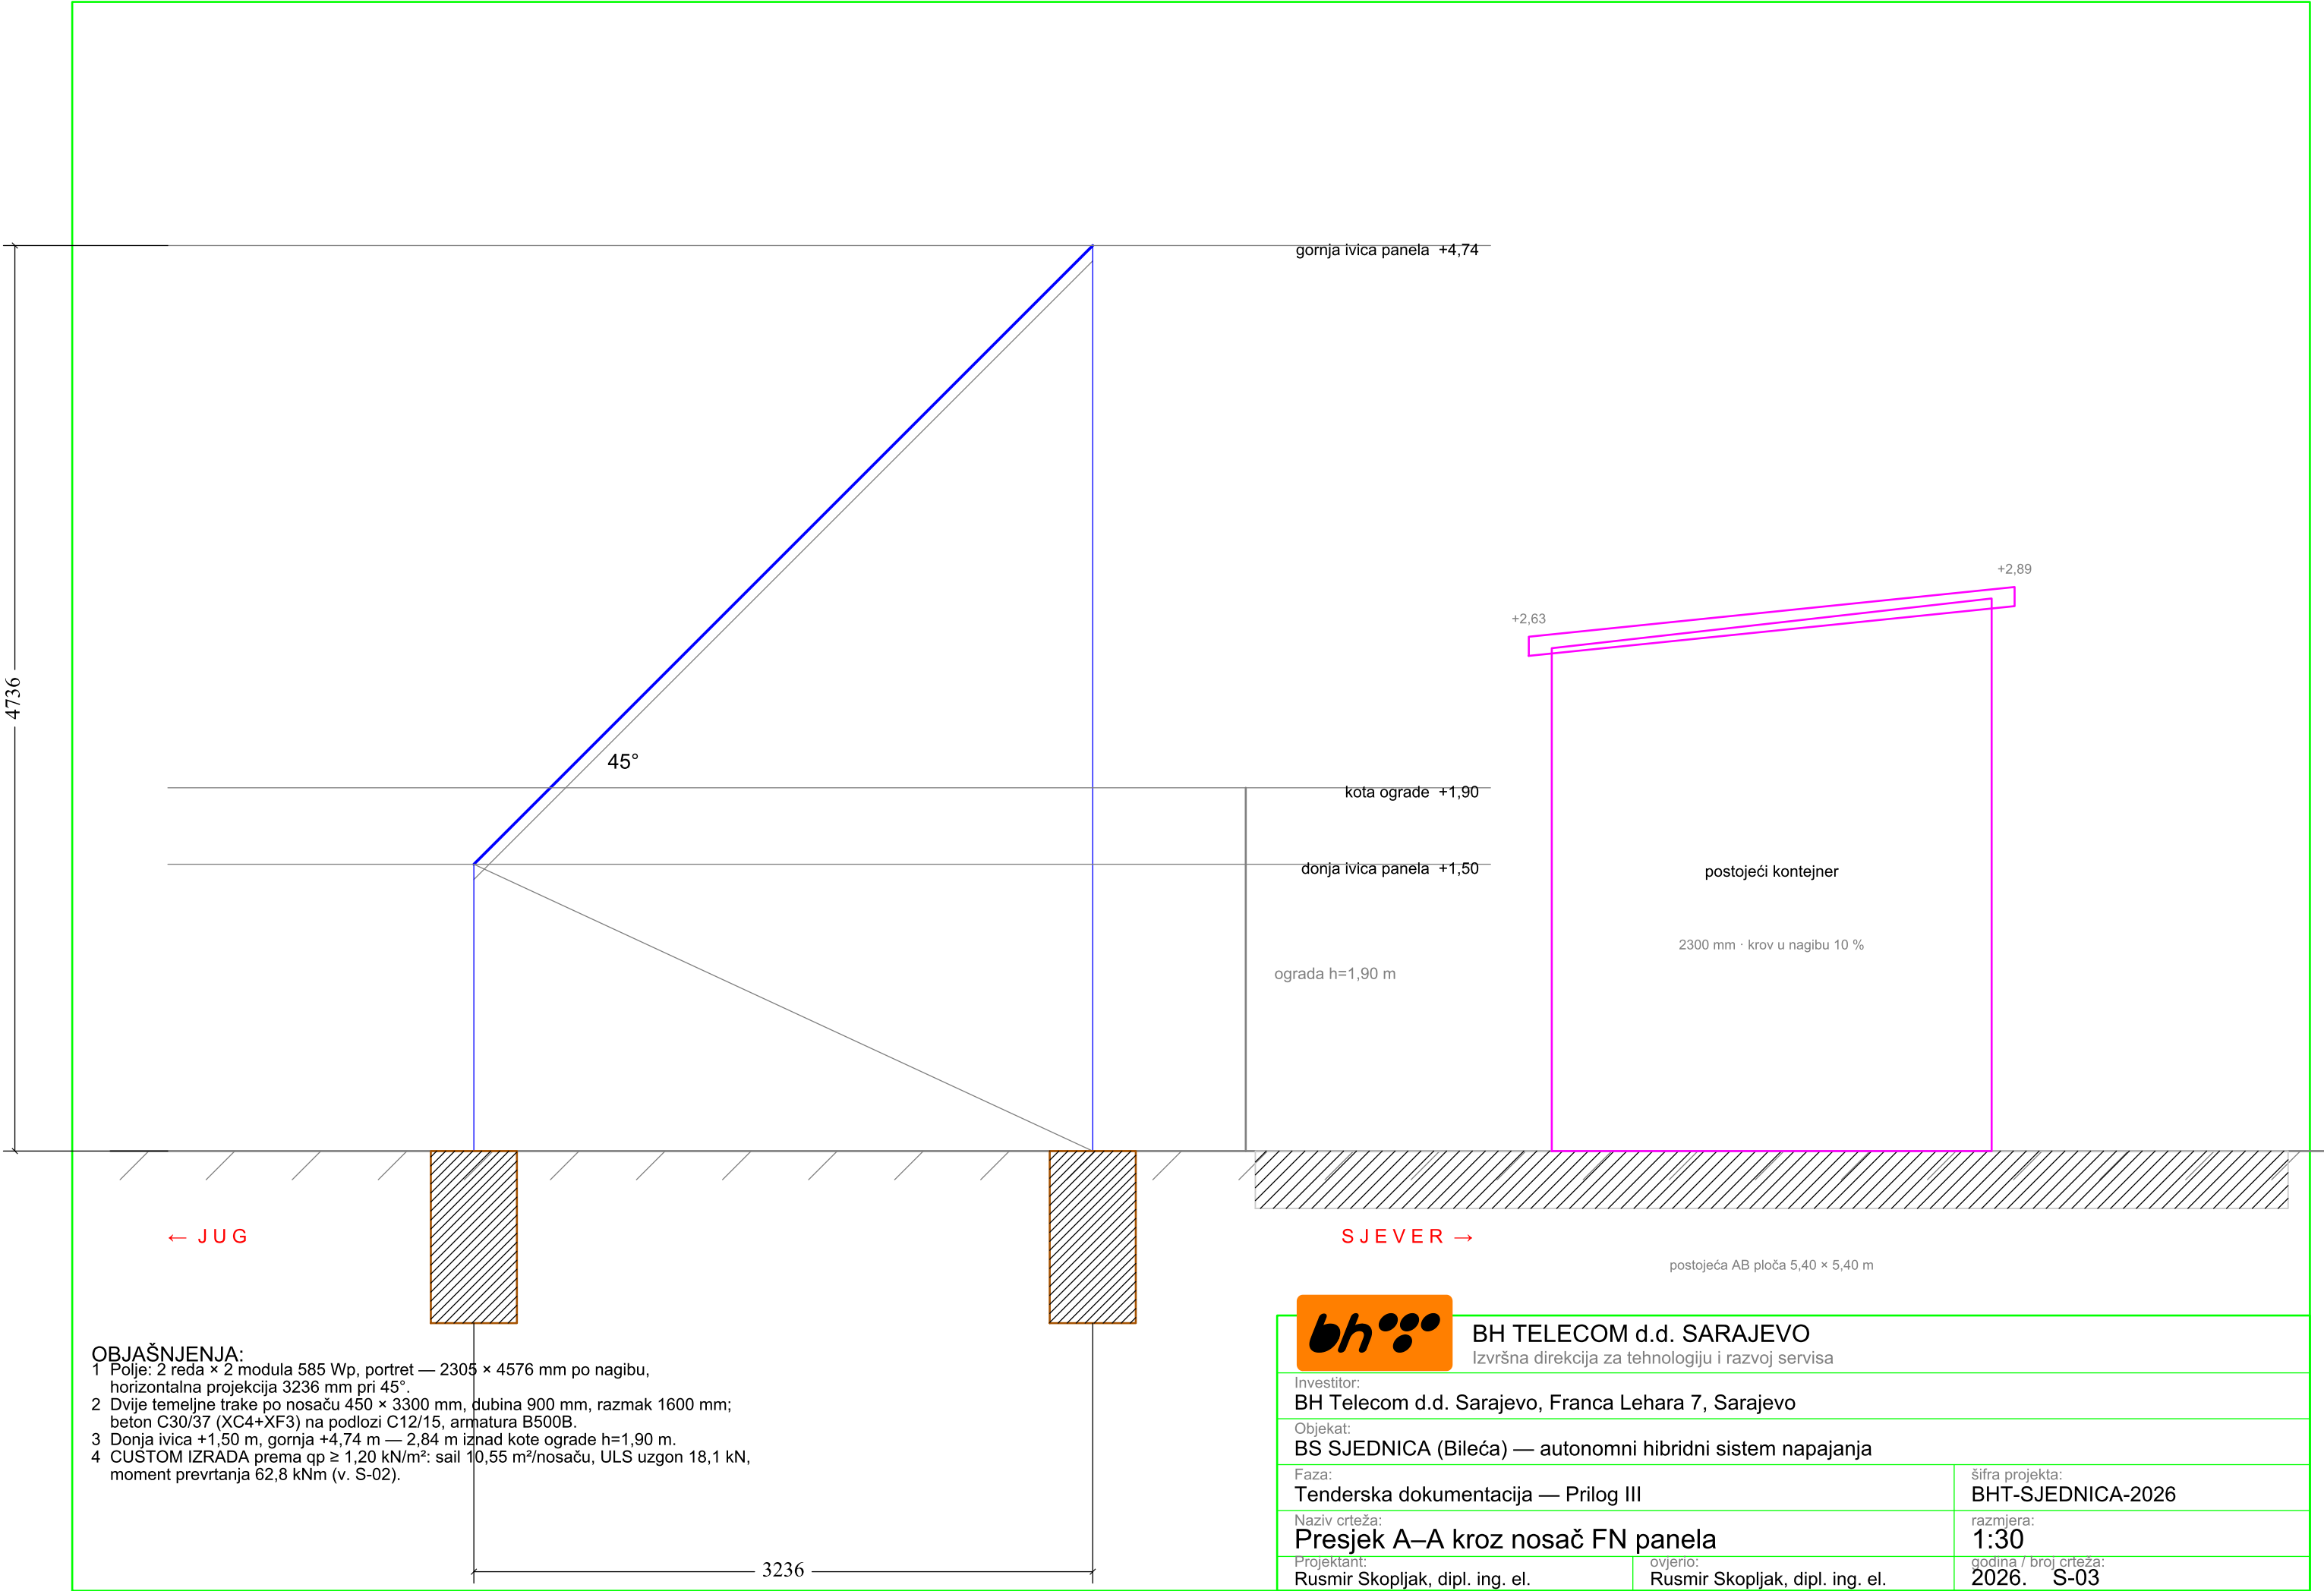

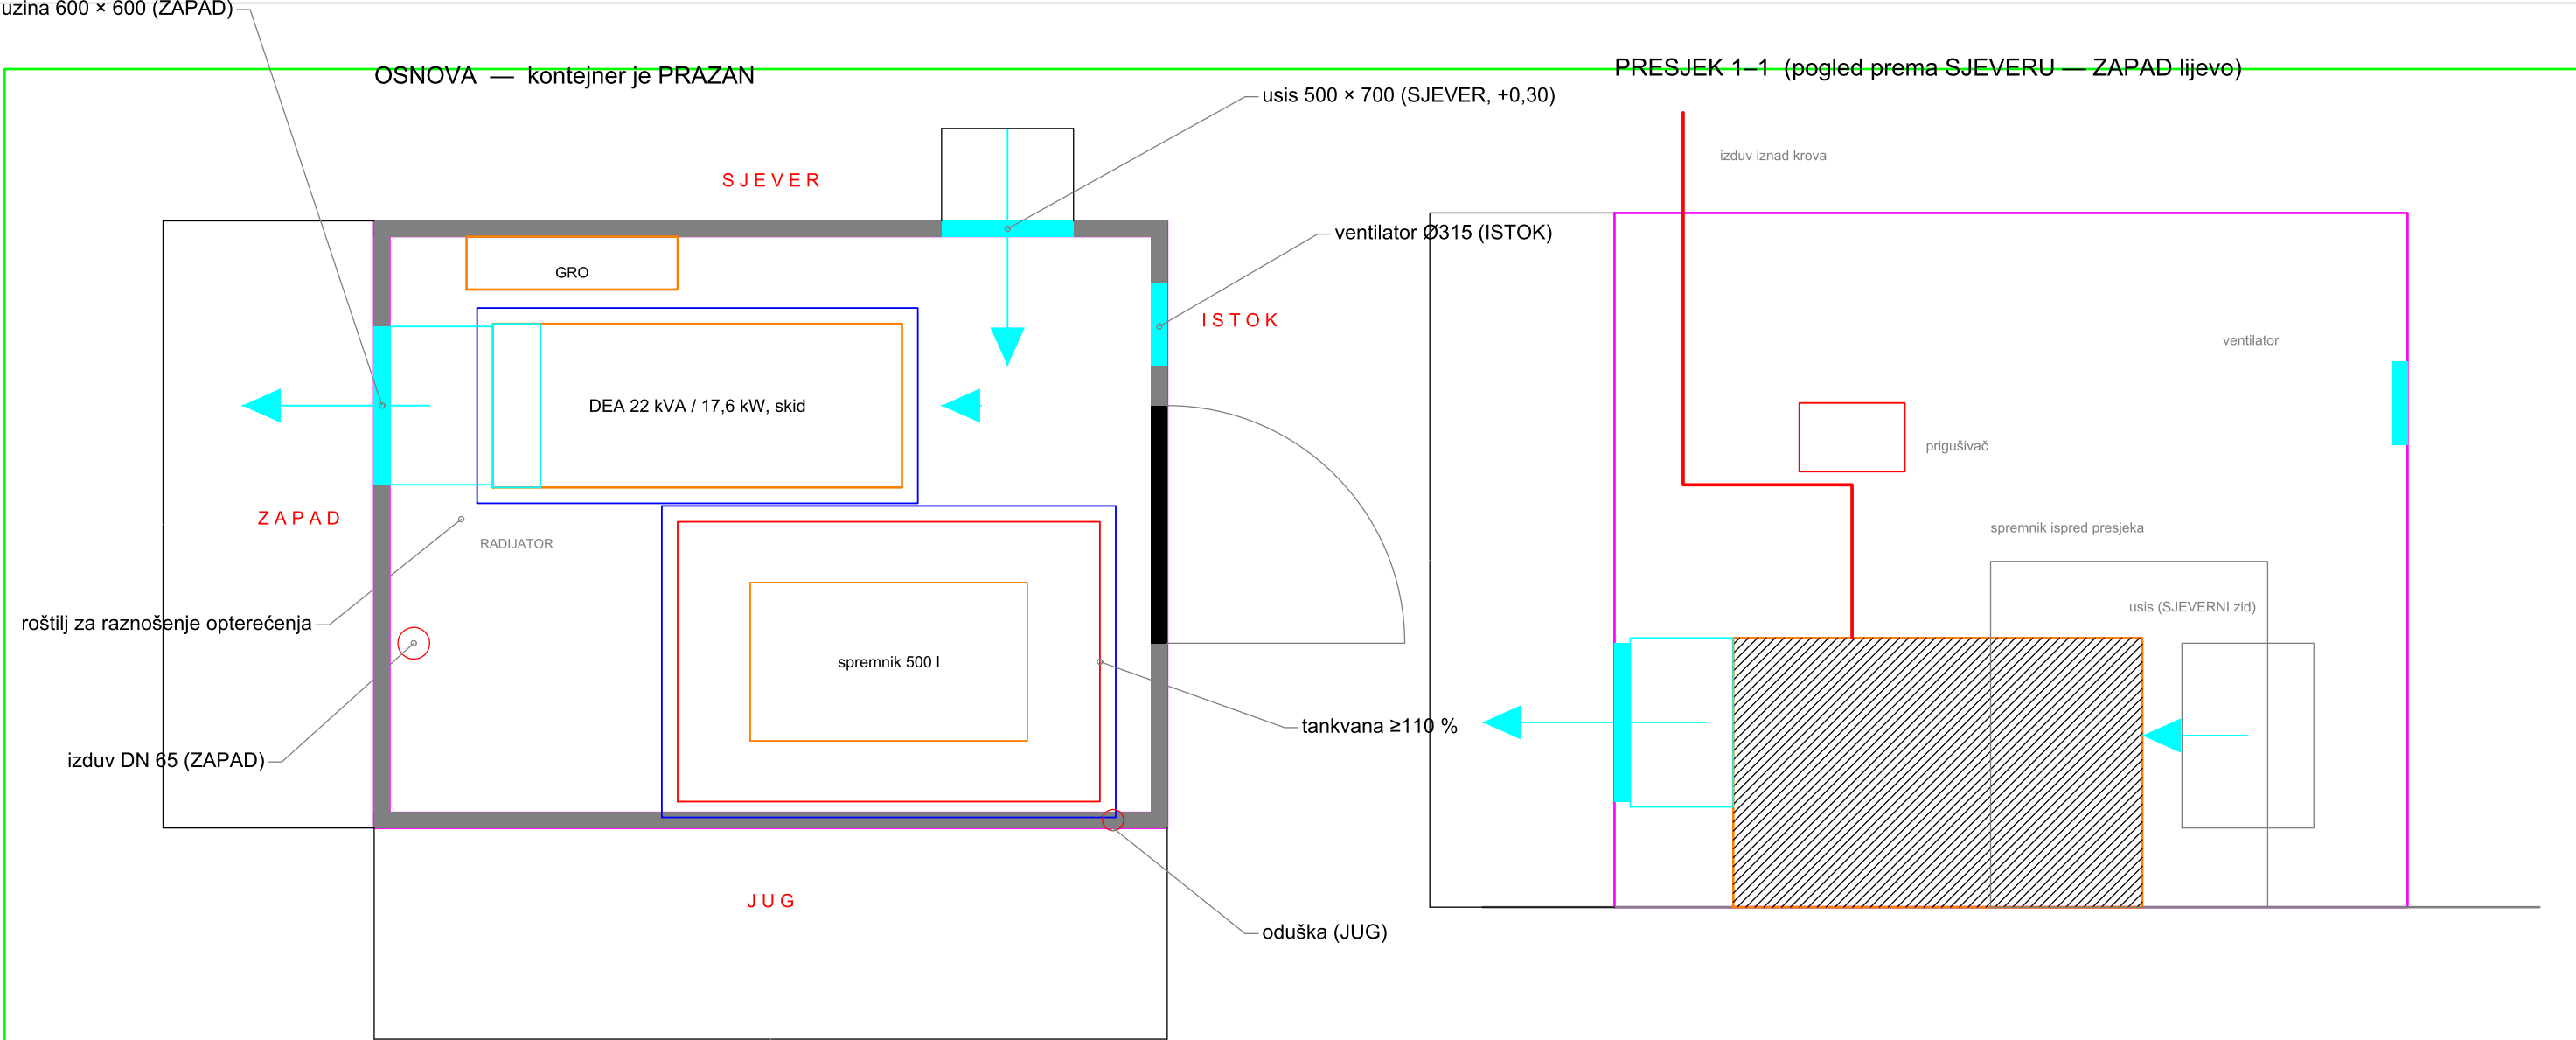

NAPOMENE:

- 1 FG Wilson P22-6 (Skid), TL 2019-08-14: hladnjak 1980 m³/h, sagorijevanje 90 m³/h, toplota u prostor 7,1 kW, maks. vanjski otpor 125 Pa.
- 2 Žaluzine zadovoljavaju: usis 500 × 700 ($\Delta p \approx 16$ Pa) + izlaz 600 × 600 (≈ 15 Pa) + kanal < 125 Pa.
- 3 Ventilator 1200 m³/h je DOPUNSKA ventilacija (min. 120 m³/h); protok hlađenja daje ventilator hladnjaka.
- 4 Izdub DN 65 usvojen (NO 50 zadovoljava protutlak, ali radi pri 33 m/s).
- 5 Pod je dimenzionisan na 10,00 kN/m² ravnomjerno raspodijeljeno (projekat lokacije, 4.4.2.3). Agregat 3,93 i pun spremnik 9,2 kN/m² su KONCENTRISANI — roštilj za raznošenje je OBAVEZAN.
- 6 RASPORED: usis SJEVER (+0,30) — zasjenjena strana, najhladniji zrak; kanal/izlaz i izdub ZAPAD, oduška JUG, ventilator ISTOK; ≥3 m između usisa, izduva i oduške. Izlaz toplog zraka i izdub NISU na sjevernoj strani, pa se ormari ICC330-H1/MTS9302 ne griju.
- 7 GRO na SJEVERNOM zidu, uz vanjske ormare koje napaja (najkraća trasa).
- 8 UNOS: skid 620 mm kroz vrata 900 mm. Kontejner je PRAZAN.



BH TELECOM d.d. SARAJEVO
Izvršna direkcija za tehnologiju i razvoj servisa

Investitor:
BH Telecom d.d. Sarajevo, Franca Lehara 7, Sarajevo

Objekat:
BS SJEDNICA (Bileća) — autonomni hibridni sistem napajanja

Faza:
Tenderska dokumentacija — Prilog III

šifra projekta:
BHT-SJEDNICA-2026


Naziv crteža:
DEA u postojećem kontejneru — osnova i presjek

razmjera:
1:25

Projektant:
Rusmir Skopljak, dipl. ing. el.

ovjerio:
Rusmir Skopljak, dipl. ing. el.

godina / broj crteža:
2026. M-01

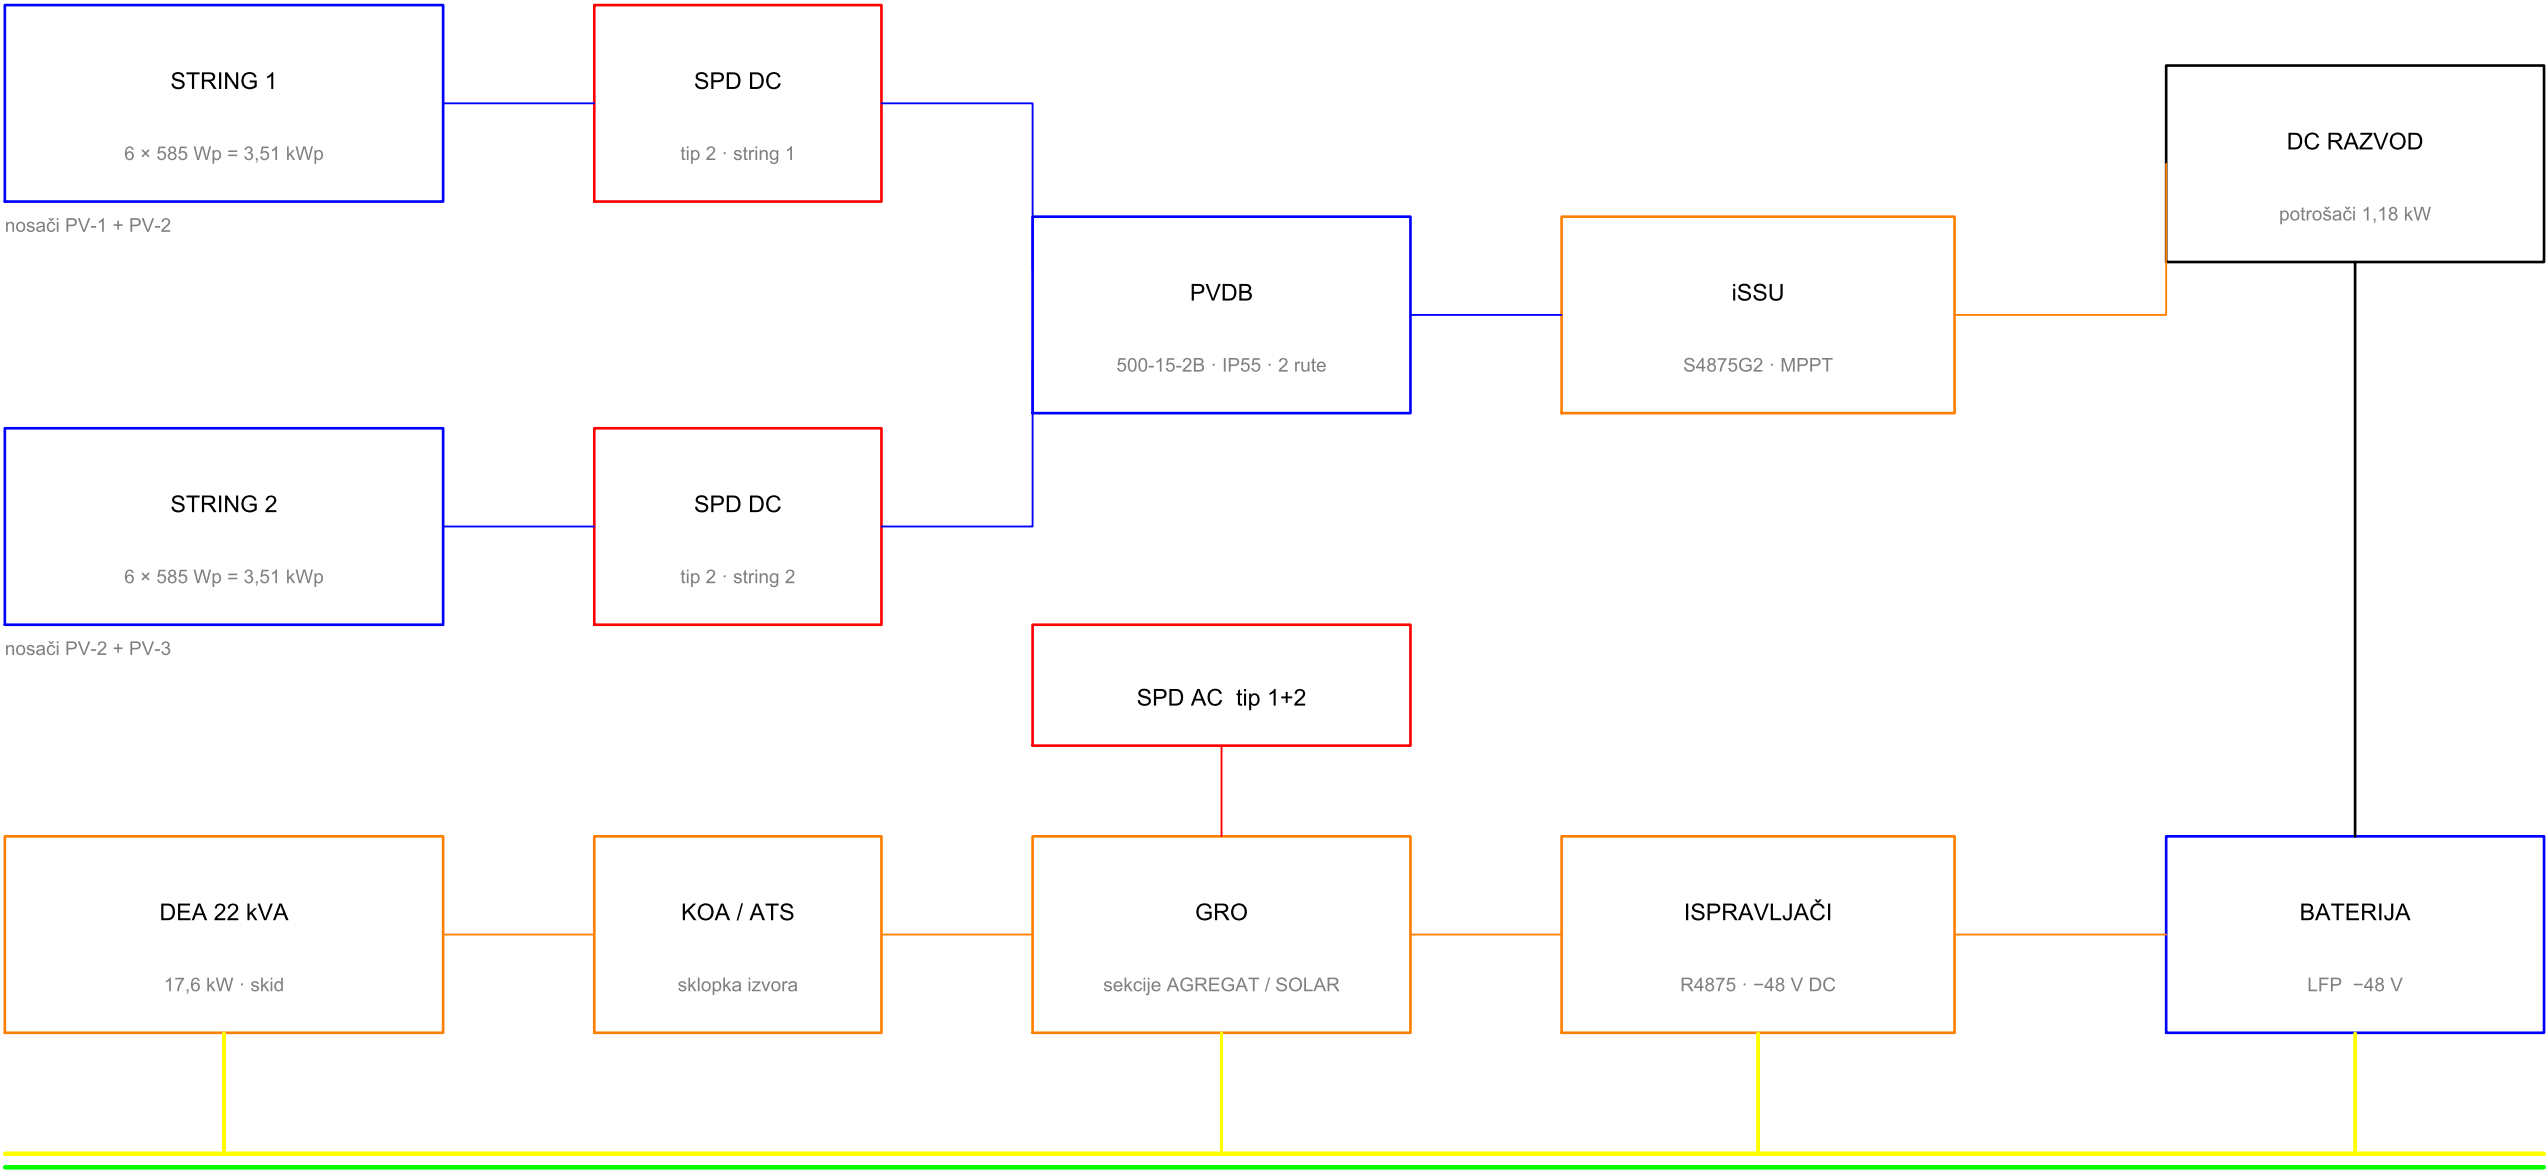

postojeći prstenasti uzemljivač Fe/Zn 25×4 · R ≤ 10 Ω · nosači FN vezani bakrenim užetom 50 mm² preko bimetalnih spojeva

NAPOMENE:

- 1 Lokacija NIJE na mreži — DEA je jedini AC izvor; KOA/ATS je sklopka izvora, ne prebacivanje sa mreže.
- 2 Uzemljenje otočnog izvora TN-S: tačka spajanja N-PE u novom GRO, ne u postojećem PMO.
- 3 Prenaponska zaštita: AC tip 1+2 (objekat ima LPS), DC tip 2 po stringu, signalni vodovi EN 61643-21.
- 4 Zaštita u GRO mora isključiti prema IEC 60364-4-41 pri struji kvara ograničenoj pobudom generatora.
- 5 FN polja su unutar zone zaštite antenskog stuba h=38 m (EN 62305).
- 6 12 modula = 2 stringa × 6 (na 3 nosača × 4); PVDB ima 2 rute, po jedan DC odvodnik po stringu.



BH TELECOM d.d. SARAJEVO
Izvršna direkcija za tehnologiju i razvoj servisa

Investitor:
BH Telecom d.d. Sarajevo, Franca Lehara 7, Sarajevo

Objekat:
BS SJEDNICA (Bileća) — autonomni hibridni sistem napajanja

Faza:
Tenderska dokumentacija — Prilog III

Naziv crteža:
Jednopolna shema — hibridni sistem napajanja

Projektant:
Rusmir Skopljak, dipl. ing. el.

ovjerio:
Rusmir Skopljak, dipl. ing. el.

šifra projekta:
BHT-SJEDNICA-2026

razmjera:
—

godina / broj crteža:
2026. E-01