


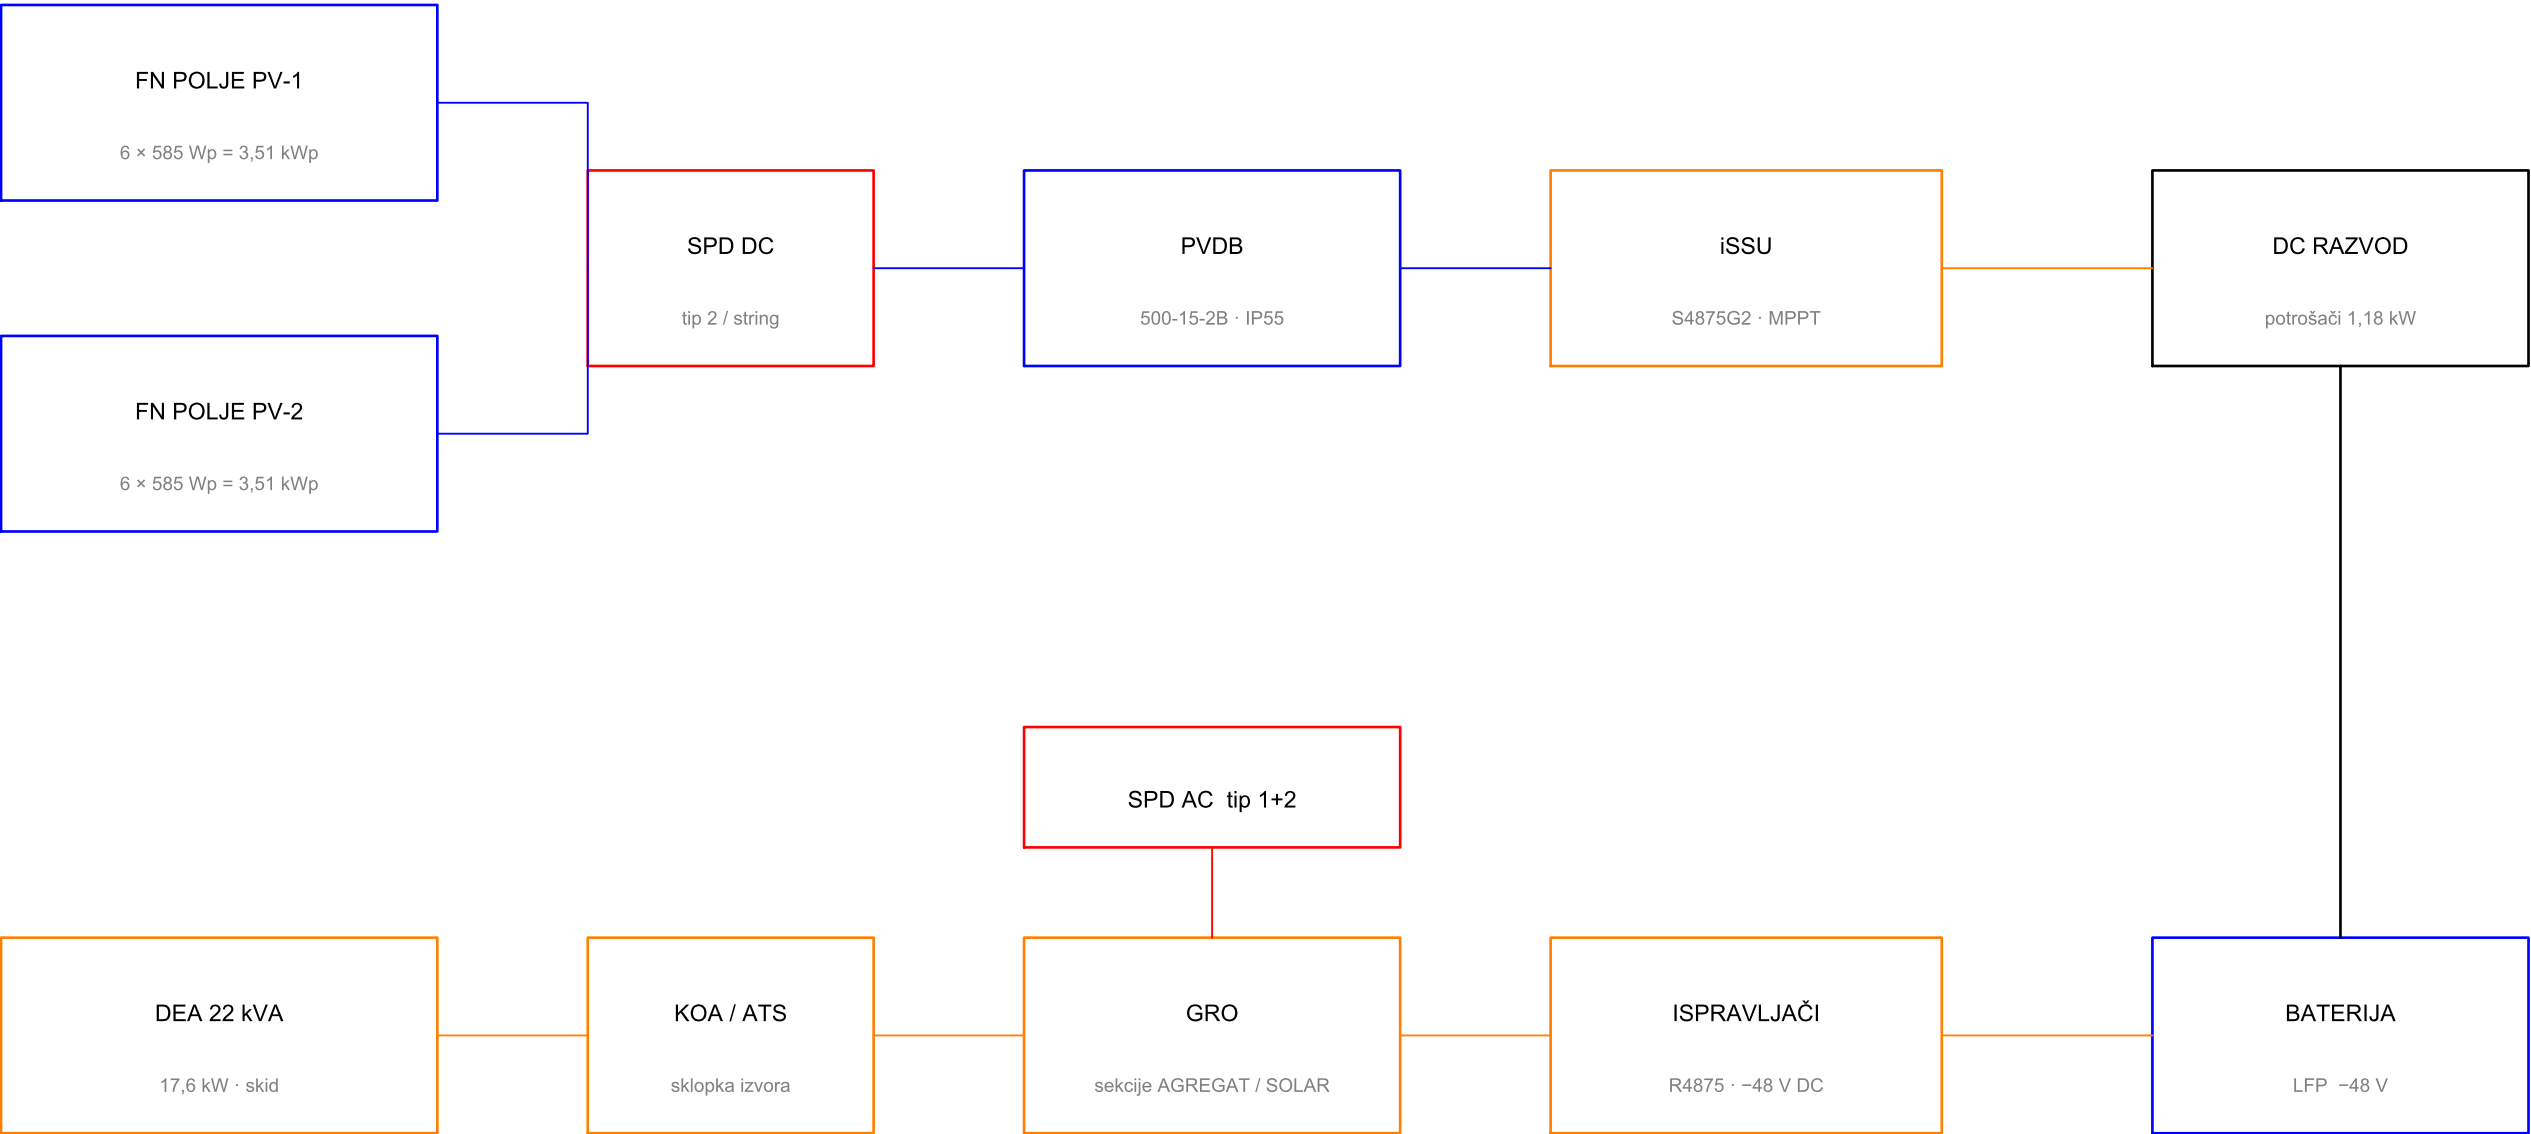

postojeći prstenasti uzemljivač Fe/Zn 25×4 · R ≤ 10 Ω · nosači FN vezani bakrenim užetom 50 mm² preko bimetalnih spojeva

- NAPOMENE:**
- 1 Lokacija NIJE priključena na elektroenergetsku mrežu — DEA je jedini AC izvor, te KOA/ATS radi kao sklopka izvora, a ne kao prebacivanje sa mreže.
 - 2 Sistem uzemljenja otočnog izvora (TN-S) definisati projektom: tačka spajanja N-PE je u novom GRO, a ne u postojećem PMO koji više nema izvor napajanja.
 - 3 Prenaponska zaštita: tip 1+2 na AC strani (objekat ima vanjski LPS), tip 2 po stringu na DC strani, te zaštita signalnih vodova prema EN 62305-4.
 - 4 Zaštitni uređaj u GRO mora obezbijediti automatsko isključenje prema IEC 60364-4-41 pri struji kvara ograničenoj SHUNT pobudom generatora.
 - 5 FN polja su unutar zone zaštite antenskog stuba h=38 m prema EN 62305.



BH TELECOM d.d. SARAJEVO

Izvršna direkcija za tehnologiju i razvoj servisa

Investitor:
BH Telecom d.d. Sarajevo, Franca Lehara 7, Sarajevo

Objekat:
BS SJEDNICA (Bileća) — autonomni hibridni sistem napajanja

Faza:
Tenderska dokumentacija — Prilog III

Naziv crteža:
Jednopolna shema — hibridni sistem napajanja

Projektant:
Rusmir Skopljak, dipl. ing. el.

ovjerio:
Rusmir Skopljak, dipl. ing. el.

šifra projekta:
BHT-SJEDNICA-2026

razmjera:
—

godina / broj crteža:
2026. E-01