


OBJAŠNJENJA:

1. Polje FN panela: 2 reda × 3 modula 585 Wp u portretu — širina polja 3476 mm, dužina po nagibu 4576 mm (2 × 2278 mm), horizontalna projekcija 3236 mm pri 45°. ISPRAVLJENO: raniji nacrt je projekciju izvodio iz uzdužne grede 3656 mm (2590 mm), što nije dužina polja modula. Gornja ivica je stoga na +3,74 m.
2. Dvije temeljne trake po nosaču, 450 × 3300 mm, dubina 900 mm, razmak 2600 mm, beton C25 na podlozi C10; dubina i armatura prema ovjerenom proračunu.
3. Gornja (sjeverna) ivica panela je 1,84 m iznad kote ograde h=1,90 m.
4. MJERODAVNO: qp ≥ 1,20 kN/m² — vidjeti napomenu na listu S-02.

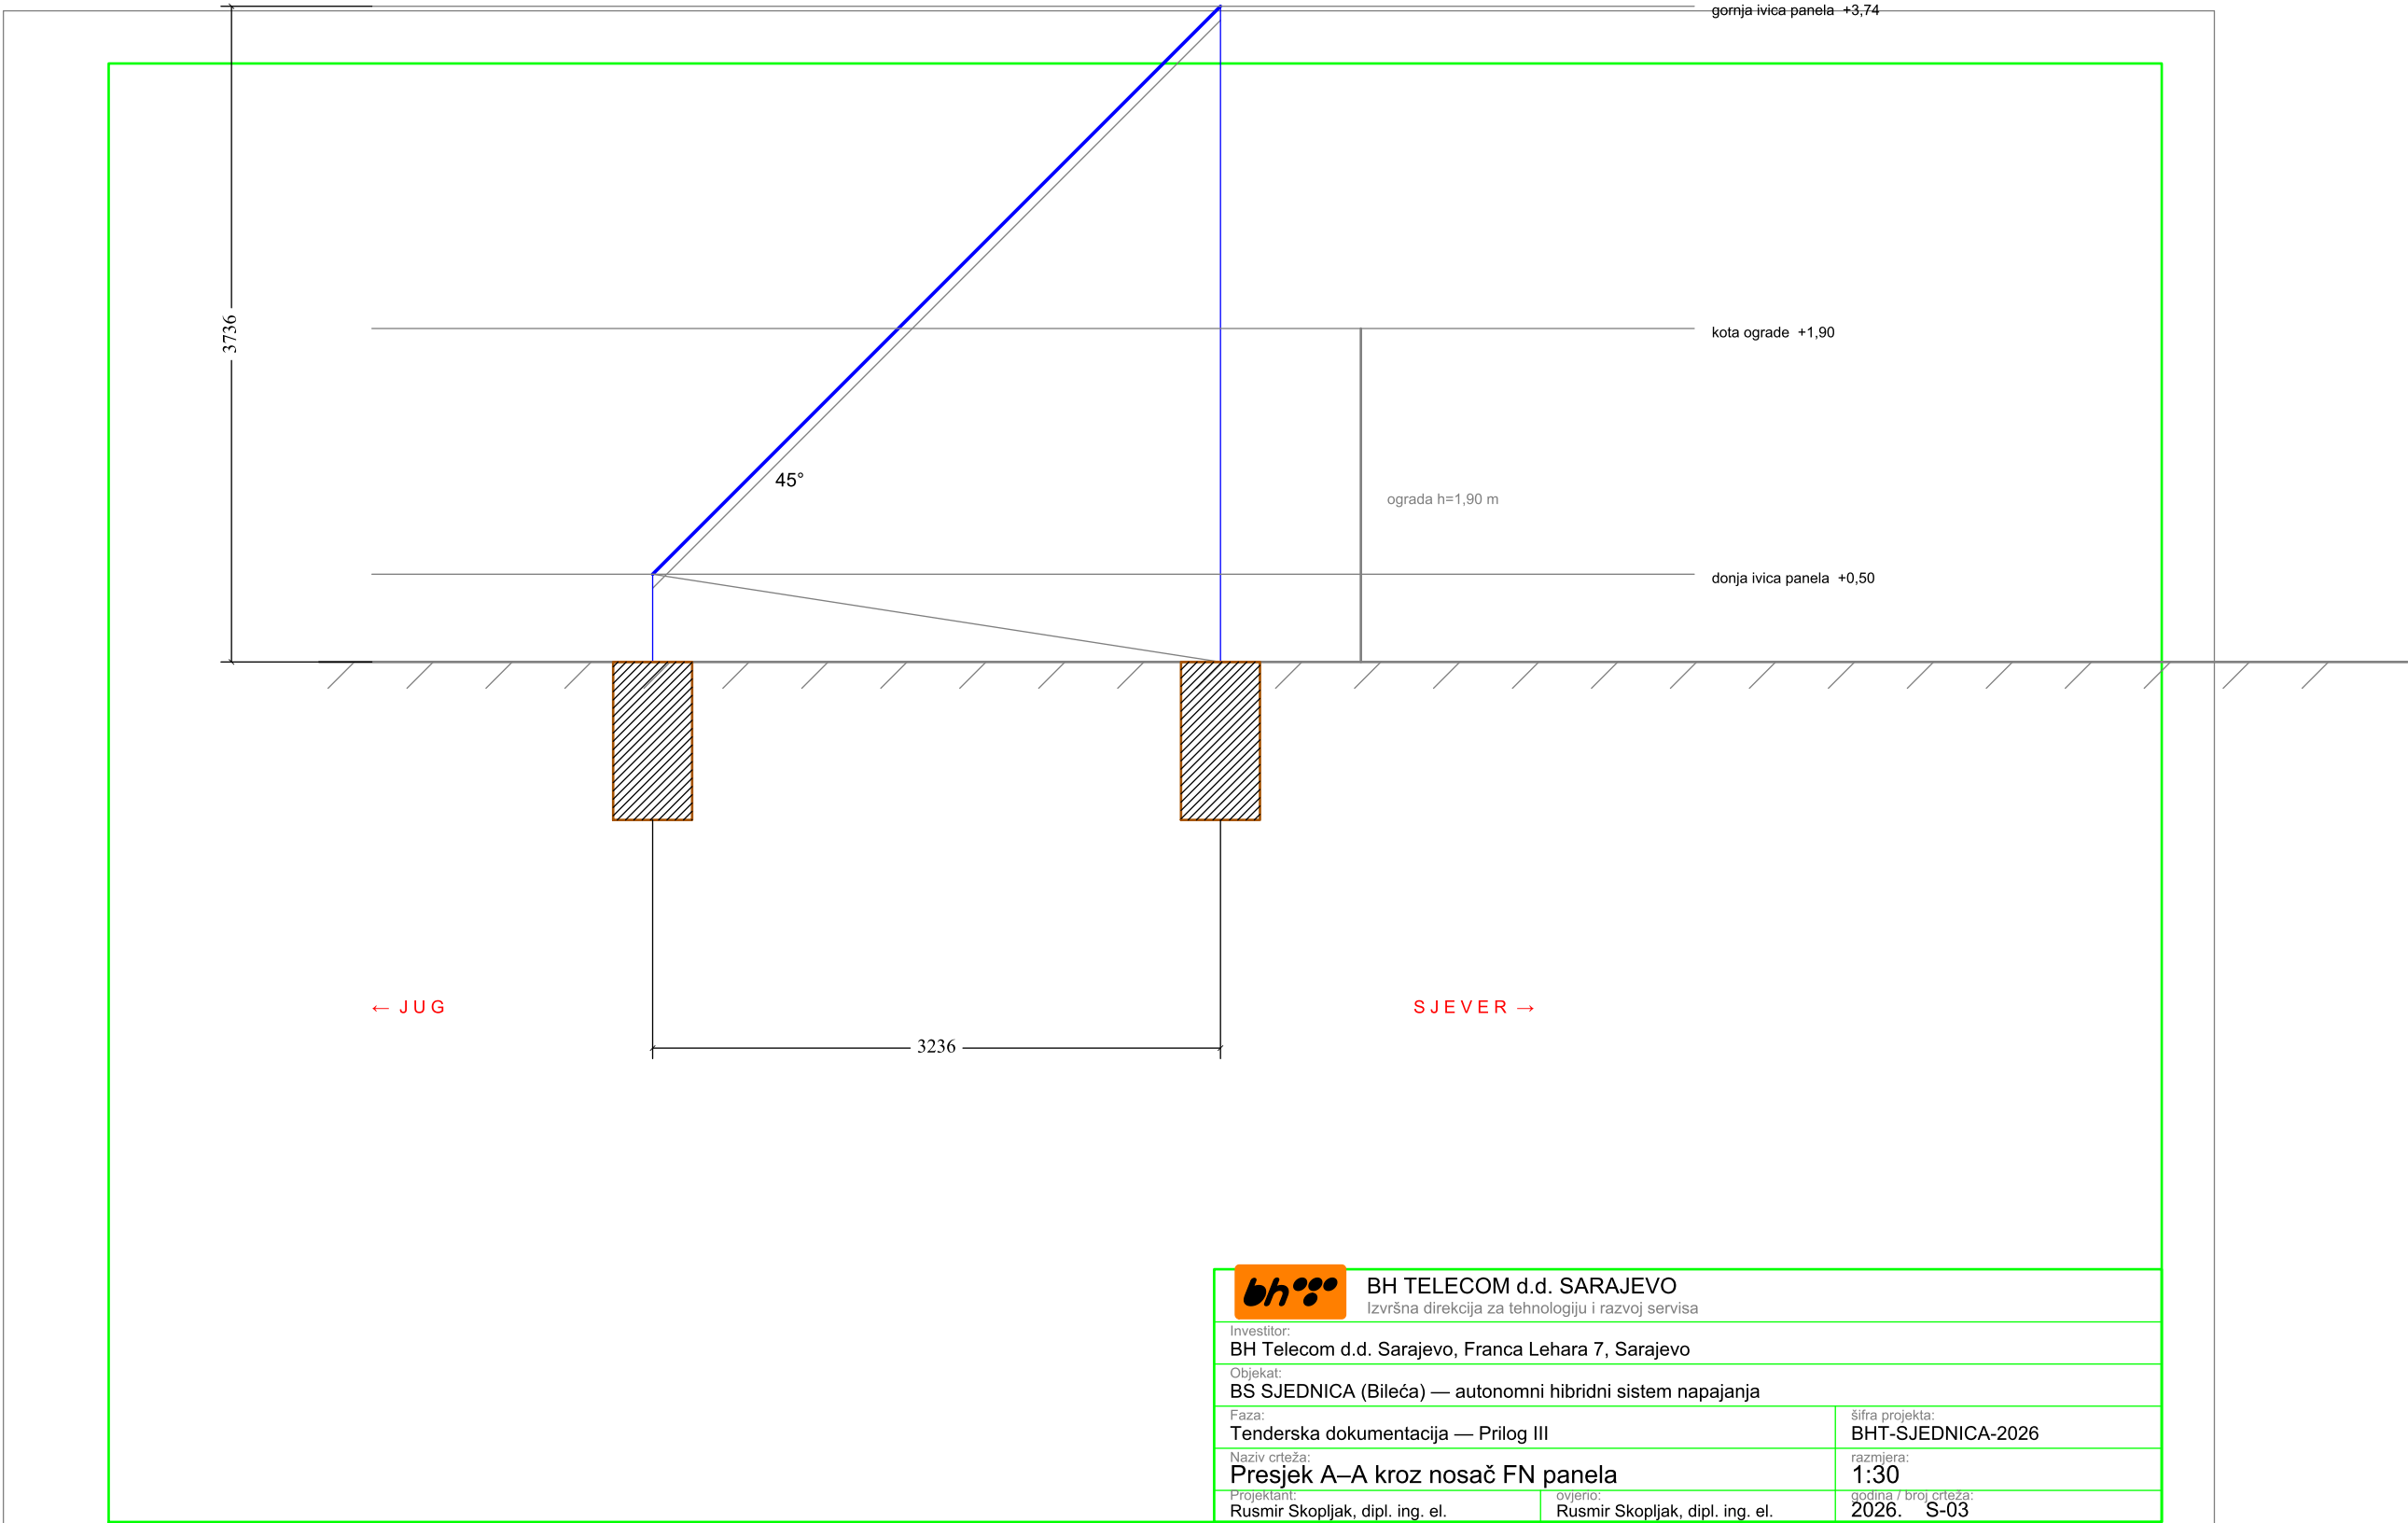

BH TELECOM d.d. SARAJEVO

Izvršna direkcija za tehnologiju i razvoj servisa

Investitor:

BH Telecom d.d. Sarajevo, Franca Lehara 7, Sarajevo

Objekat:

BS SJEDNICA (Bileća) — autonomni hibridni sistem napajanja

Faza:

Tenderska dokumentacija — Prilog III

Naziv crteža:

Presjek A–A kroz nosač FN panela

Projektant:

Rusmir Skopljak, dipl. ing. el.

ovjeren:

Rusmir Skopljak, dipl. ing. el.

šifra projekta:

BHT-SJEDNICA-2026

razmjera:

1:30

godina / broj crteža:

2026. S-03