

OSNOVA — kontejner je PRAZAN

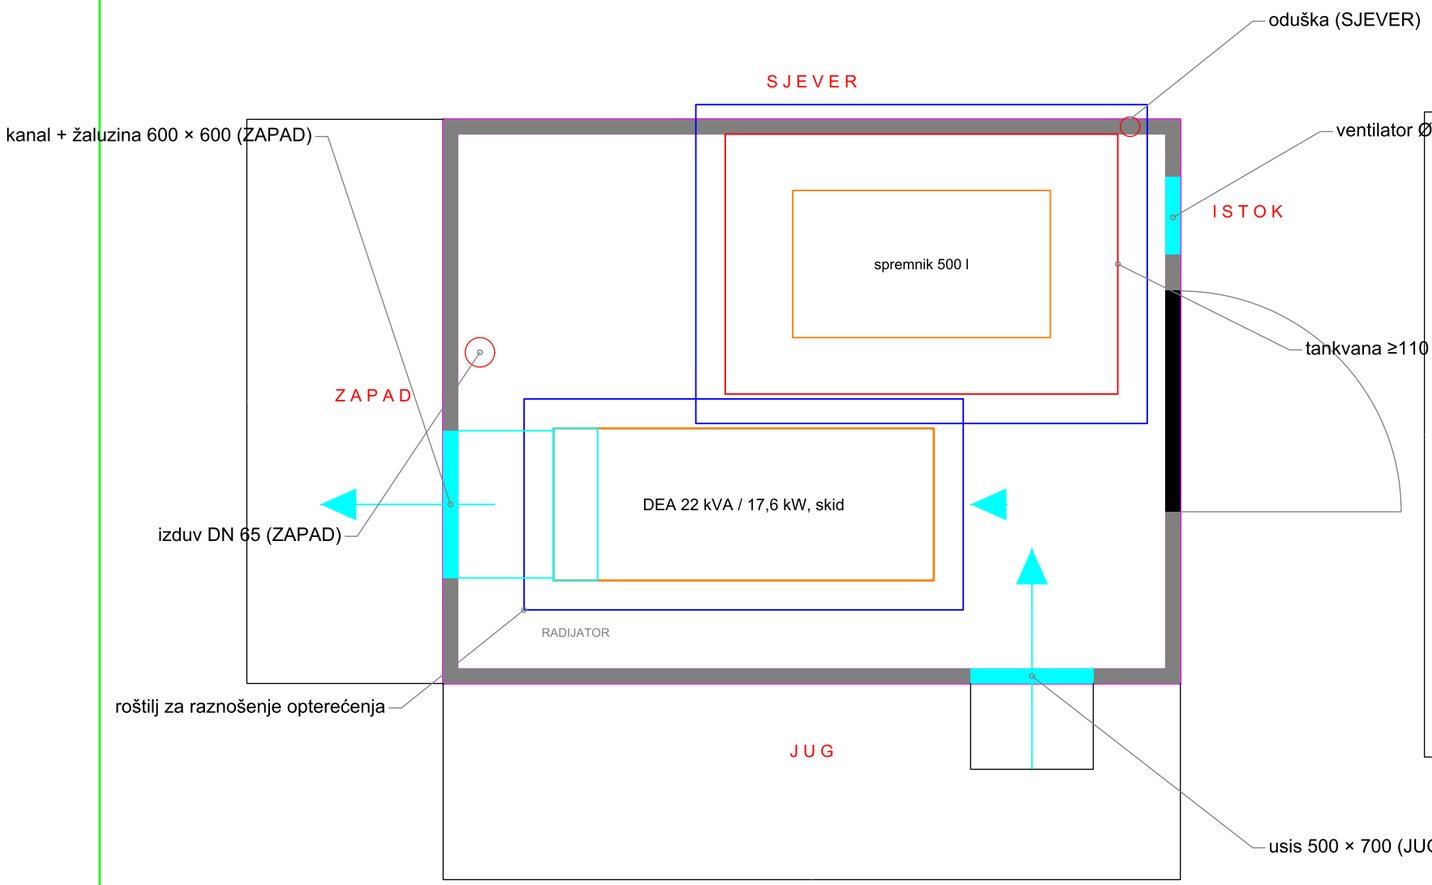

PRESJEK 1–1 (pogled prema SJEVERU — ZAPAD lijevo)

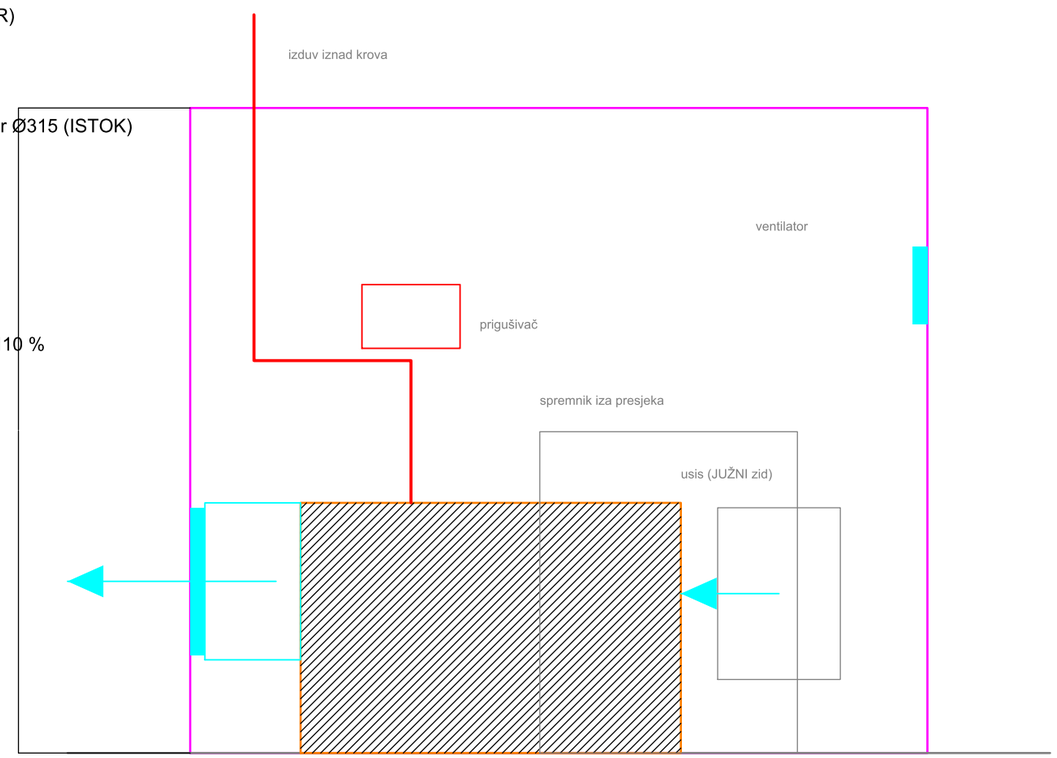

NAPOMENE:

1. FG Wilson P22-6 (Skid), TL 2019-08-14: hladnjak 1980 m³/h, sagorijevanje 90 m³/h, toplota u prostor 7,1 kW, maks. vanjski otpor 125 Pa.
2. Žaluzine zadovoljavaju: usis 500 × 700 (Δp≈16 Pa) + izlaz 600 × 600 (≈15 Pa) + kanal < 125 Pa.
3. Ventilator 1200 m³/h je DOPUNSKA ventilacija (min. 120 m³/h); protok hlađenja daje ventilator hladnjaka.
4. Izduv DN 65 usvojen (NO 50 zadovoljava protutlak, ali radi pri 33 m/s).
5. Pod je dimenzionisan na 10,00 kN/m² ravnomjerno raspodijeljeno (projekat lokacije, 4.4.2.3). Agregat 3,93 i pun spremnik 9,2 kN/m² su KONCENTRISANI — roštilj za raznošenje je OBAVEZAN.
6. RASPORED: usis JUG (+0,30), kanal/izlaz i izduv ZAPAD, oduška SJEVER, ventilator ISTOK; ≥3 m između usisa, izduva i oduške. Ništa ne izbacuje prema ormarima na SJEVERU.
7. UNOS: skid 620 mm kroz vrata 900 mm. Kontejner je PRAZAN.

BH TELECOM d.d. SARAJEVO
Izvršna direkcija za tehnologiju i razvoj servisa

Investitor: BH Telecom d.d. Sarajevo, Franca Lehara 7, Sarajevo		
Objekat: BS SJEDNICA (Bileća) — autonomni hibridni sistem napajanja		
Faza: Tenderska dokumentacija — Prilog III		šifra projekta: BHT-SJEDNICA-2026
Naziv crteža: DEA u postojećem kontejneru — osnova i presjek		razmjera: 1:25
Projektant: Rusmir Skopljak, dipl. ing. el.	ovjerio: Rusmir Skopljak, dipl. ing. el.	godina / broj crteža: 2026. M-01