



Dioničko društvo BH Telecom Sarajevo  
Franca Lehara 7, 71000 Sarajevo, BiH  
Izvršna direkcija za tehnologiju i razvoj servisa  
tel: +387 33 256 500; fax: +387 33 256 505

## BH TELECOM d.d. SARAJEVO

Izvršna direkcija za tehnologiju i razvoj servisa

### TENDERSKA DOKUMENTACIJA ZA NABAVKU

#### INFRASTRUKTURA I INSTALACIJA OPREME ZA AUTONOMNI HIBRIDNI SISTEM NAPAJANJA SJEDNICA, BILEĆA (LOT 1 i 2)

PROVOĐENJEM NABAVKE PUTEM PREGOVARAČKOG POSTUPKA NABAVKE SA OBJAVOM  
OBAVJEŠTENJA

### PRILOG III

SITUACIJA, DISPOZICIJA OPREME I GRAFIČKI PRILOZI (NACRTI)

Lokacija: BS Sjednica, Bileća, BiH

Koordinate: 42,9448° N · 18,3236° E · 1076 m n.v.

Sarajevo, august 2026. godine





BH TELECOM d.d. SARAJEVO | BS SJEDNICA (BILEĆA) | PRILOG III

Fotografija postojećeg stanja lokacije

Antenski stub, kontejner, ograda — stanje prije izvođenja radova


Crtež br.  
INFO-01




# 1. OPŠTI PODACI O LOKACIJI

|                     |   |
|---------------------|---|
| Investitor          | BH Telecom d.d. Sarajevo, Franca Lehara 7, 71000 Sarajevo                                                              |
| Objekat             | Bazna stanica SJEDNICA                                                                                                 |
| Općina / Entitet    | Bileća / Republika Srpska                                                                                              |
| Koordinate          | 42.9448° N, 18.3236° E                                                                                                 |
| Nadmorska visina    | 1076 m   |
| Zakupljena površina | 150 m²   |
| Betonski temelj     | 5,40 × 5,40 m, sa metalnom ogradom visine 1,90 m                                                                       |
| Antenski stub       | Rešetkasta izvedba, visina 38 m; baza 4,20 m (dno) / 1,20 m (vrh)                                                      |
| Kontejner           | Vanjske dimenzije 3,005 × 2,30 m, zidni paneli 60 mm (unutra 6,29 m2), IP55, prema ovjerenom projektu lokacije; PRAZAN |
| Priključak na EES   | NE — lokacija nije priključena na elektroenergetsku mrežu                                                              |
| TK oprema           | Huawei RRU (3 kom) + BBU/MPLS, -48 VDC                                                                                 |
| Snaga potrošača     | 1.180 W nazivno / 1.330 W maksimalno (sa hlađenjem)                                                                    |
| Sistem napajanja    | Hibridni: FN moduli (primarni) + LFP baterije + DEA (rezervni)                                                         |
| FN konfiguracija    | 12 × 585 Wp (7,02 kWp), fiksni nagib 45°, bifacijalni                                                                  |
| DEA                 | 22 kVA / 17,6 kW stand-by (ISO 8528-3), skid izvedba u kontejneru                                                      |
| Spremnik goriva     | Dvoplašni, 500 l , sa nivo sondom i detekcijom curenja                                                                 |
| Maks. rad DEA       | 250 h/god (standby režim prema ISO 8528)                                                                               |

Napomena: podaci preuzeti iz RFI dokumenta „Autonomno napajanje za BS“ od 27.04.2026. godine i Projektnog zadatka za hibridno napajanje BS Sjednica. Konstruktivni podaci kontejnera preuzeti iz Projektnog zadatka za tipsku prenosivu kućicu — kontejner (opterećenje poda 10,00 kN/m², snijeg 3,00 kN/m², vjetar 1,10 kN/m²). DEA kao FG Wilson P22-6 (motor Perkins 404D-22G1, EU Stage IIIA) ili ekvivalent.

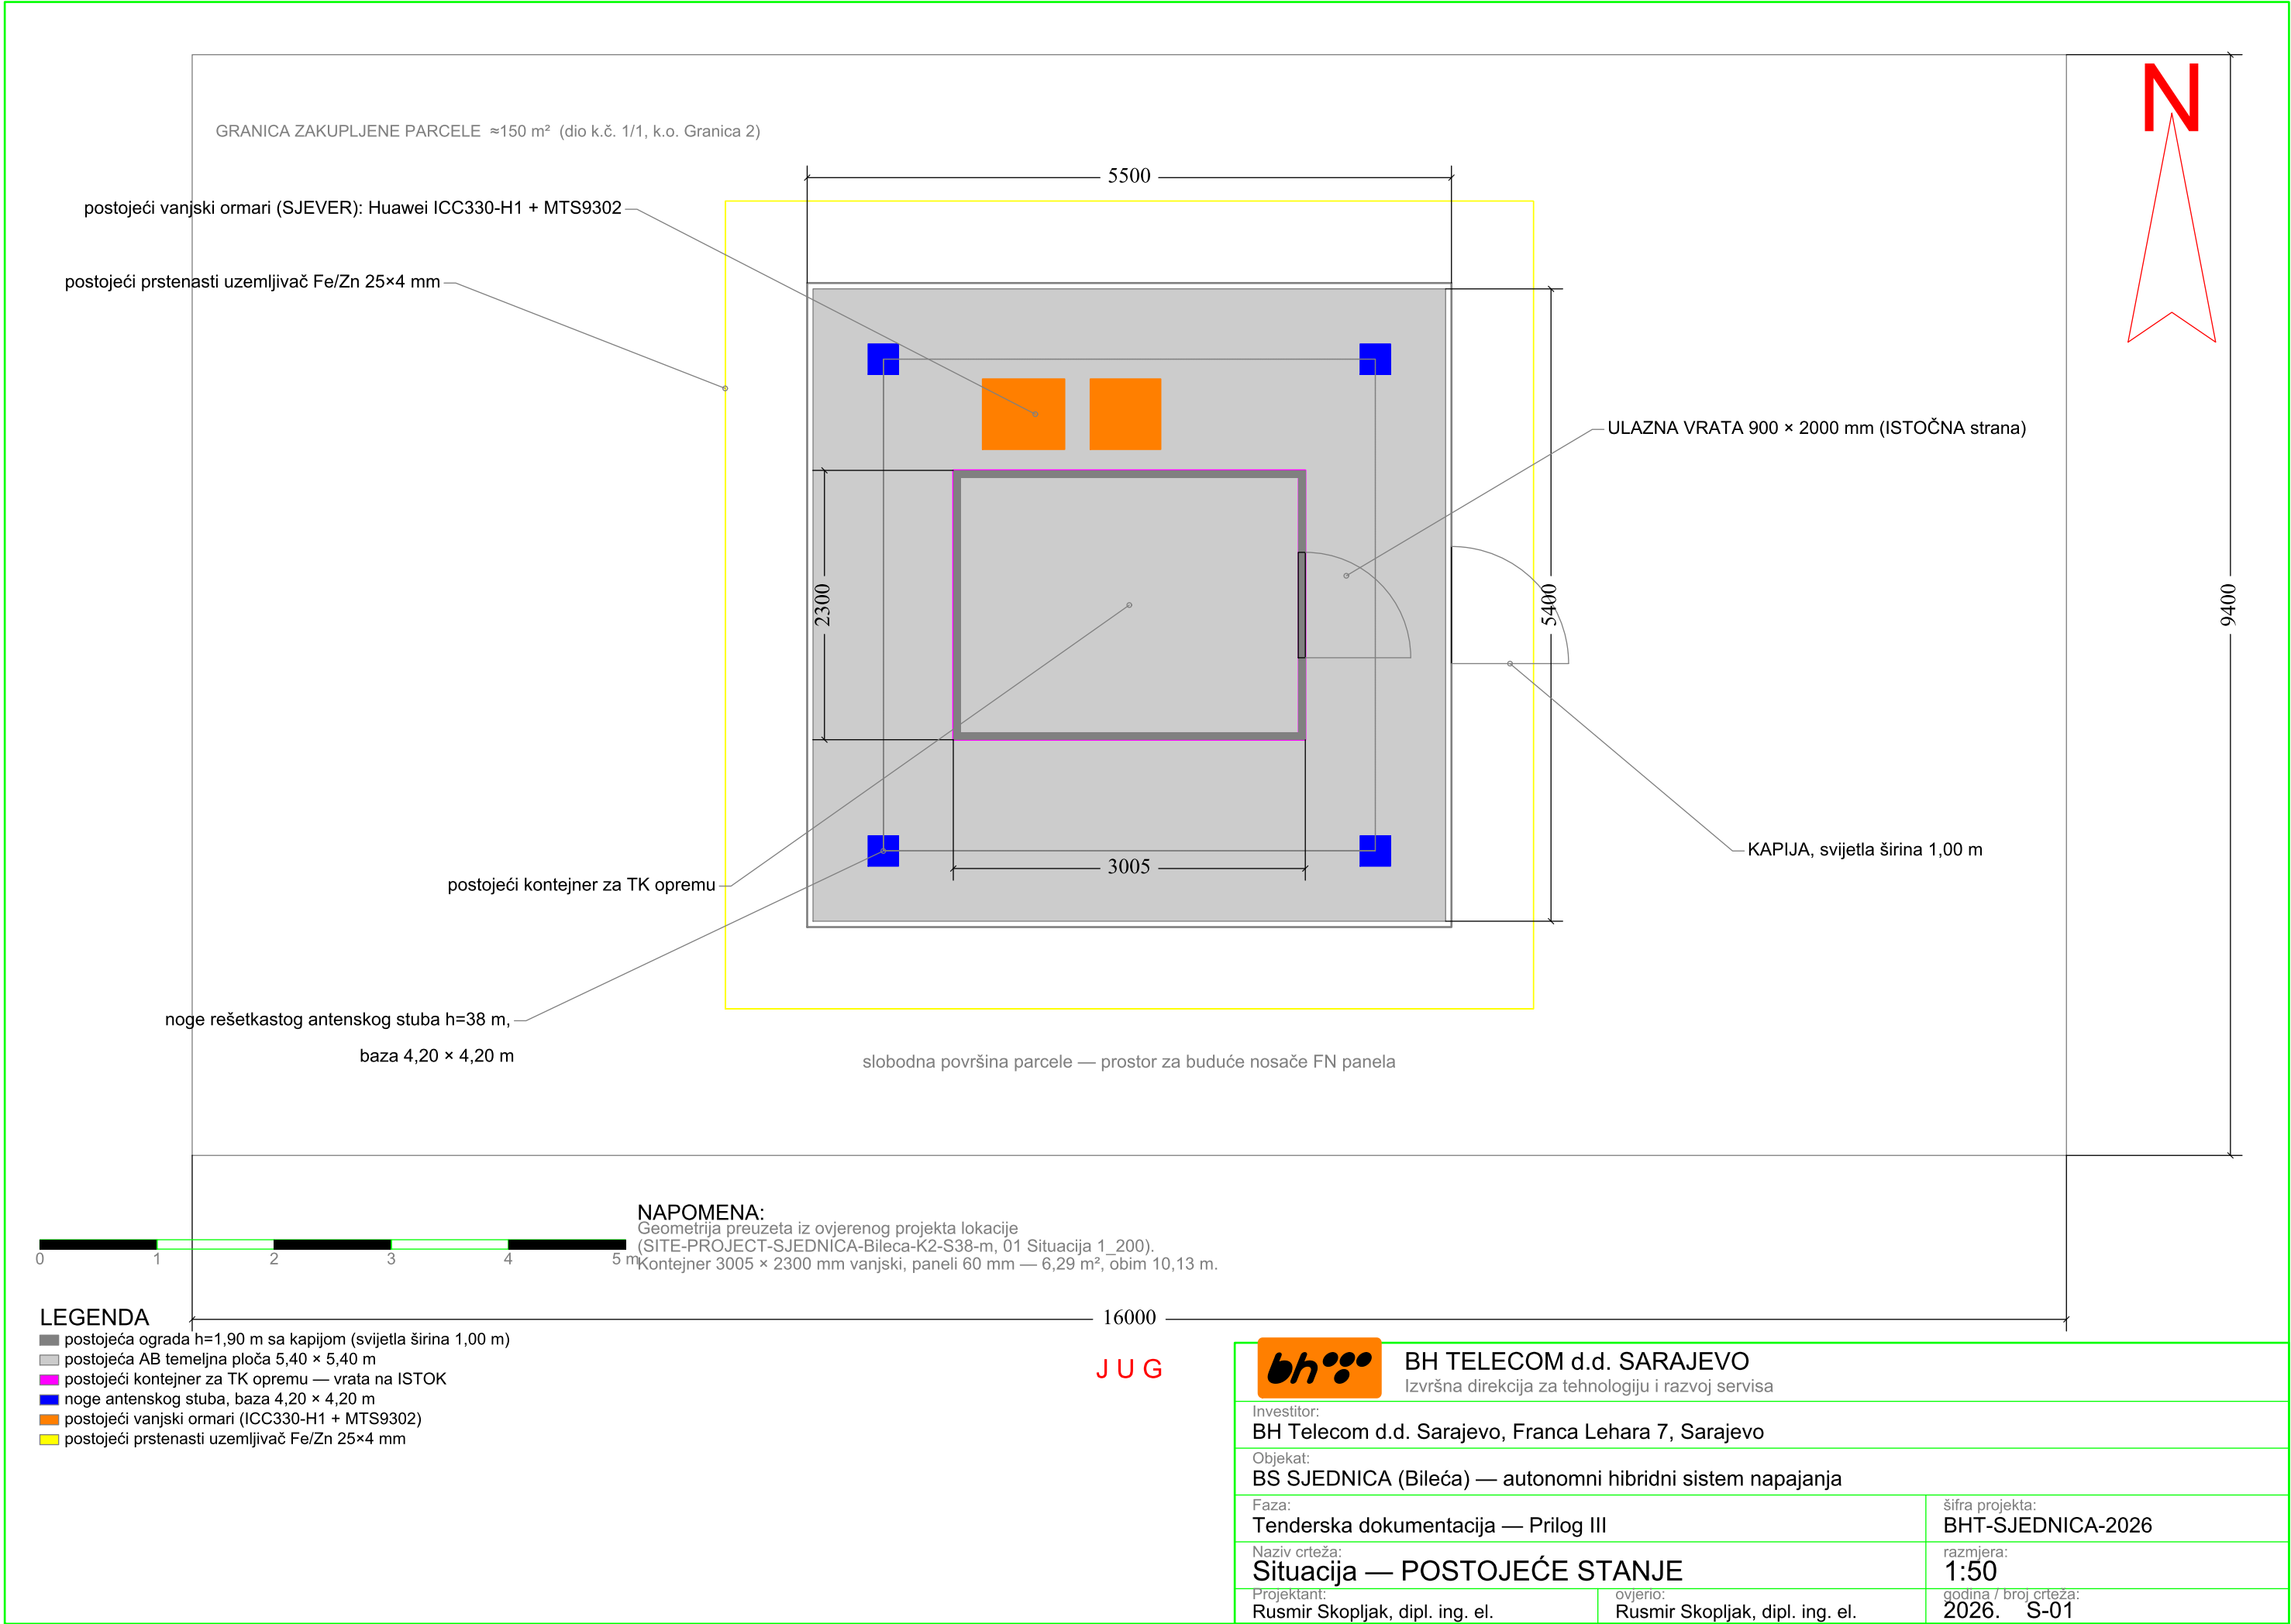

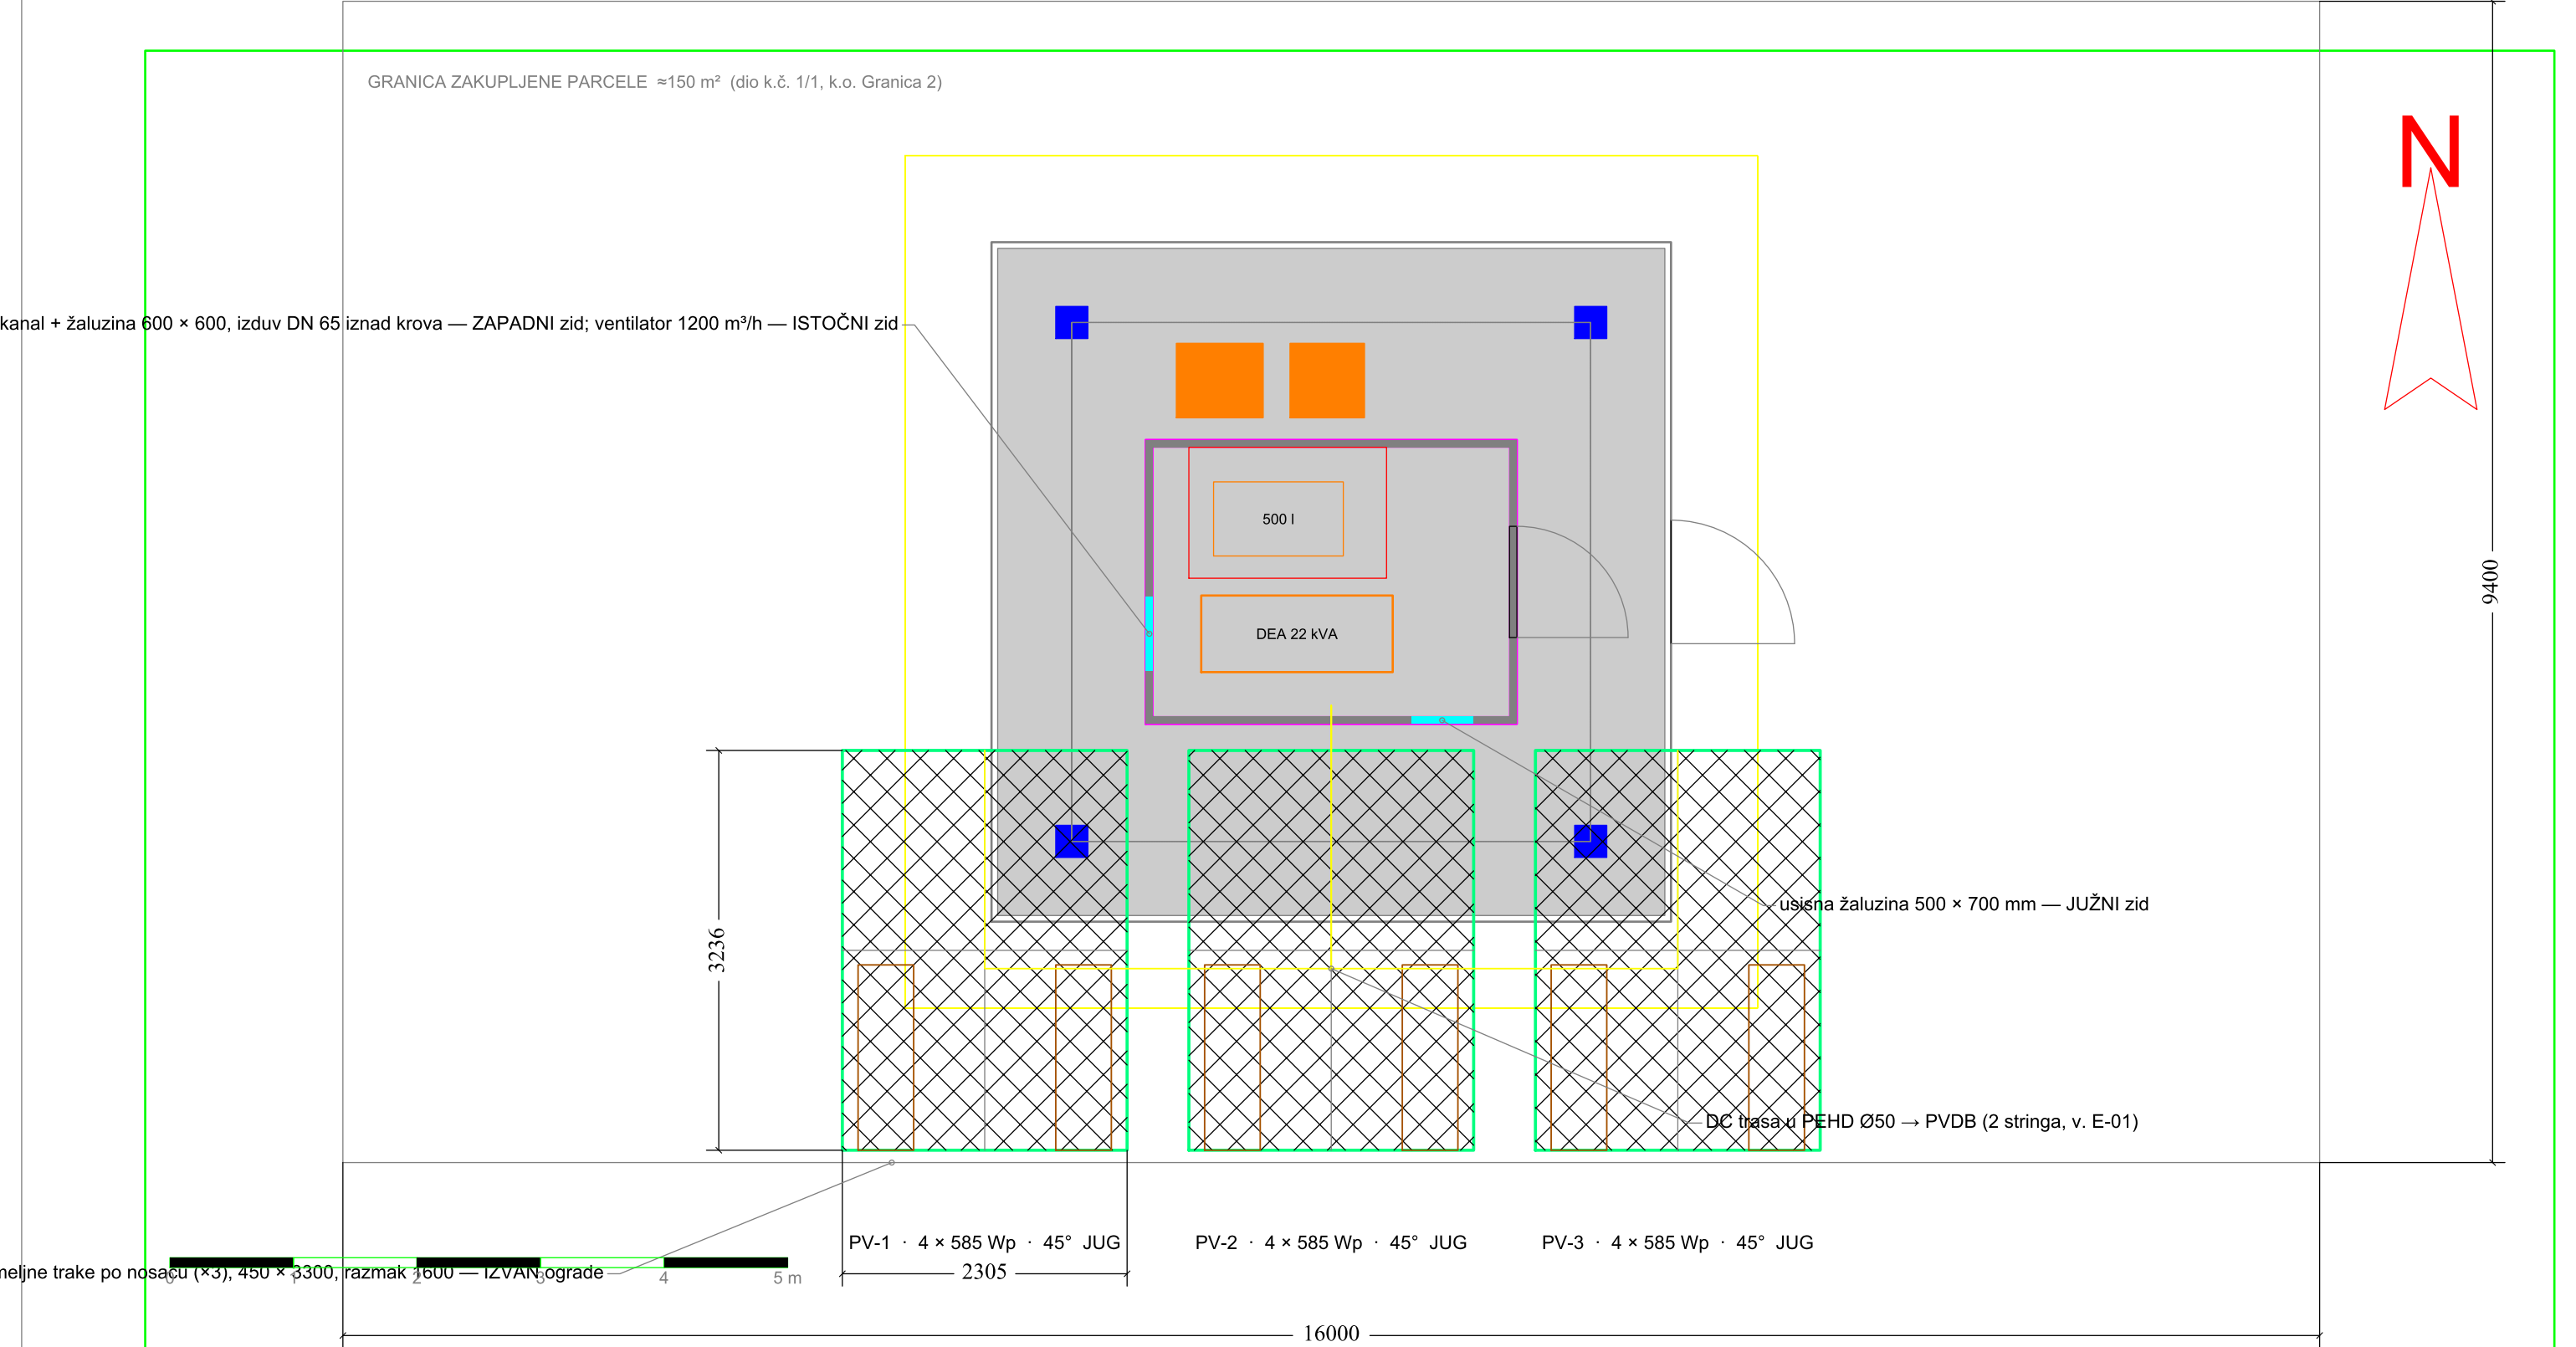

LEGENDA

- LOT 1 — nosači FN panela PV-1..PV-3 (po 4 × 585 Wp, 45°, JUG) — 2 stringa × 6
- LOT 1 — AB temeljne trake 450 × 3300 mm, razmak 1600 mm
- LOT 1 — DC trasa u PEHD Ø50 do PVDB
- LOT 2 — DEA 22 kVA u skid izvedbi i spremnik 500 l
- LOT 2 — usisna žaluzina (JUG); kanal, žaluzina i izduv (ZAPAD); ventilator (ISTOK)

NAPOMENA — PRORAČUNSKO OPTEREĆENJE:

Vjetar  $q_p \geq 1,20 \text{ kN/m}^2$  (udar 3 s  $\approx 45 \text{ m/s}$ ) — iznad kapaciteta kataloškog nosača tipa A, stoga CUSTOM IZRADA: sail 10,55 m²/nosaču, ULS uzgon 18,1 kN, moment prevrtanja 62,8 kNm; ovjerava ponuđač (Prilog II, 1.3).  
Temelji IZVAN ograde (400 mm od kote ograde); gornja ivica panela +4,23 m, 2836 mm iznad ograde. Kontejner je PRAZAN.



BH TELECOM d.d. SARAJEVO

Izvršna direkcija za tehnologiju i razvoj servisa

Investitor:

BH Telecom d.d. Sarajevo, Franca Lehara 7, Sarajevo

Objekat:

BS SJEDNICA (Bileća) — autonomni hibridni sistem napajanja

Faza:

Tenderska dokumentacija — Prilog III

Naziv crteža:

Situacija — BUDUĆE STANJE (LOT 1 + LOT 2)

Projektant:

Rusmir Skopljak, dipl. ing. el.

ovjerio:

Rusmir Skopljak, dipl. ing. el.

šifra projekta:


BHT-SJEDNICA-2026

razmjera:

1:50

godina / broj crteža:

2026. S-02

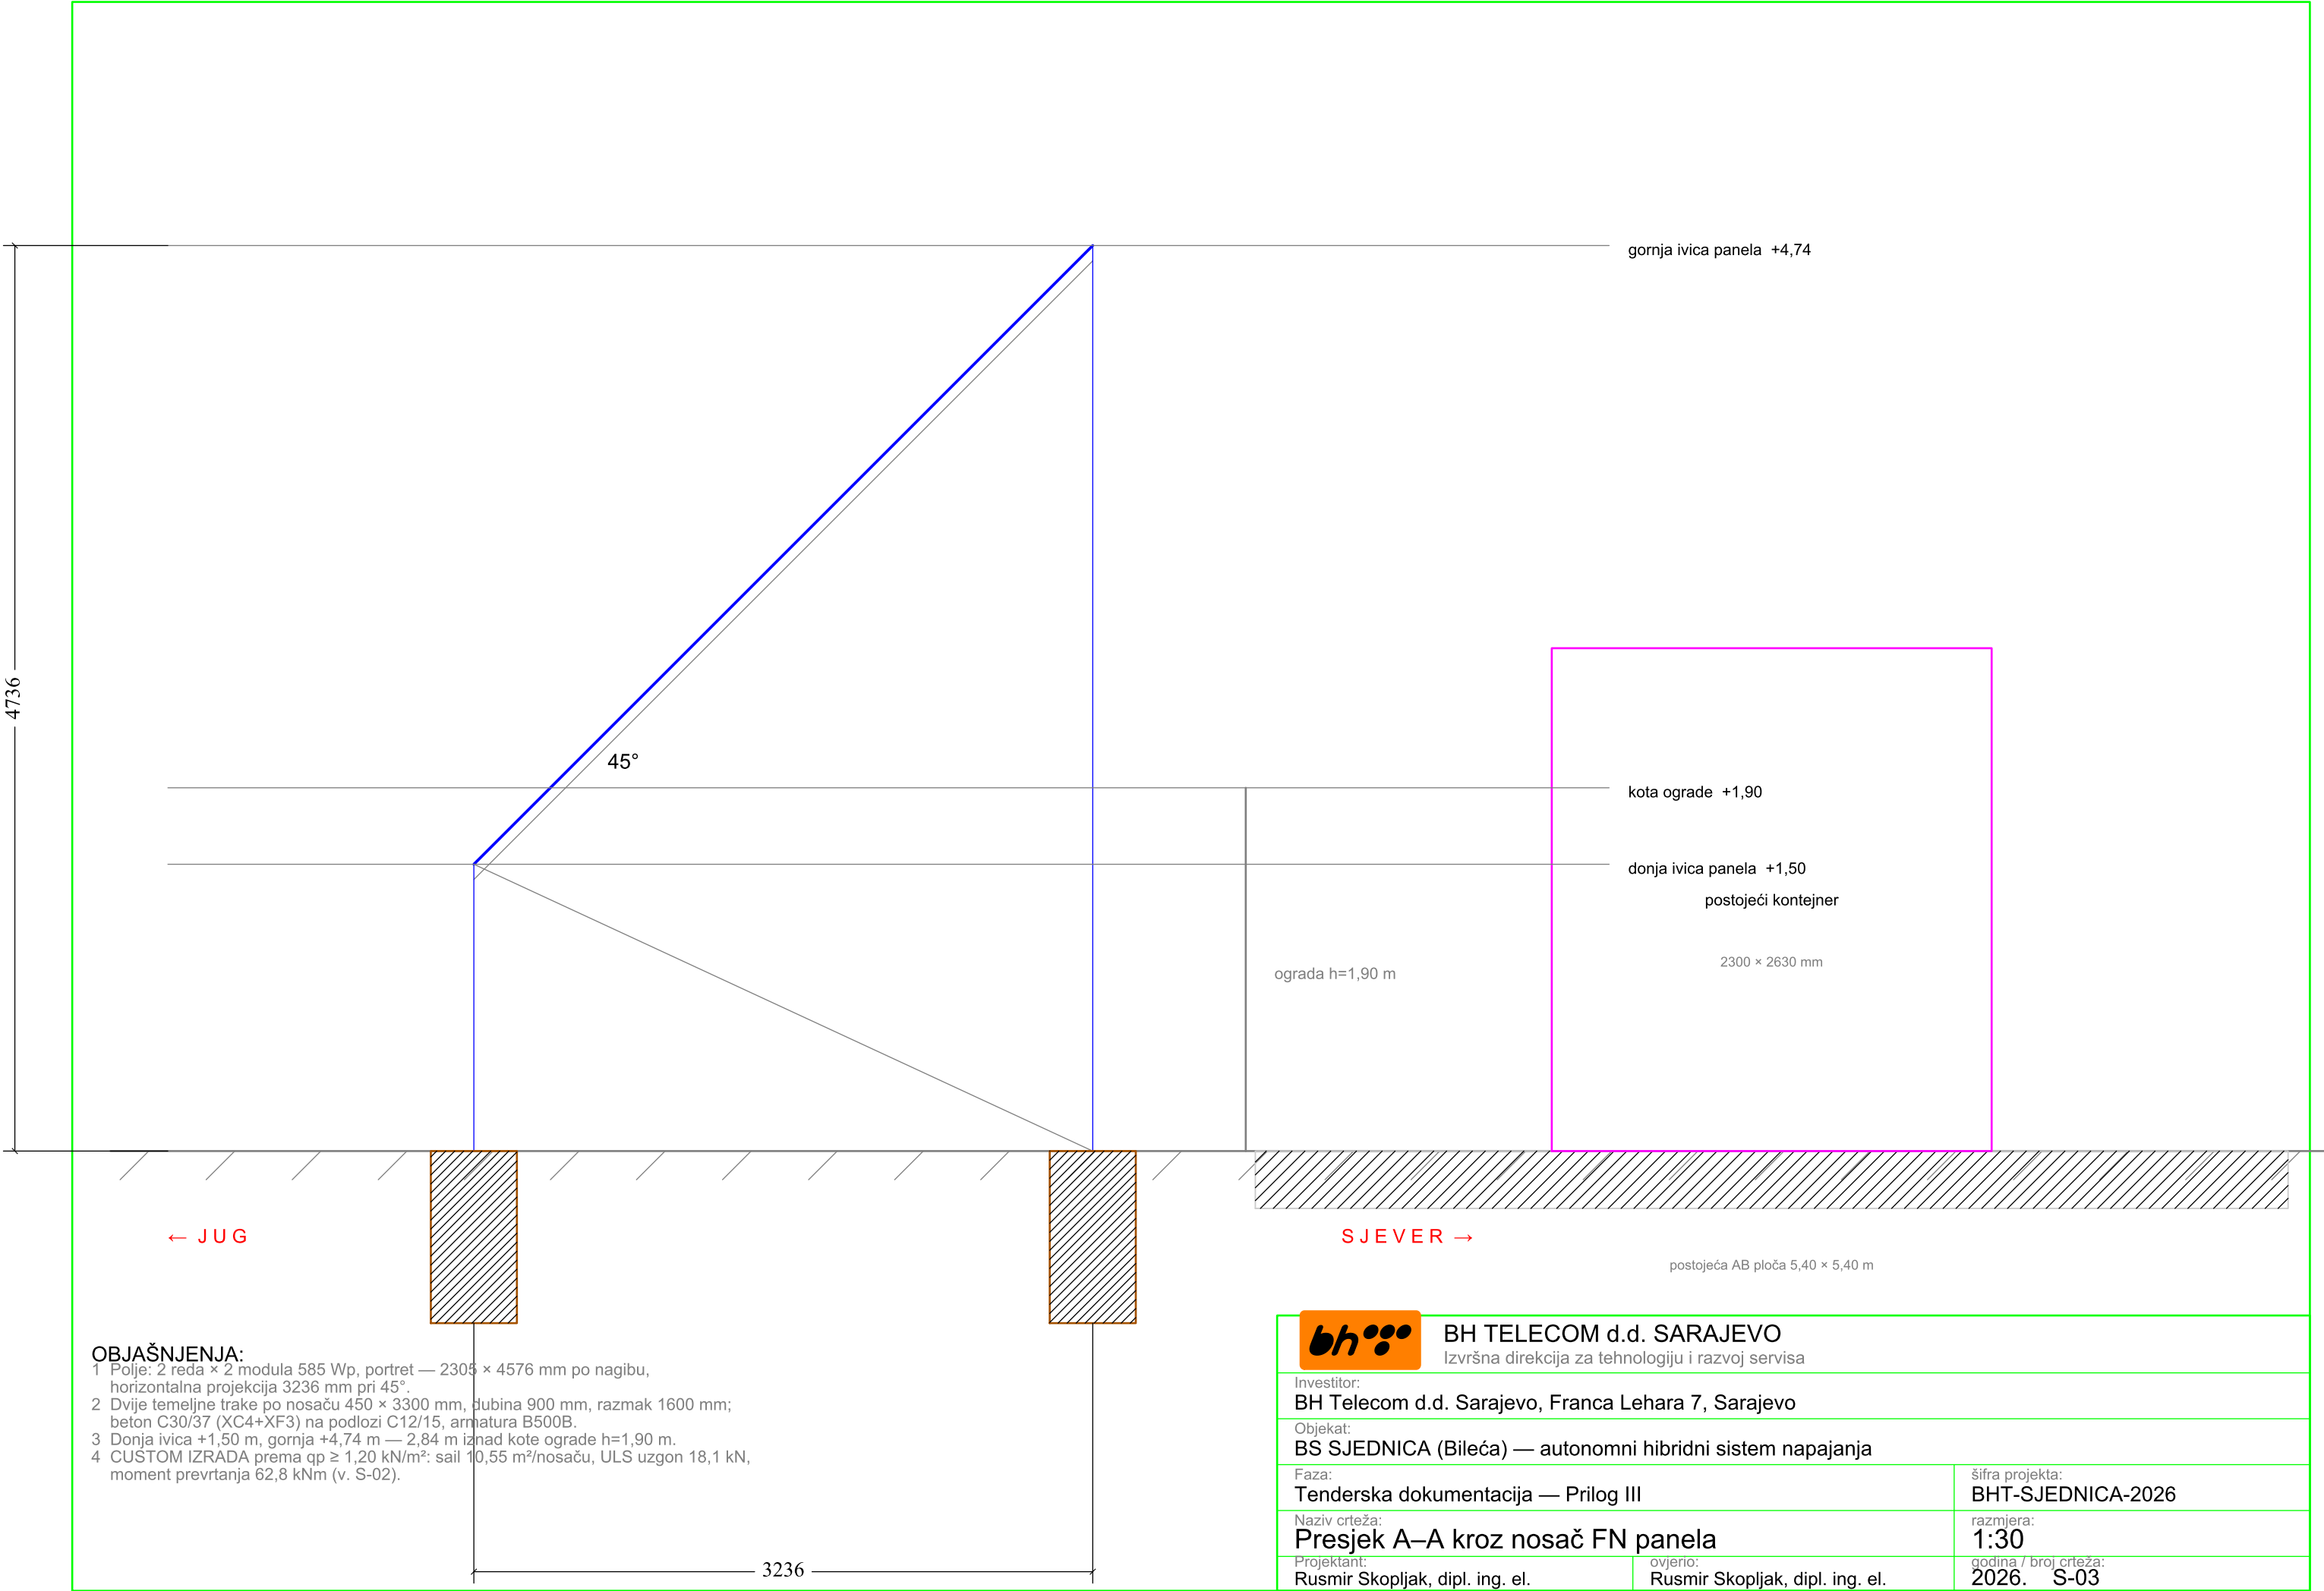

OBJAŠNJENJA:

- Polje: 2 reda x 2 modula 585 Wp, portret — 2303 x 4576 mm po nagibu, horizontalna projekcija 3236 mm pri 45°.
- Dvije temeljne trake po nosaču 450 x 3300 mm, dubina 900 mm, razmak 1600 mm; beton C30/37 (XC4+XF3) na podlozi C12/15, armatura B500B.
- Donja ivica +1,50 m, gornja +4,74 m — 2,84 m iznad kote ograde h=1,90 m.
- CUSTOM IZRADA prema qp ≥ 1,20 kN/m²: sail 10,55 m²/nosaču, ULS uzgon 18,1 kN, moment prevrtanja 62,8 kNm (v. S-02).



BH TELECOM d.d. SARAJEVO

Izvršna direkcija za tehnologiju i razvoj servisa

Investitor:

BH Telecom d.d. Sarajevo, Franca Lehara 7, Sarajevo

Objekat:

BS SJEDNICA (Bileća) — autonomni hibridni sistem napajanja

Faza:

Tenderska dokumentacija — Prilog III

Naziv crteža:

Presjek A–A kroz nosač FN panela

Projektant:

Rusmir Skopljak, dipl. ing. el.

ovjerio:

Rusmir Skopljak, dipl. ing. el.

šifra projekta:

BHT-SJEDNICA-2026

razmjera:

1:30


godina / broj crteža:

2026. S-03









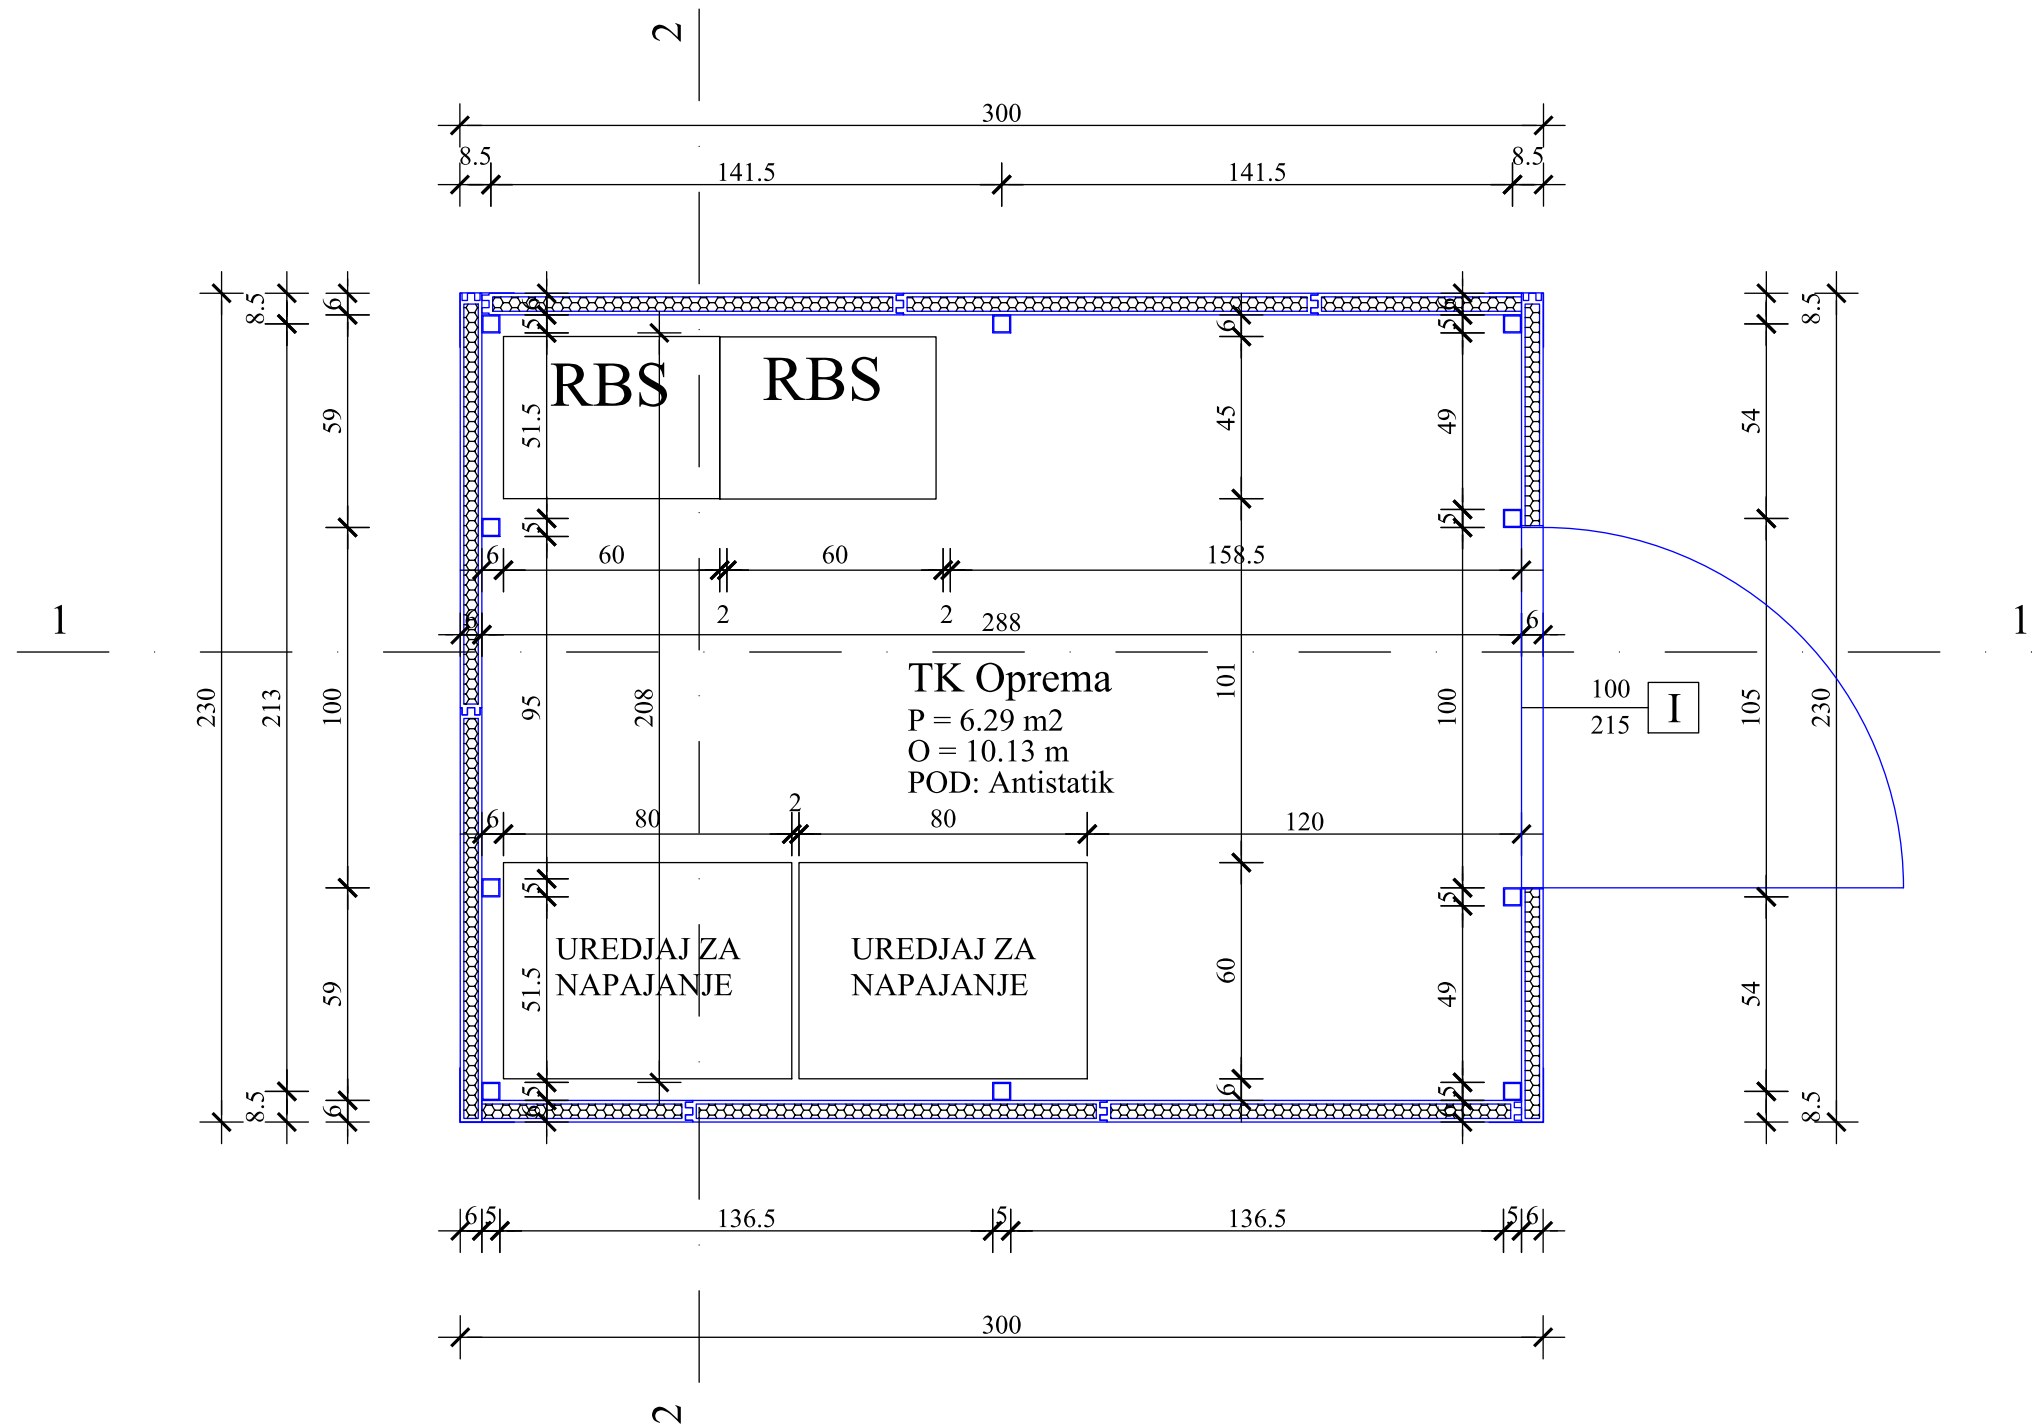





|                                                 |            |                                                          |                                 |   |                                                    |
|-------------------------------------------------|------------|----------------------------------------------------------|---------------------------------|---|----------------------------------------------------|
| Investitor: BH TELECOM d.d.                     |            | Objekat: Infrastruktura bazne stanice mobilne telefonije |                                 | <br>Dioničko društvo Sarajevo |                                                    |
| Glavni projekat<br>Knjiga 1/1                   | Faza:<br>A | godina:<br>2018.                                         | šifra projekta: GP-BS-10472-326 |   |                                                    |
| Naziv crteža: Osnova objekta za smještaj opreme |            |                                                          | razmjera:<br>1:50               | broj crteža:<br>1 - (148/177)                                                                                      | ovjerio:<br>Projektant: Dženadin Mušinović, d.i.g. |

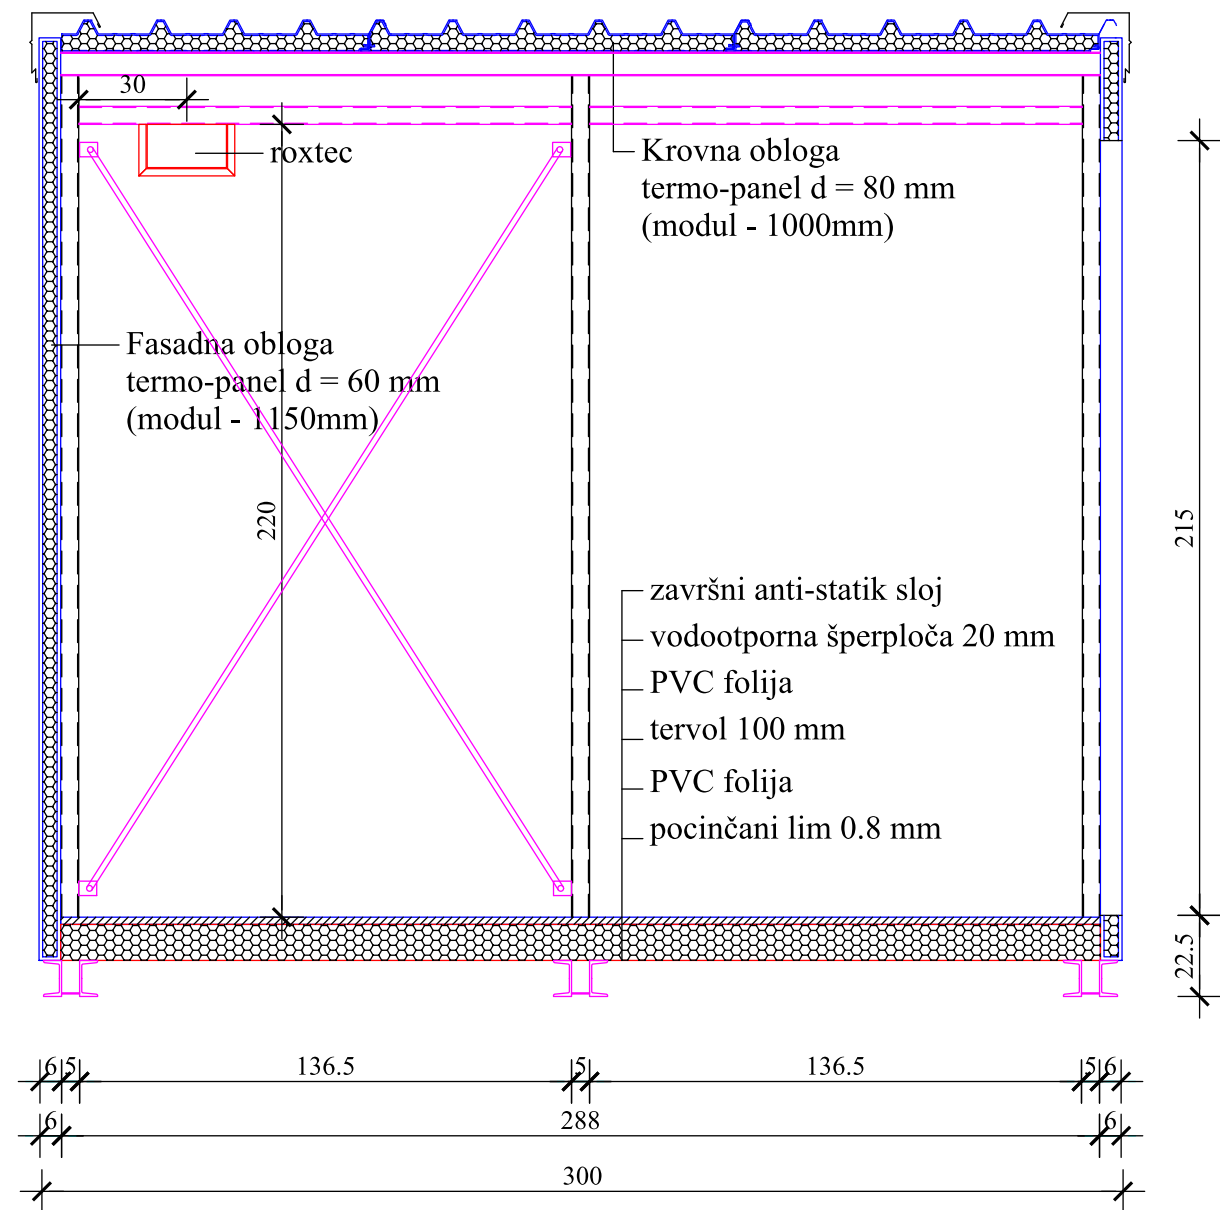

|                                                      |            |                                                          |                                 |   |  |
|------------------------------------------------------|------------|----------------------------------------------------------|---------------------------------|---|--|
| Investitor: BH TELECOM d.d.                          |            | Objekat: Infrastruktura bazne stanice mobilne telefonije |                                 | <br>Dioničko društvo Sarajevo                       |  |
| Glavni projekat<br>Knjiga 1/1                        | Faza:<br>A | godina:<br>2018.                                         | šifra projekta: GP-BS-10472-326 |   |  |
| Naziv crteža: Presjek 1-1 objekta za smještaj opreme |            | razmjera:<br>1:50                                        | broj crteža:<br>2 - (149/177)   | ovjerio: <br>Projektant: Dženadin Mušinović, d.i.g. |  |

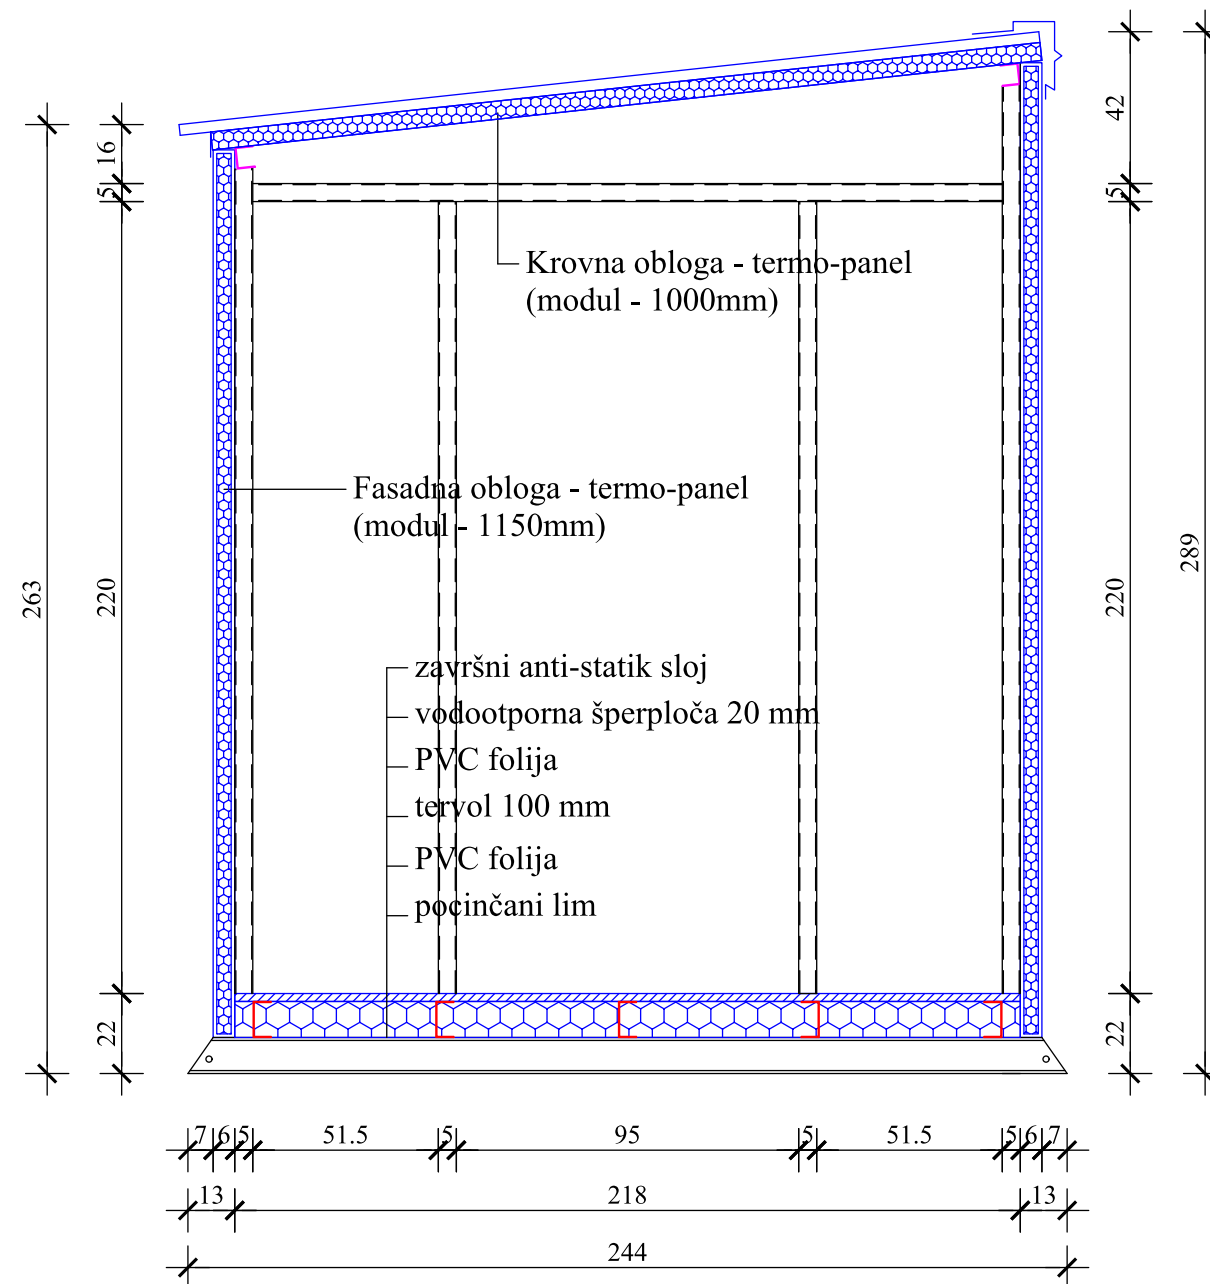


|                                                      |            |                                                          |                                 |   |                                                  |
|------------------------------------------------------|------------|----------------------------------------------------------|---------------------------------|---|--------------------------------------------------|
| Investitor: BH TELECOM d.d.                          |            | Objekat: Infrastruktura bazne stanice mobilne telefonije |                                 | <br>Dioničko društvo Sarajevo |                                                  |
| Glavni projekat<br>Knjiga 1/1                        | Faza:<br>A | godina:<br>2018.                                         | šifra projekta: GP-BS-10472-326 |   |                                                  |
| Naziv crteža: Presjek 2-2 objekta za smještaj opreme |            |                                                          | razmjera:<br>1:50               | broj crteža:<br>3 - (150/177)                                                                                      | ovjerio:<br>Projektant:Dženadin Mušinović,d.i.g. |

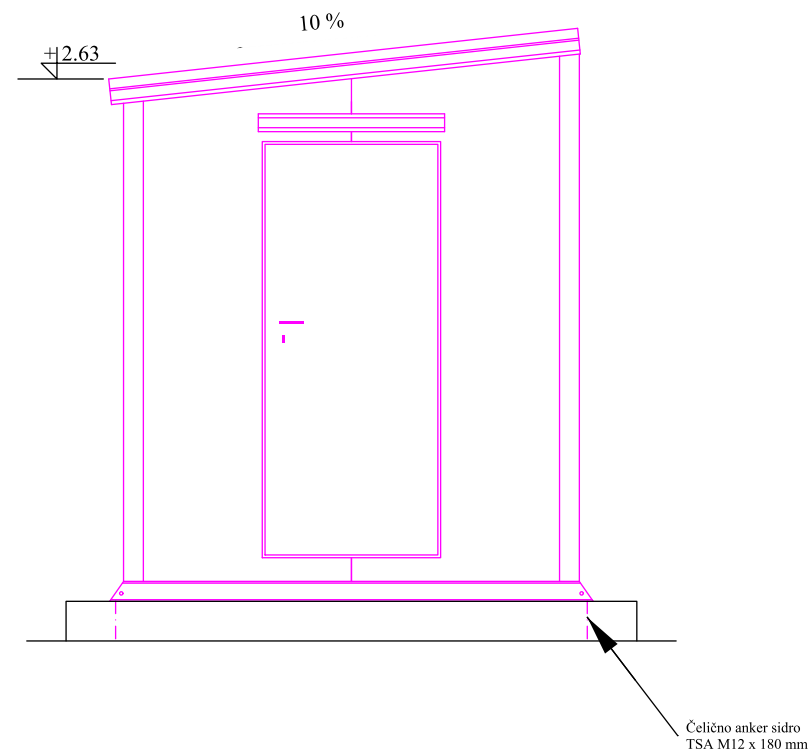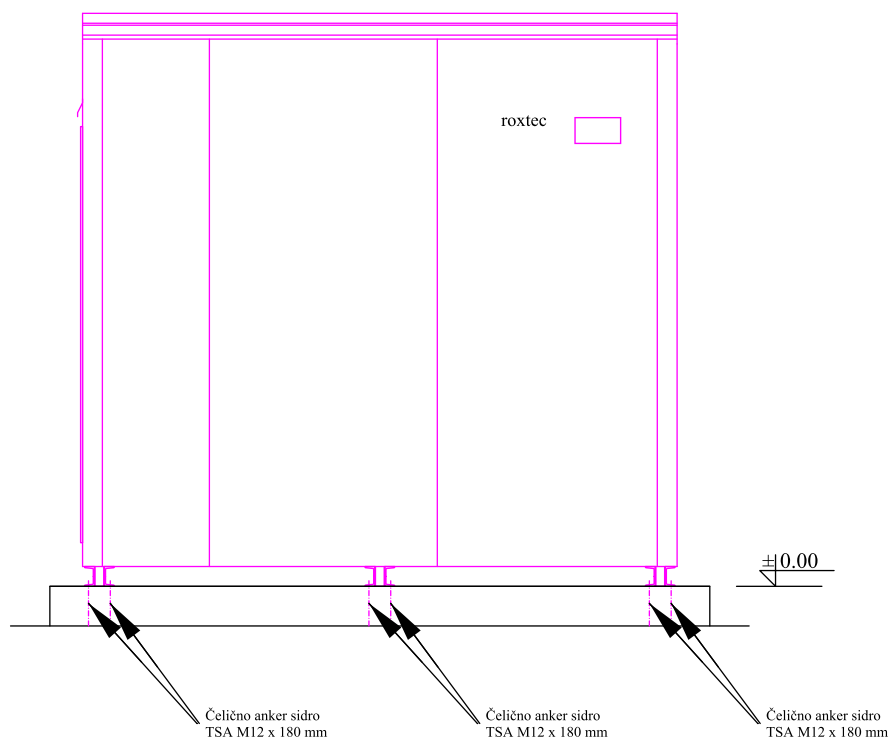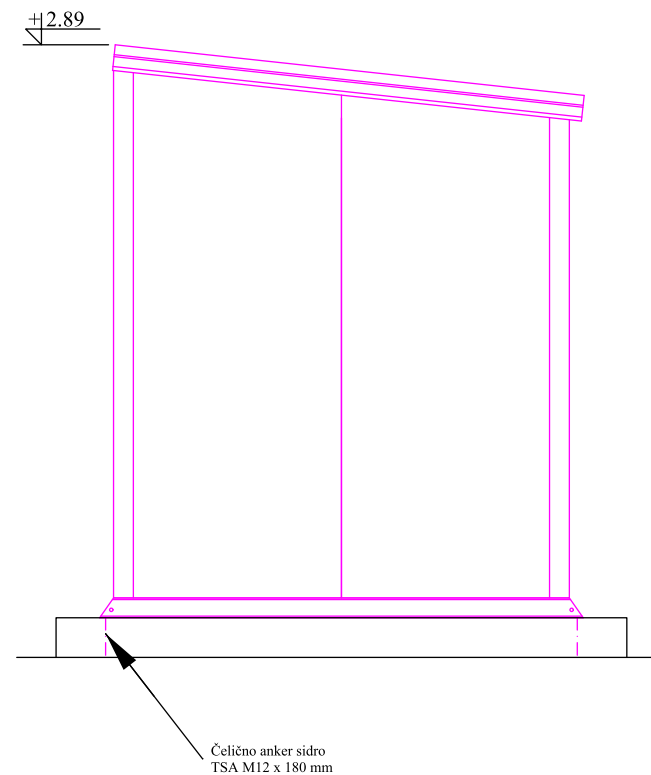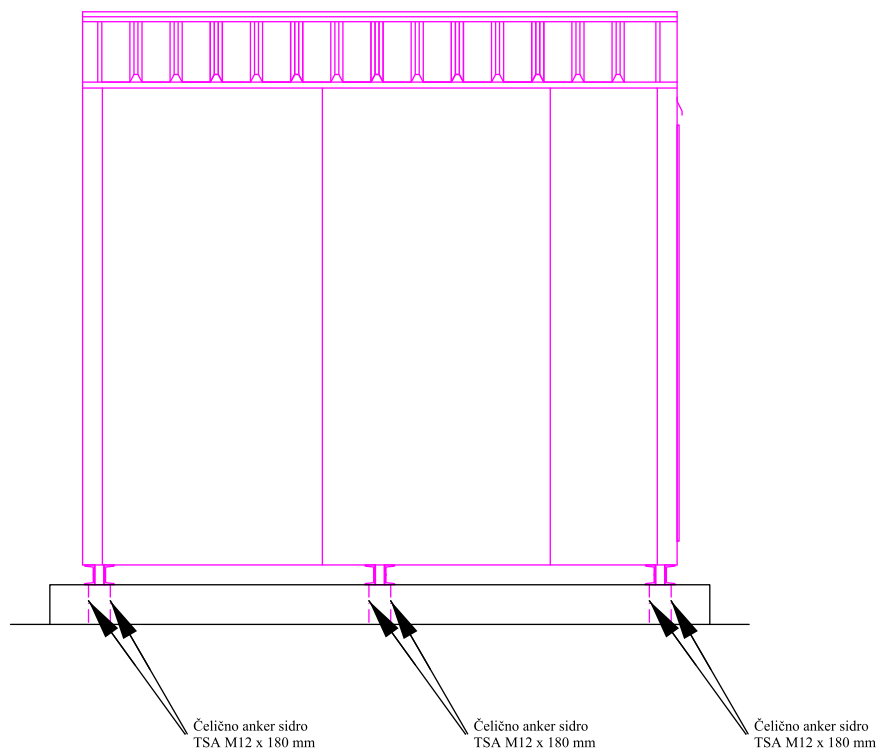


|                                                 |            |                                                          |                                 |   |                               |
|-------------------------------------------------|------------|----------------------------------------------------------|---------------------------------|---|-------------------------------|
| Investitor: BH TELECOM d.d.                     |            | Objekat: Infrastruktura bazne stanice mobilne telefonije |                                 | <br>Dioničko društvo Sarajevo |                               |
| Glavni projekat<br>Knjiga 1/1                   | Faza:<br>A | godina:<br>2018.                                         | šifra projekta: GP-BS-10472-326 |   |                               |
| Naziv crteža: Fasade objekta za smještaj opreme |            |                                                          |                                 | razmjera:<br>1:50                                                                                                  | broj crteža:<br>4 - (151/177) |
|                                                 |            |                                                          |                                 | ovjerio:<br>Projektant:Dženadin Mušinović,d.i.g.                                                                   |                               |




Ugaoni vanjski opšav

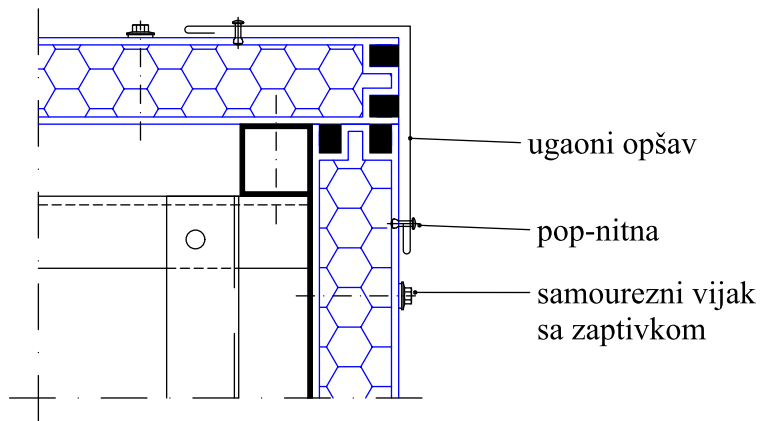


Čeoni lim na višem kraju krova

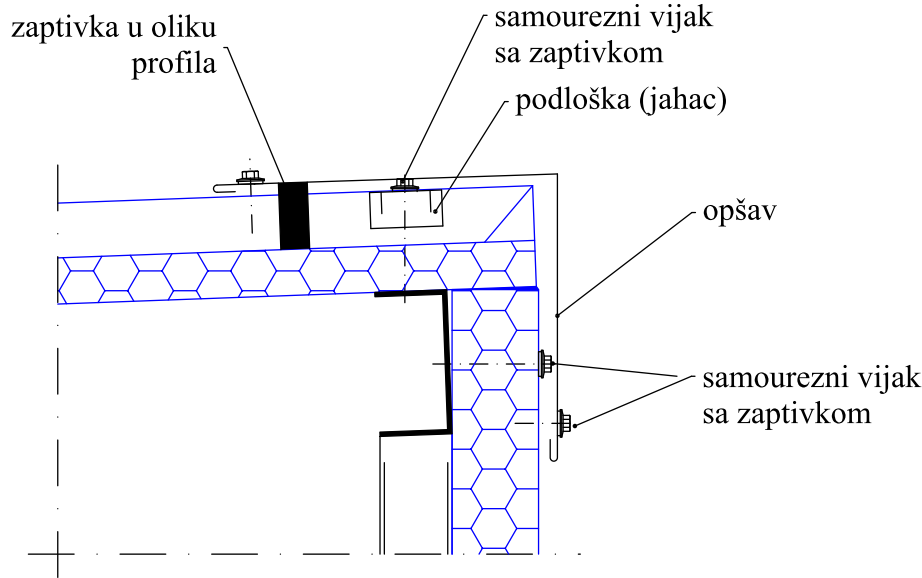

Čeoni lim na nižem kraju krova

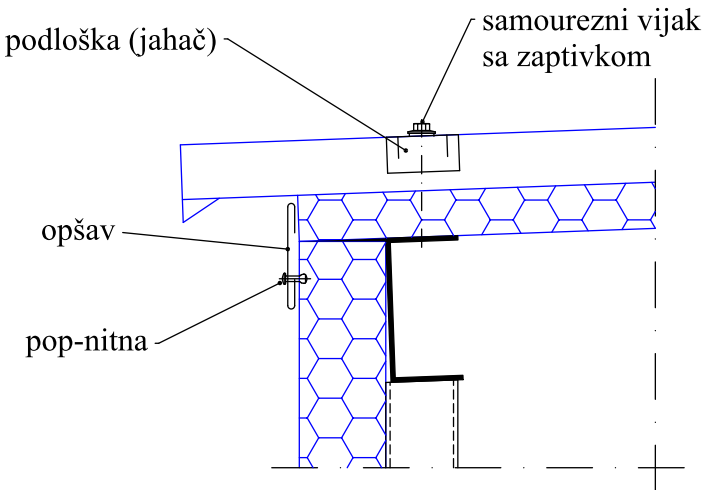


Bočni krovni opšav

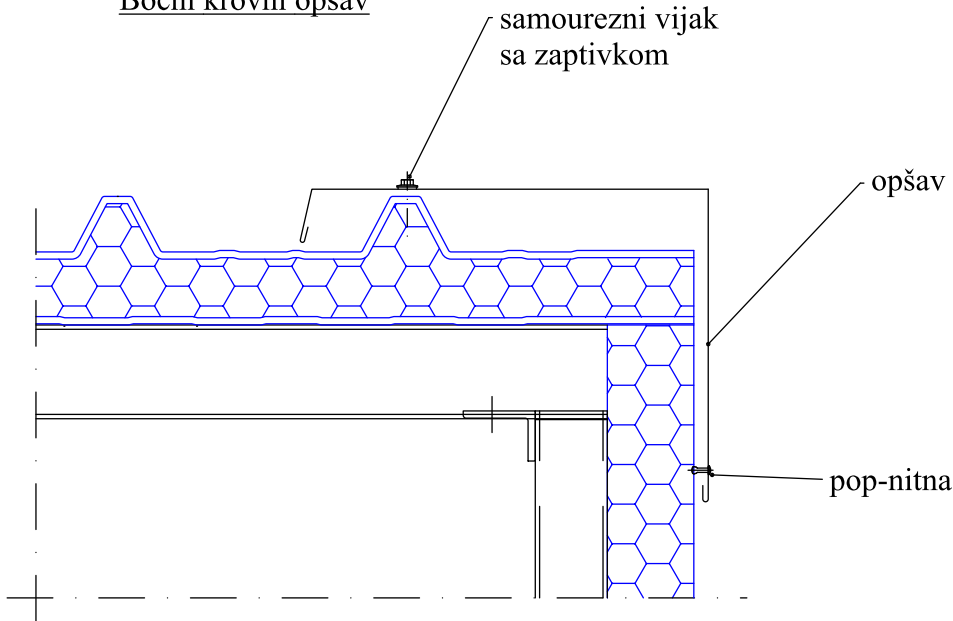


|                                                  |            |                                                          |                                 |                                                |                                                    |
|--------------------------------------------------|------------|----------------------------------------------------------|---------------------------------|------------------------------------------------|----------------------------------------------------|
| Investitor: BH TELECOM d.d.                      |            | Objekat: Infrastruktura bazne stanice mobilne telefonije |                                 | <b>bh telecom</b><br>Dioničko društvo Sarajevo |                                                    |
| Glavni projekat<br>Knjiga 1/1                    | Faza:<br>A | godina:<br>2018.                                         | šifra projekta: GP-BS-10472-326 | broj crteža:<br>5 - (152/177)                  | ovjerio:<br>Projektant: Dženadin Mušinović, d.i.g. |
| Naziv crteža: DETalji objekta za smještaj opreme |            |                                                          |                                 | razmjera:<br>1:50                              |                                                    |

PLAN OPLATE TEMELJNOG BLOKA


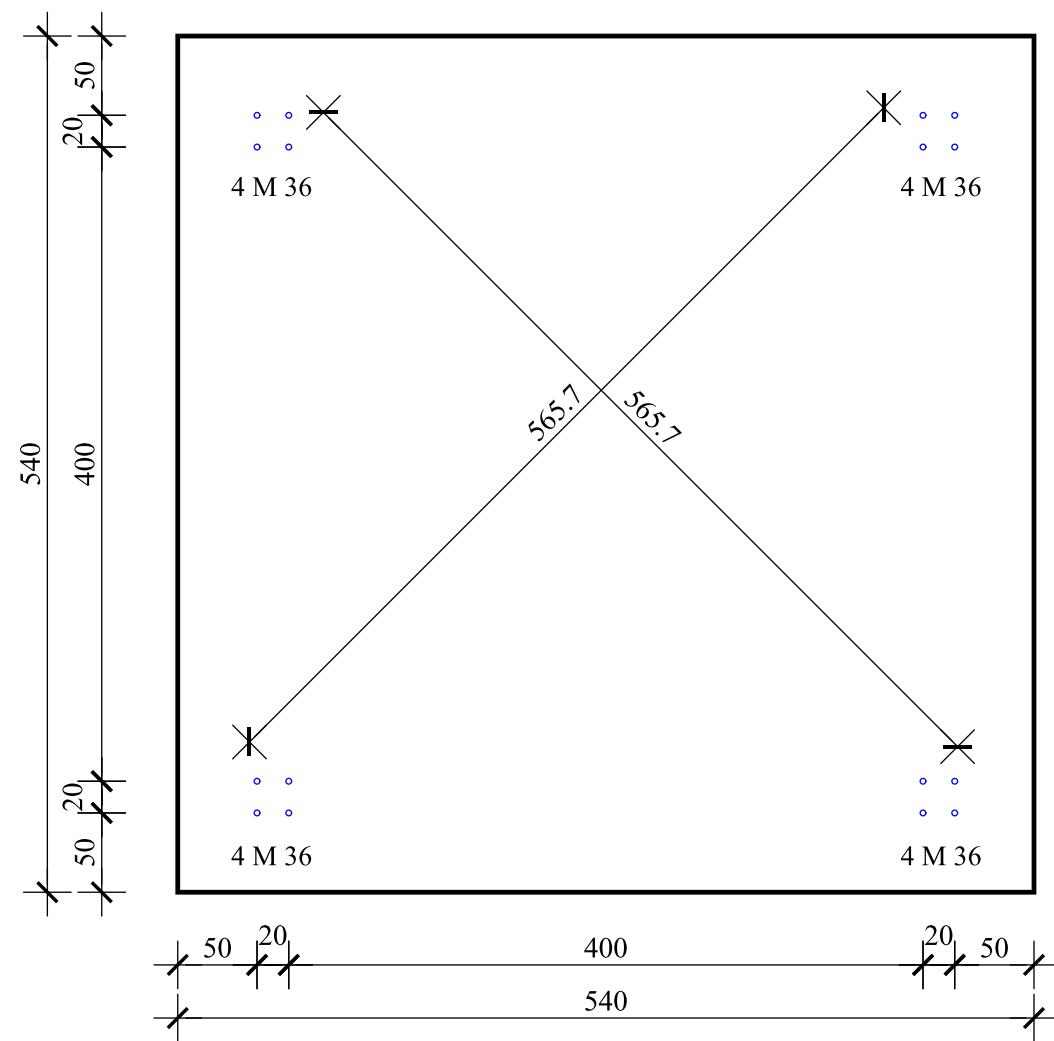


PLAN ARMATURE TEMELJNOG BLOKA

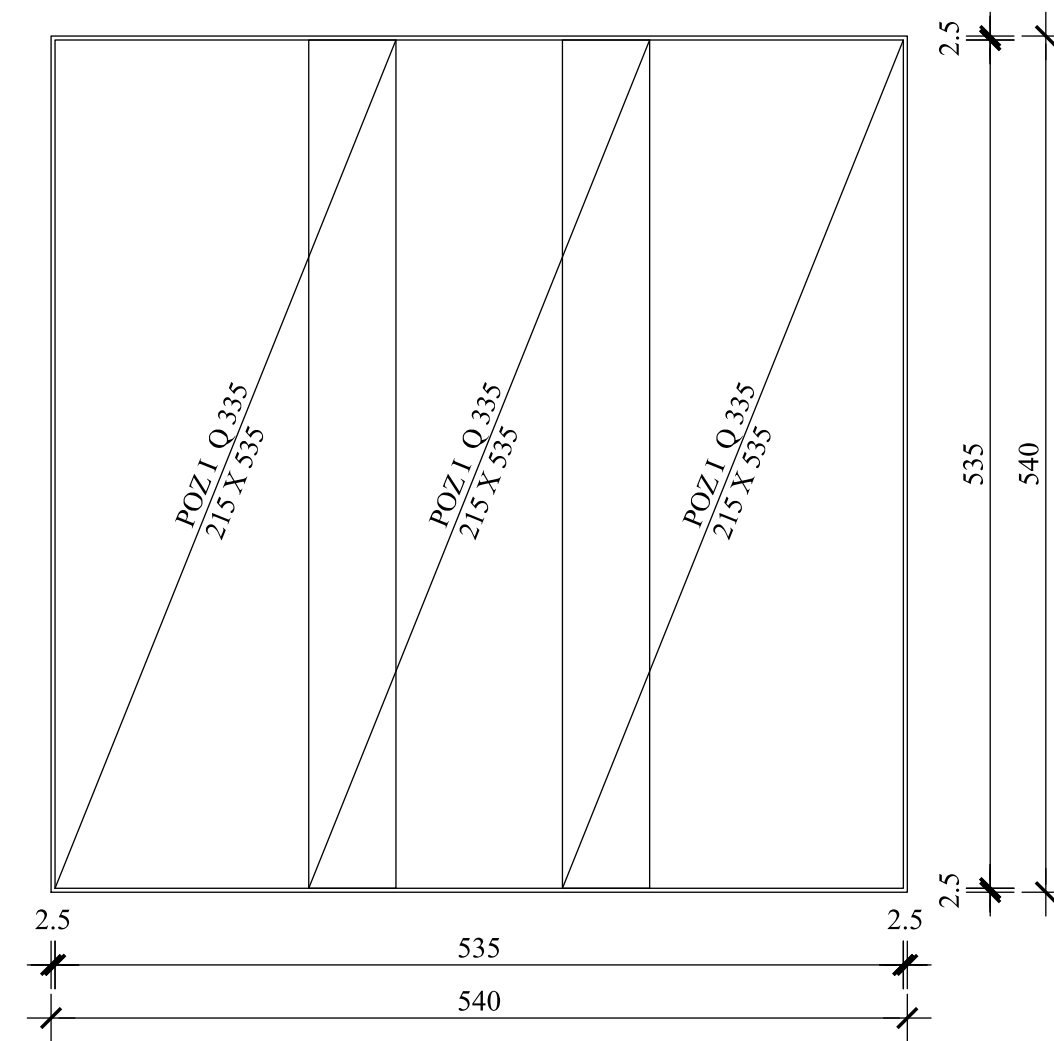

Ankeri Ø 36 mm l = 200 cm komada 4x4=16

Vilice Ø 10 mm/20 cm l = 116 cm komada 4x6=24

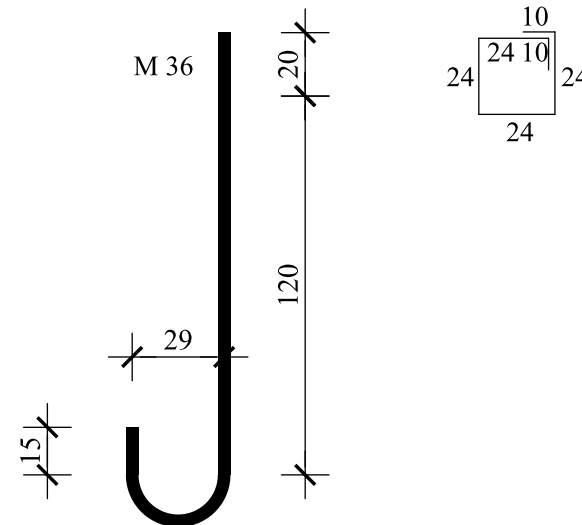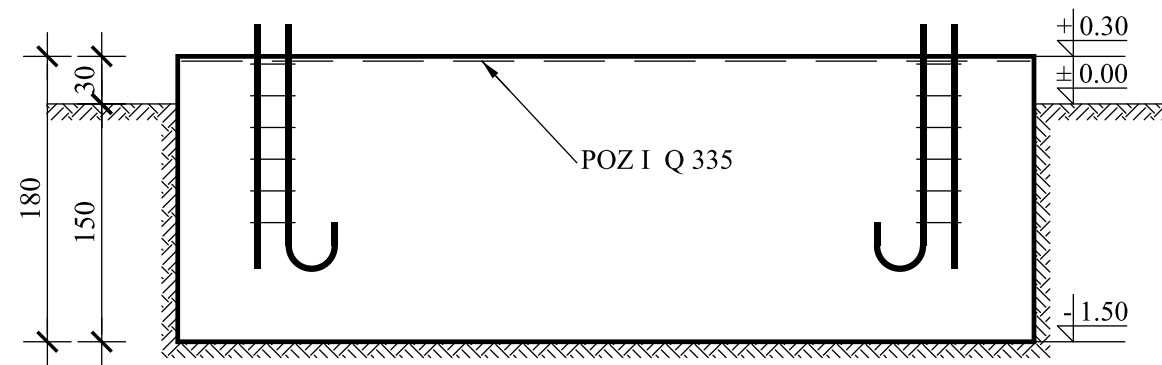


MB 25 (B.I, M-100)  
RA 400/500  
MA 500/560


|                                              |            |                                                          |                                 |   |                                                  |
|----------------------------------------------|------------|----------------------------------------------------------|---------------------------------|---|--------------------------------------------------|
| Investitor: BH TELECOM d.d.                  |            | Objekat: Infrastruktura bazne stanice mobilne telefonije |                                 | <br>Dioničko društvo Sarajevo |                                                  |
| Glavni projekat<br>Knjiga 1/1                | Faza:<br>K | godina:<br>2018.                                         | šifra projekta: GP-BS-10472-326 |   |                                                  |
| Naziv crteža: Plan oplate i armature temelja |            |                                                          | razmjera:<br>1:50               | broj crteža:<br>3 - (121/177)                                                                                      | ovjerio:<br>Projektant:Dženadin Mušinović,d.i.g. |

| INSTALISANA SNAGA: |                          |        |
|--------------------|--------------------------|--------|
| FAZA               | POTROŠAČ                 | SNAGA  |
| L1                 | 2xUPS                    | 6kW    |
| L2                 | UPS+utičnice+klima       | 6,4kW  |
| L3                 | UPS+utičnice+TZ+rasvjeta | 6,6kW  |
| ukupno             |                          | 19kW   |
| maksimalna snga    | $pr_{\Sigma}=0,85$       | 16,1kW |

|                                          |                      |                                                     |                                 |   |   |
|------------------------------------------|----------------------|-----------------------------------------------------|---------------------------------|---|---|
| Investitor: BH TELECOM d.d.              |                      | Objekat: Infrastruktura bazne stanice mobilne mreže |                                 | <div><br/>Dioničko društvo Sarajevo</div> |   |
| Glavni projekat<br>Knjiga EI             | izdanje:<br><b>I</b> | godina:<br>2018.                                    | šifra projekta: GP-BS-10472-326 |   |   |
| Naziv crteža: 3.5.2. Jednopolna šema GRO |                      |                                                     | razmjera:                       | broj crteža:<br>48/69   | Projektant: Moćević Džafer,d.e.i.<br>ovjerio:  |

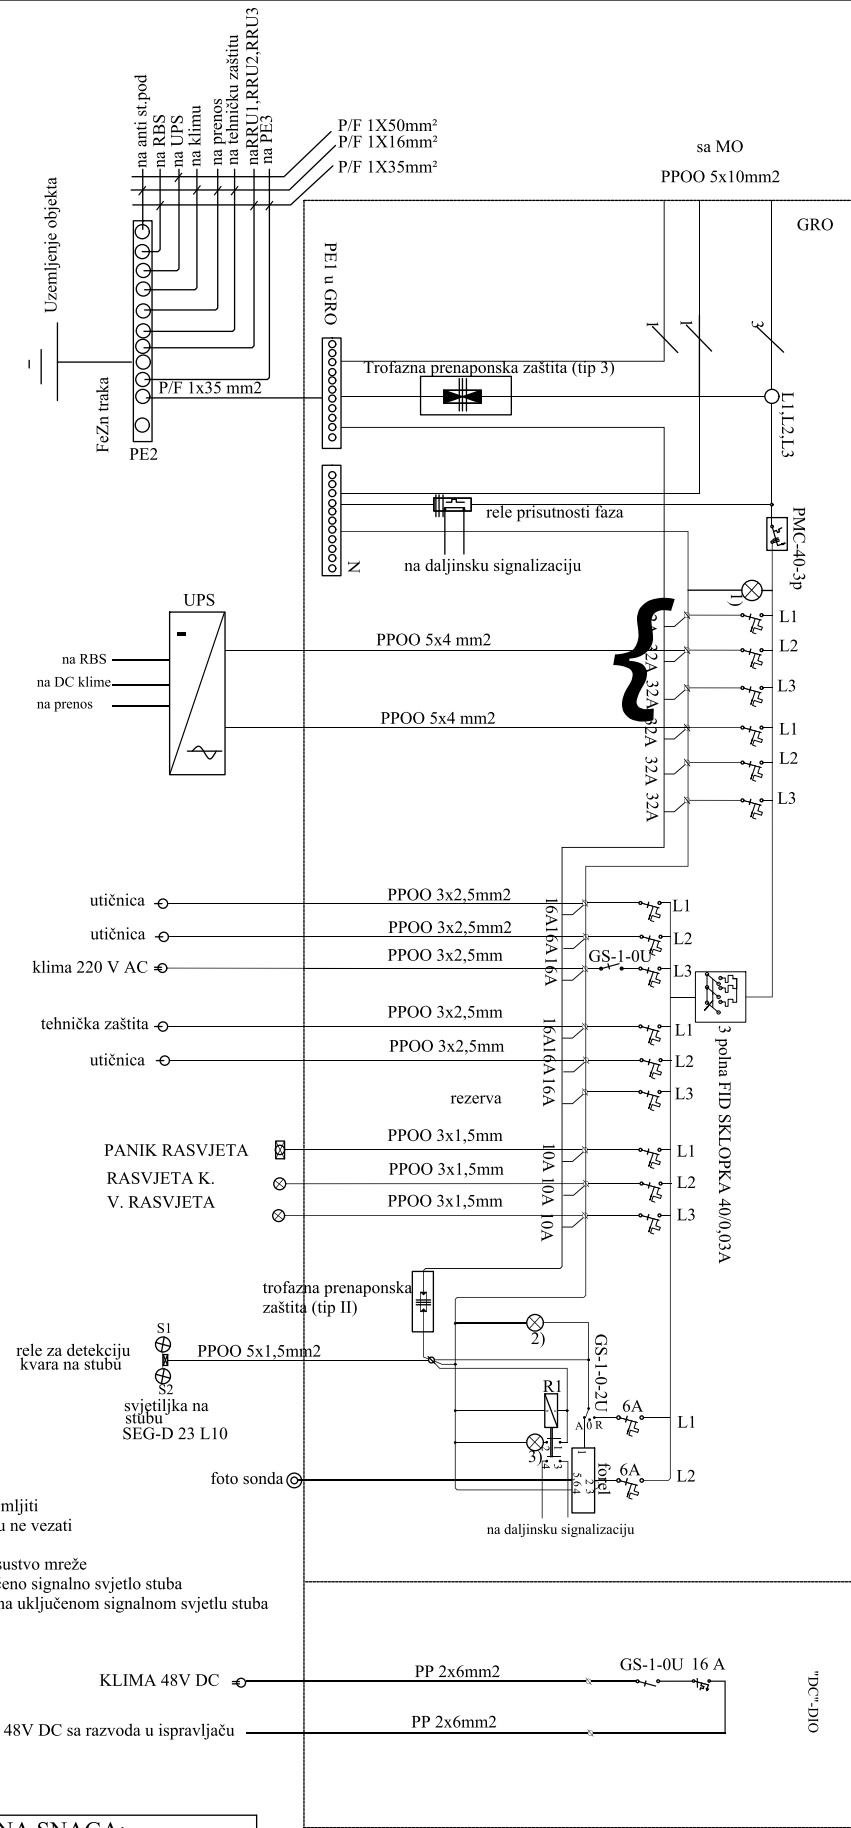

PV Proizvodnja — Heatmap (W, prosjek po satu)

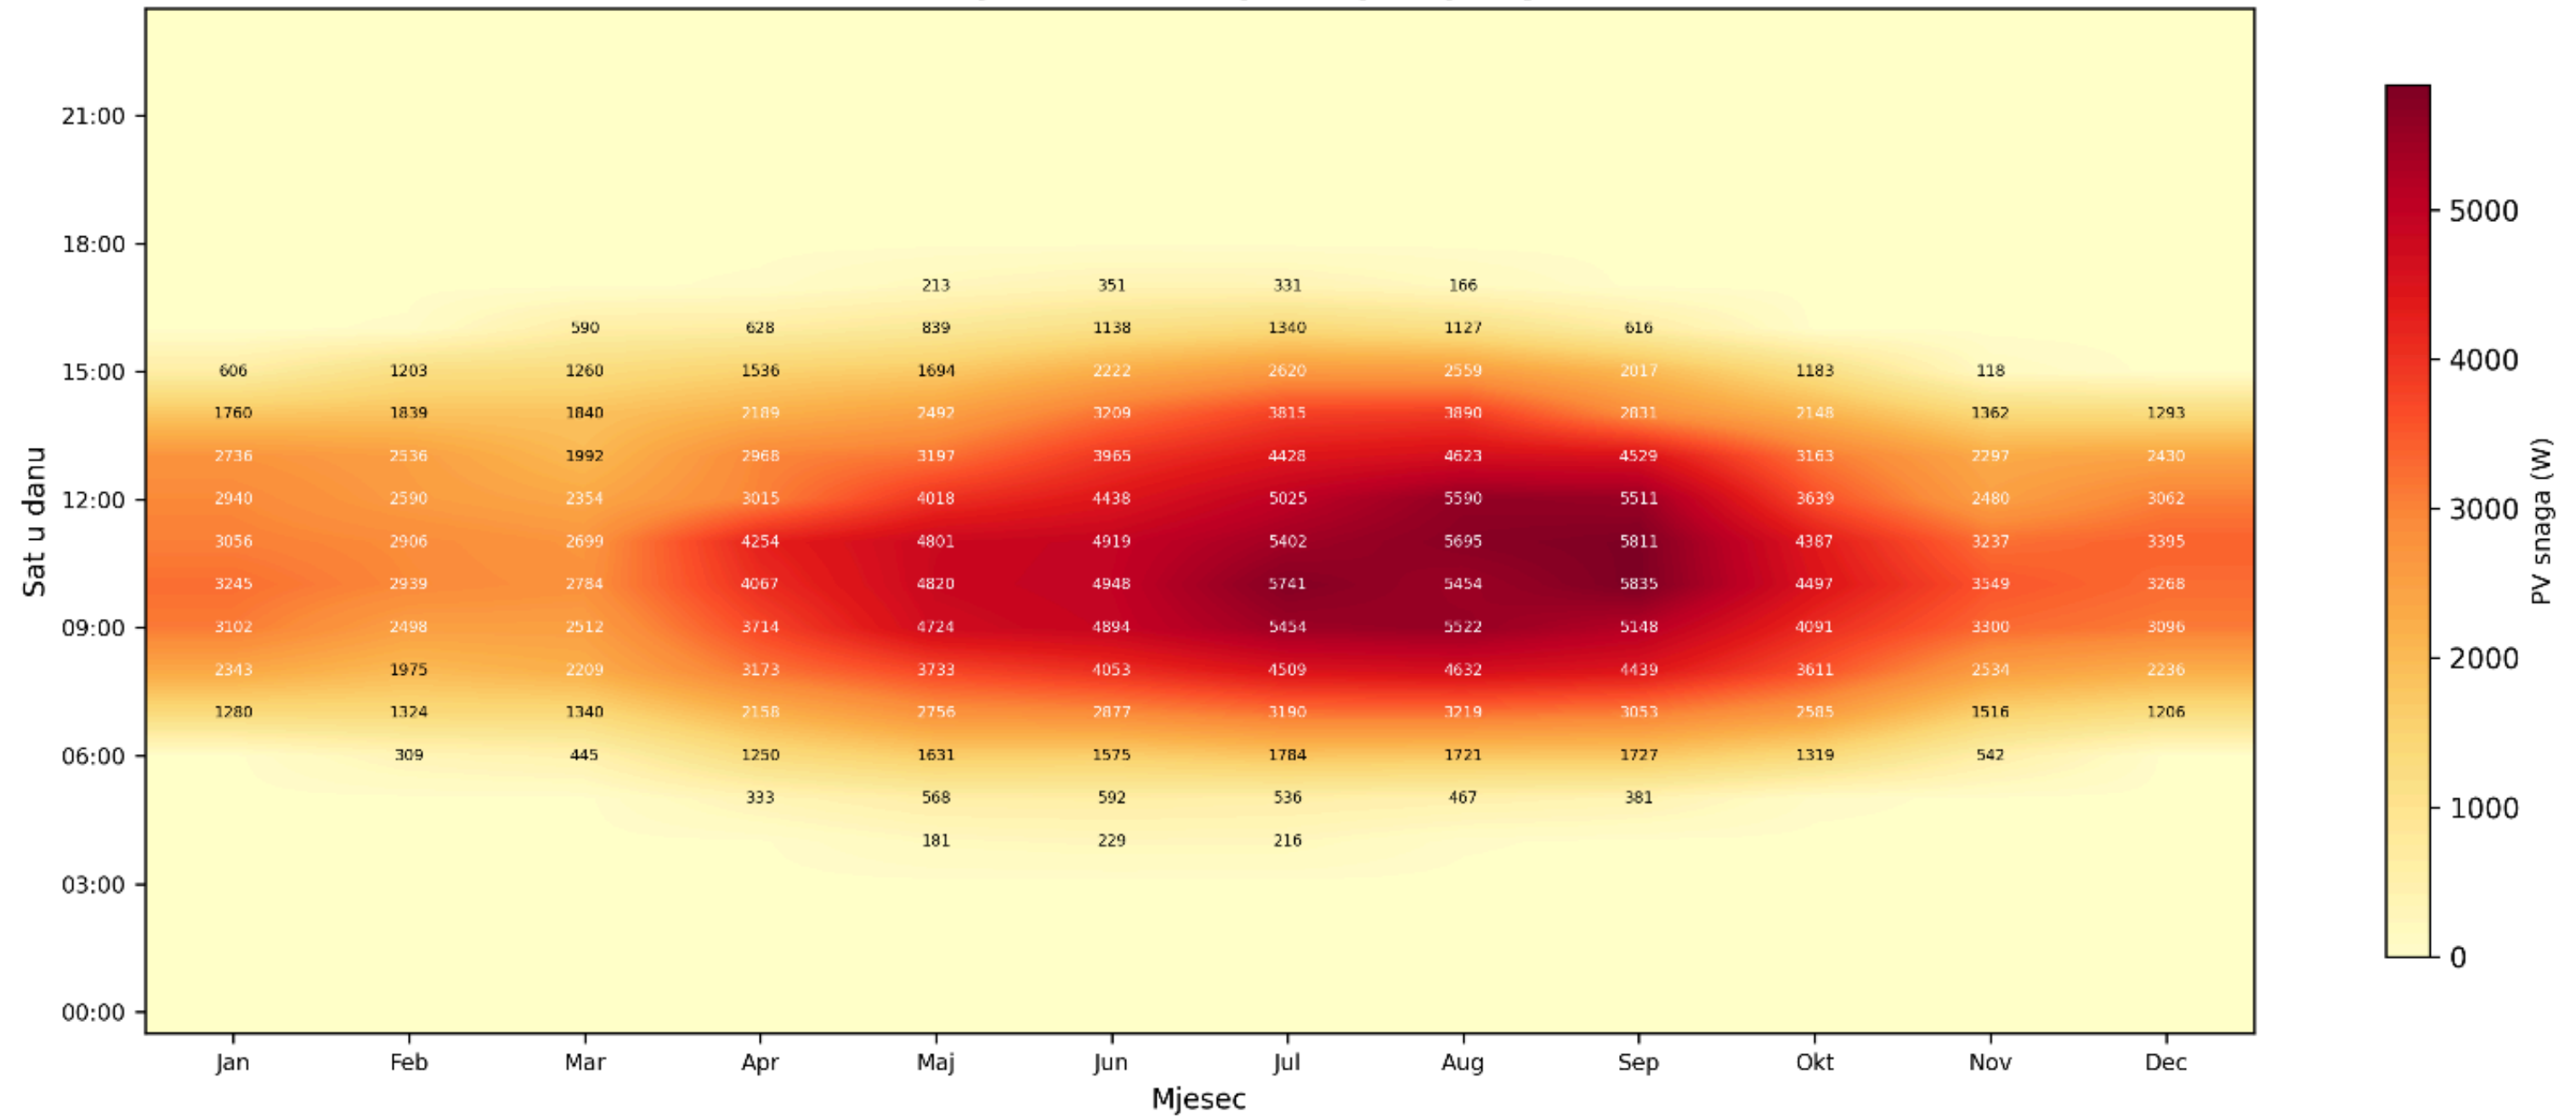

NAPOMENA: Prikazane vrijednosti NISU MJERODAVNE - referentna simulacija sadrzi gresku reda velicine.  
Mjerodavno za 12 x 585 Wp (7,02 kWp): ocekivana godisnja proizvodnja 10,1-10,9 MWh; decembar 560-600 kWh naspram potrosnje 878 kWh - DEA je nuzan.