


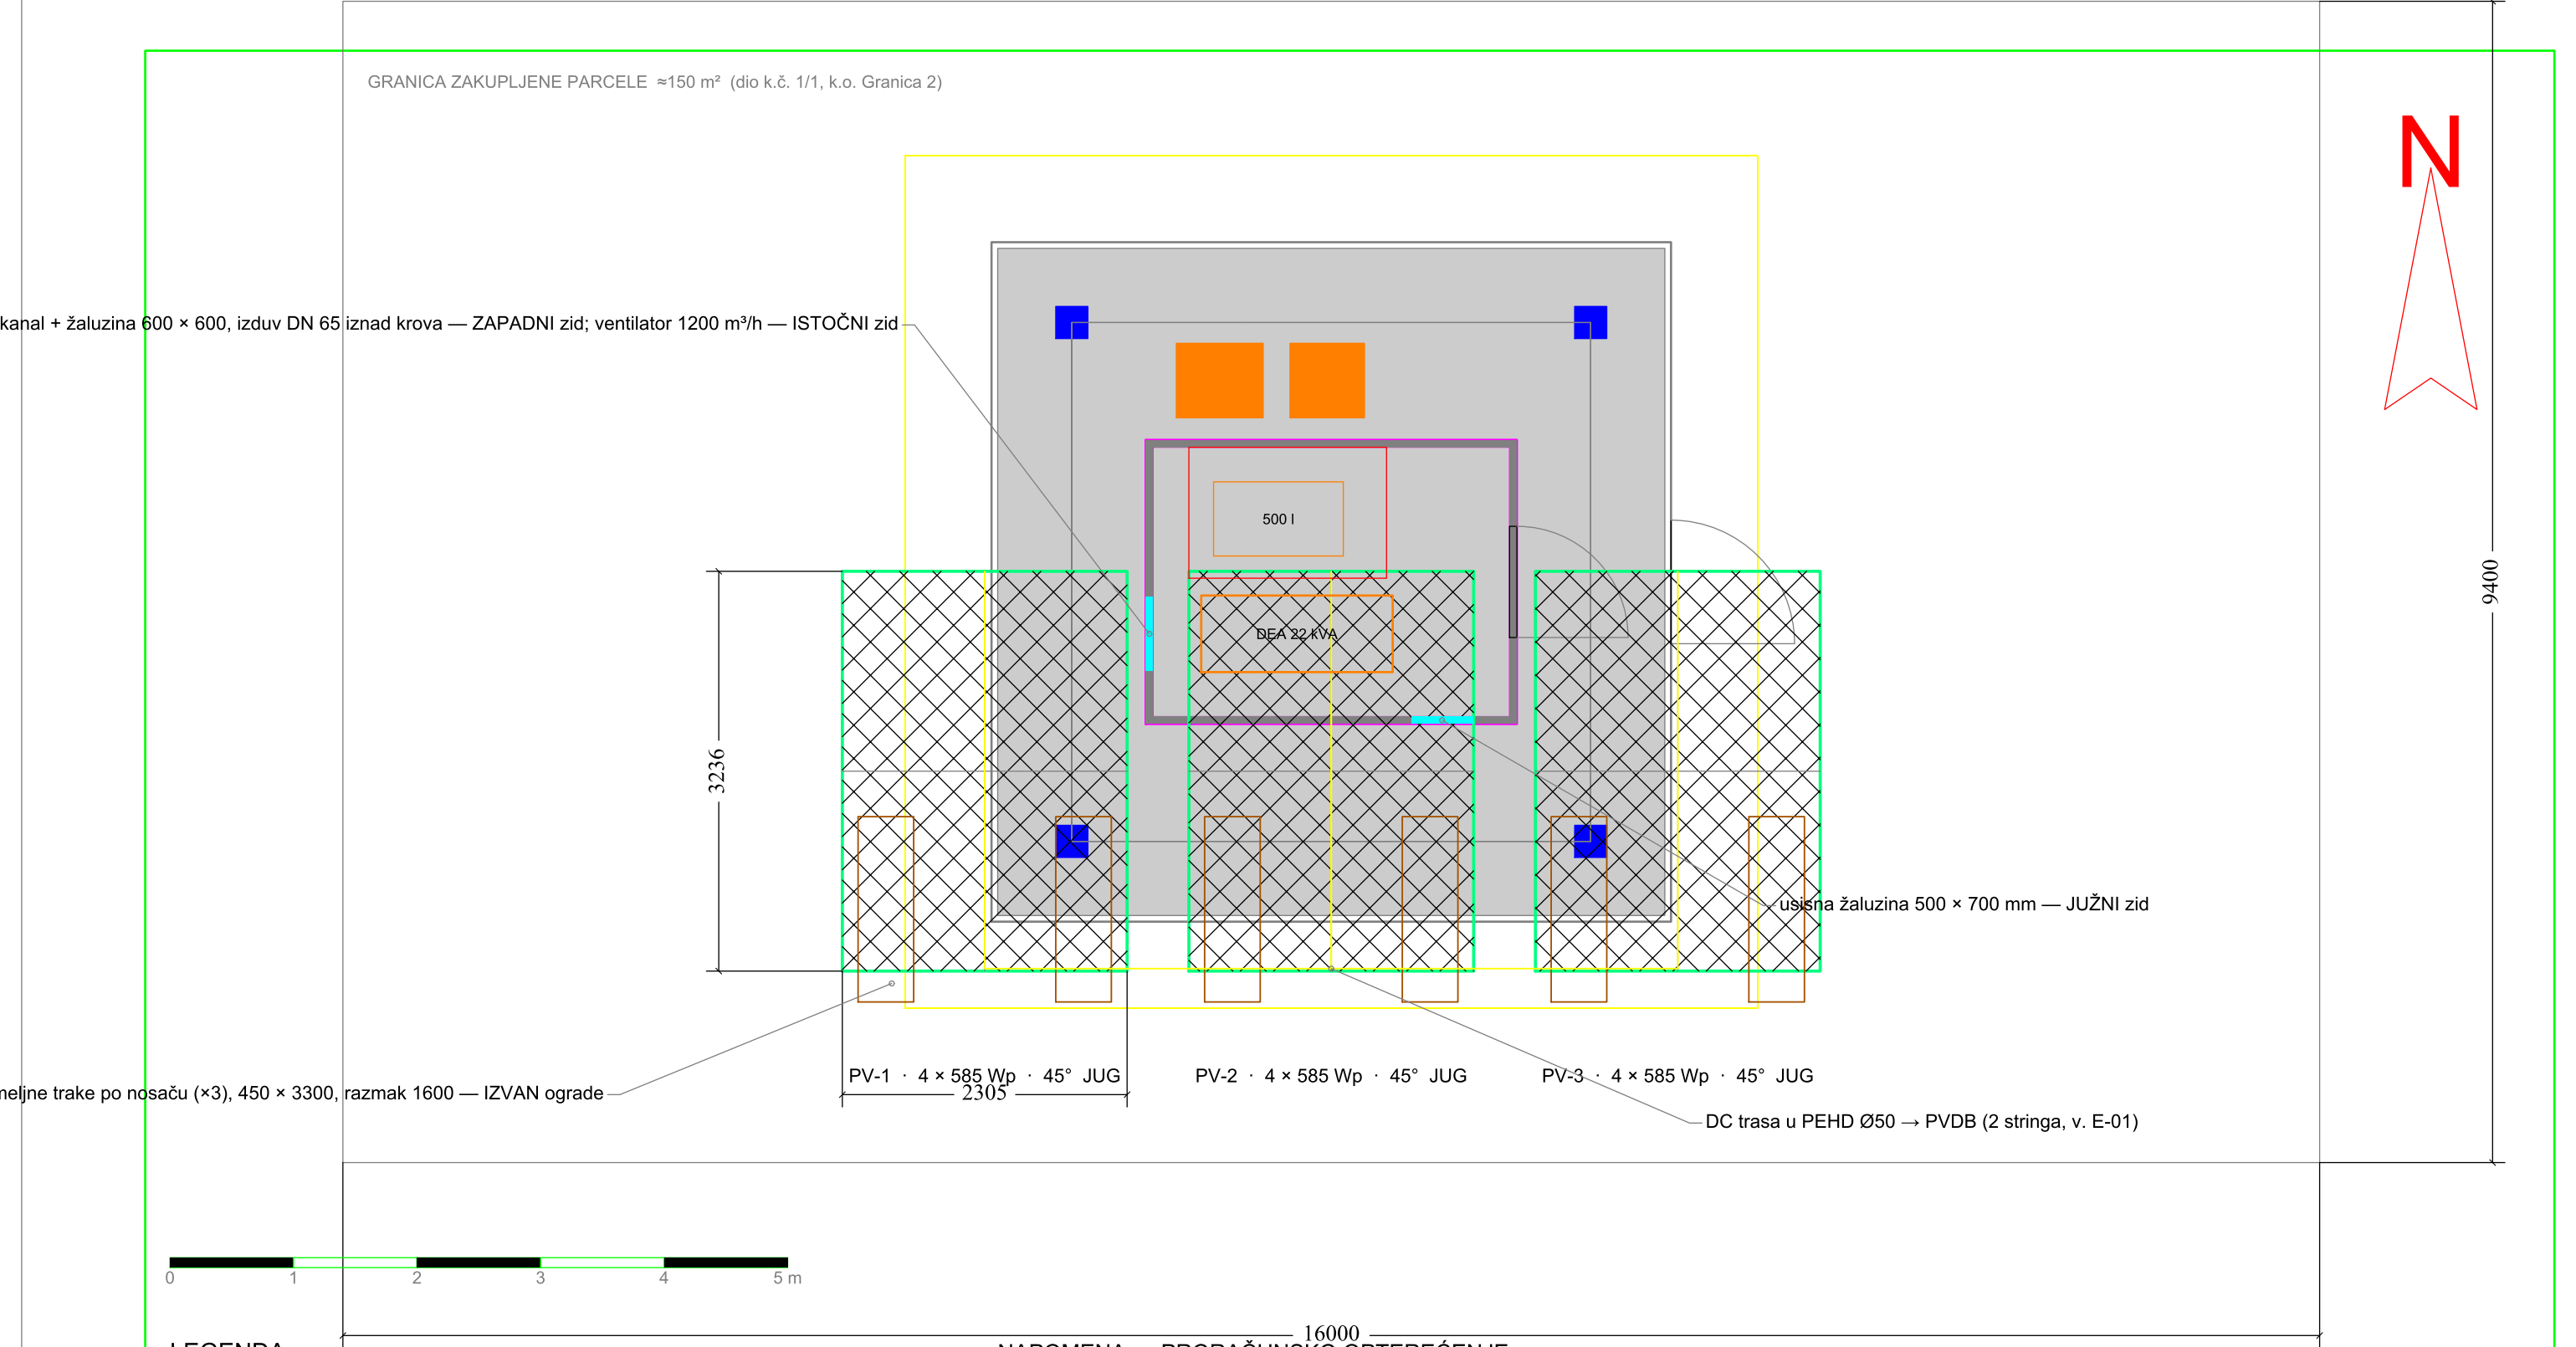

LEGENDA

- LOT 1 — nosači FN panela PV-1..PV-3 (po 4 × 585 Wp, 45°, JUG) — 2 stringa × 6
- LOT 1 — AB temeljne trake 450 × 3300 mm, razmak 1600 mm
- LOT 1 — DC trasa u PEHD Ø50 do PVDB
- LOT 2 — DEA 22 kVA u skid izvedbi i spremnik 500 I
- LOT 2 — usisna žaluzina (JUG); kanal, žaluzina i izduv (ZAPAD); ventilator (ISTOK)

NAPOMENA — PRORAČUNSKO OPTEREĆENJE:

Vjetar $q_p \geq 1,20 \text{ kN/m}^2$ (udar 3 s $\approx 45 \text{ m/s}$) — iznad kapaciteta kataloškog nosača tipa A, stoga CUSTOM IZRADA: sail 10,55 m²/nosaču, ULS uzgon 18,1 kN, moment prevrtanja 62,8 kNm; ovjerava ponuđač (Prilog II, 1.3).
Temelji IZVAN ograde (400 mm od kote ograde); gornja ivica panela +4,74 m, 2836 mm iznad ograde. Kontejner je PRAZAN.



BH TELECOM d.d. SARAJEVO

Izvršna direkcija za tehnologiju i razvoj servisa

Investitor:

BH Telecom d.d. Sarajevo, Franca Lehara 7, Sarajevo

Objekat:

BS SJEDNICA (Bileća) — autonomni hibridni sistem napajanja

Faza:

Tenderska dokumentacija — Prilog III

Naziv crteža:

Situacija — BUDUĆE STANJE (LOT 1 + LOT 2)

Projektant:

Rusmir Skopljak, dipl. ing. el.

ovjerio:

Rusmir Skopljak, dipl. ing. el.

šifra projekta:

BHT-SJEDNICA-2026

razmjera:

1:50

godina / broj crteža:

2026. S-02