OSNOVA — kontejner je PRAZAN

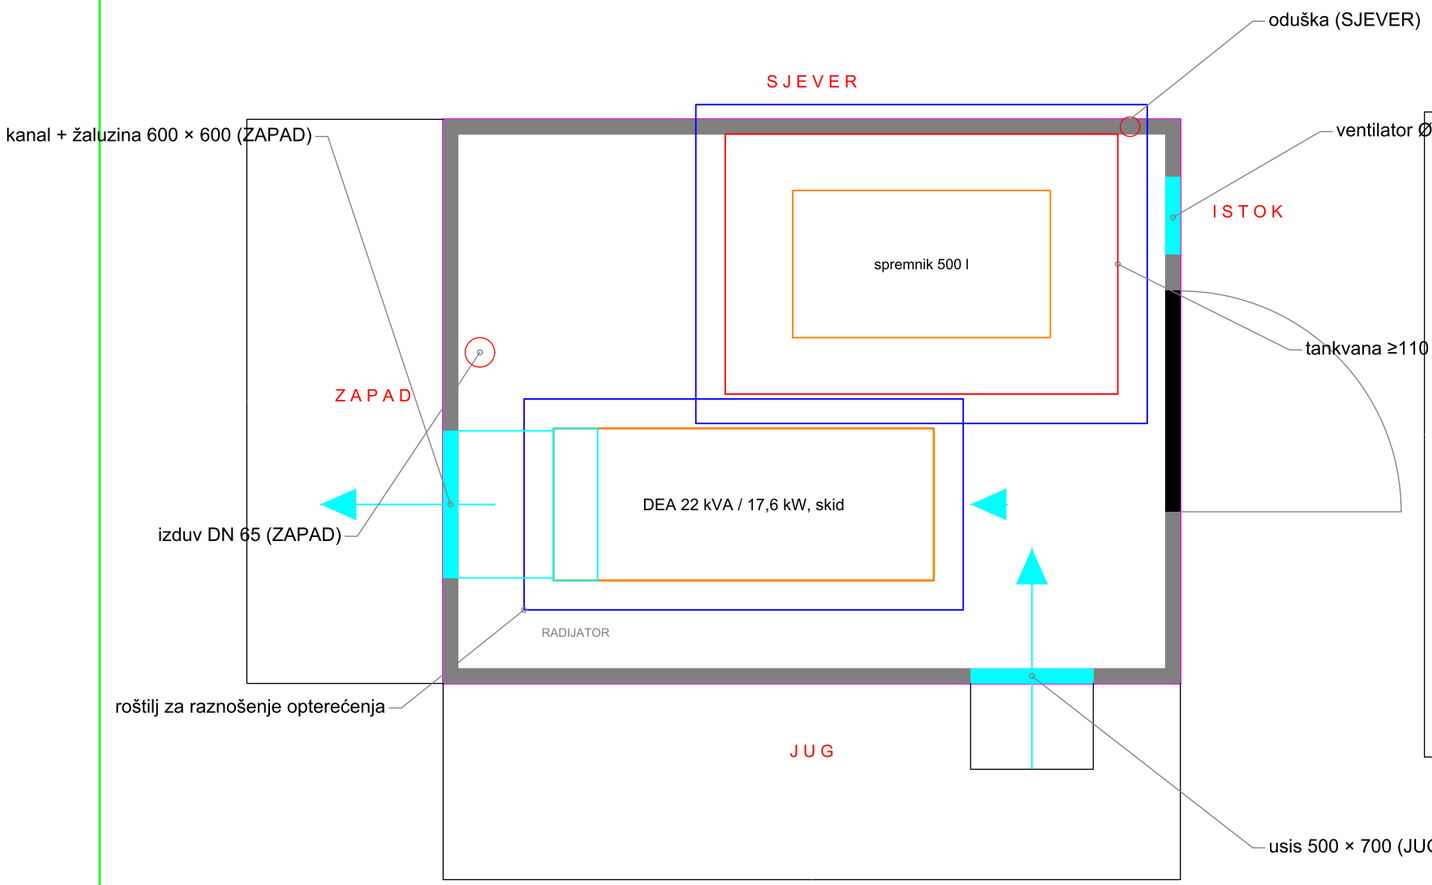

PRESJEK 1–1 (pogled prema SJEVERU — ZAPAD lijevo)

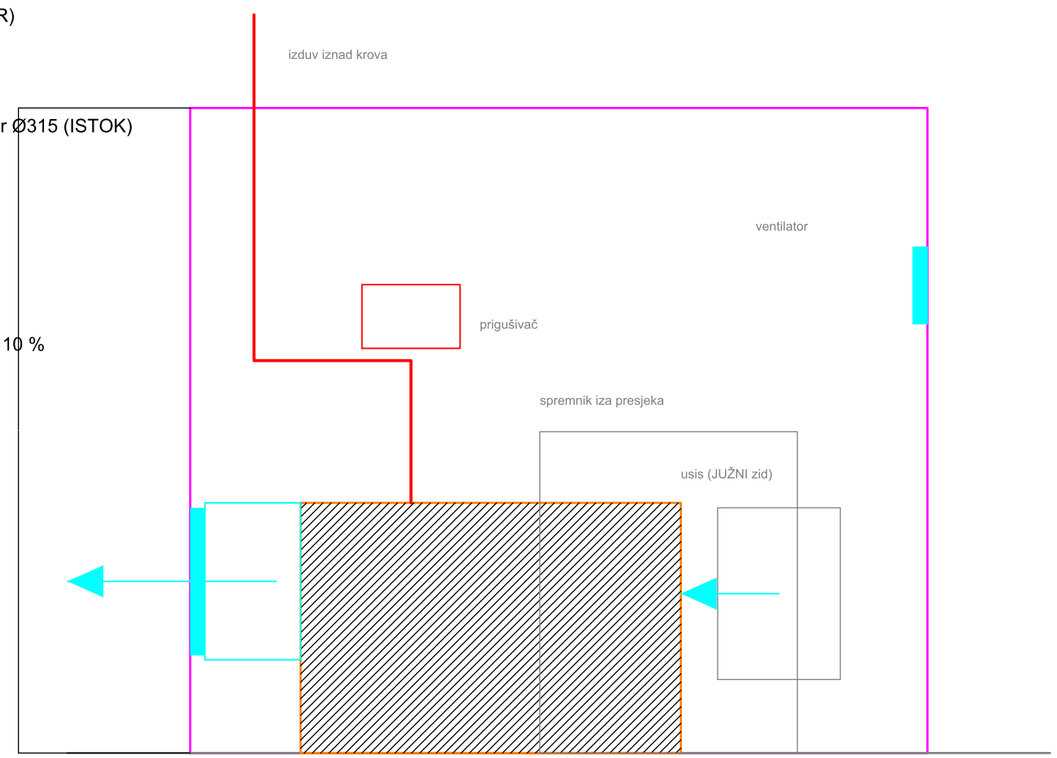

NAPOMENE:

1 FG Wilson P22-6 (Skid), TL 2019-08-14: hladnjak 1980 m³/h, sagorijevanje 90 m³/h, toplota u prostor 7,1 kW, maks. vanjski otpor 125 Pa.
2 Žaluzine zadovoljavaju: usis 500 × 700 (Δp≈16 Pa) + izlaz 600 × 600 (≈15 Pa) + kanal < 125 Pa.
3 Ventilator 1200 m³/h je DOPUNSKA ventilacija (min. 120 m³/h); protok hlađenja daje ventilator hladnjaka.
4 Izduv DN 65 usvojen (NO 50 zadovoljava protutlak, ali radi pri 33 m/s).
5 Pod je dimenzionisan na 10,00 kN/m² ravnomjerno raspodijeljeno (projekat lokacije, 4.4.2.3). Agregat 3,93 i pun spremnik 9,2 kN/m² su KONCENTRISANI — roštilj za raznošenje je OBAVEZAN.
6 RASPORED: usis JUG (+0,30), kanal/izlaz i izduv ZAPAD, oduška SJEVER, ventilator ISTOK; ≥3 m između usisa, izduva i oduške. Ništa ne izbacuje prema ormarima na SJEVERU.
7 UNOS: skid 620 mm kroz vrata 900 mm. Kontejner je PRAZAN.

BH TELECOM d.d. SARAJEVO
Izvršna direkcija za tehnologiju i razvoj servisa

Investitor: BH Telecom d.d. Sarajevo, Franca Lehara 7, Sarajevo

Objekat: BS SJEDNICA (Bileća) — autonomni hibridni sistem napajanja

Faza: Tenderska dokumentacija — Prilog III

šifra projekta: BHT-SJEDNICA-2026

Naziv crteža: DEA u postojećem kontejneru — osnova i presjek

razmjera: 1:25

Projektant: Rusmir Skopljak, dipl. ing. el.

ovjerio: Rusmir Skopljak, dipl. ing. el.

godina / broj crteža: 2026. M-01