


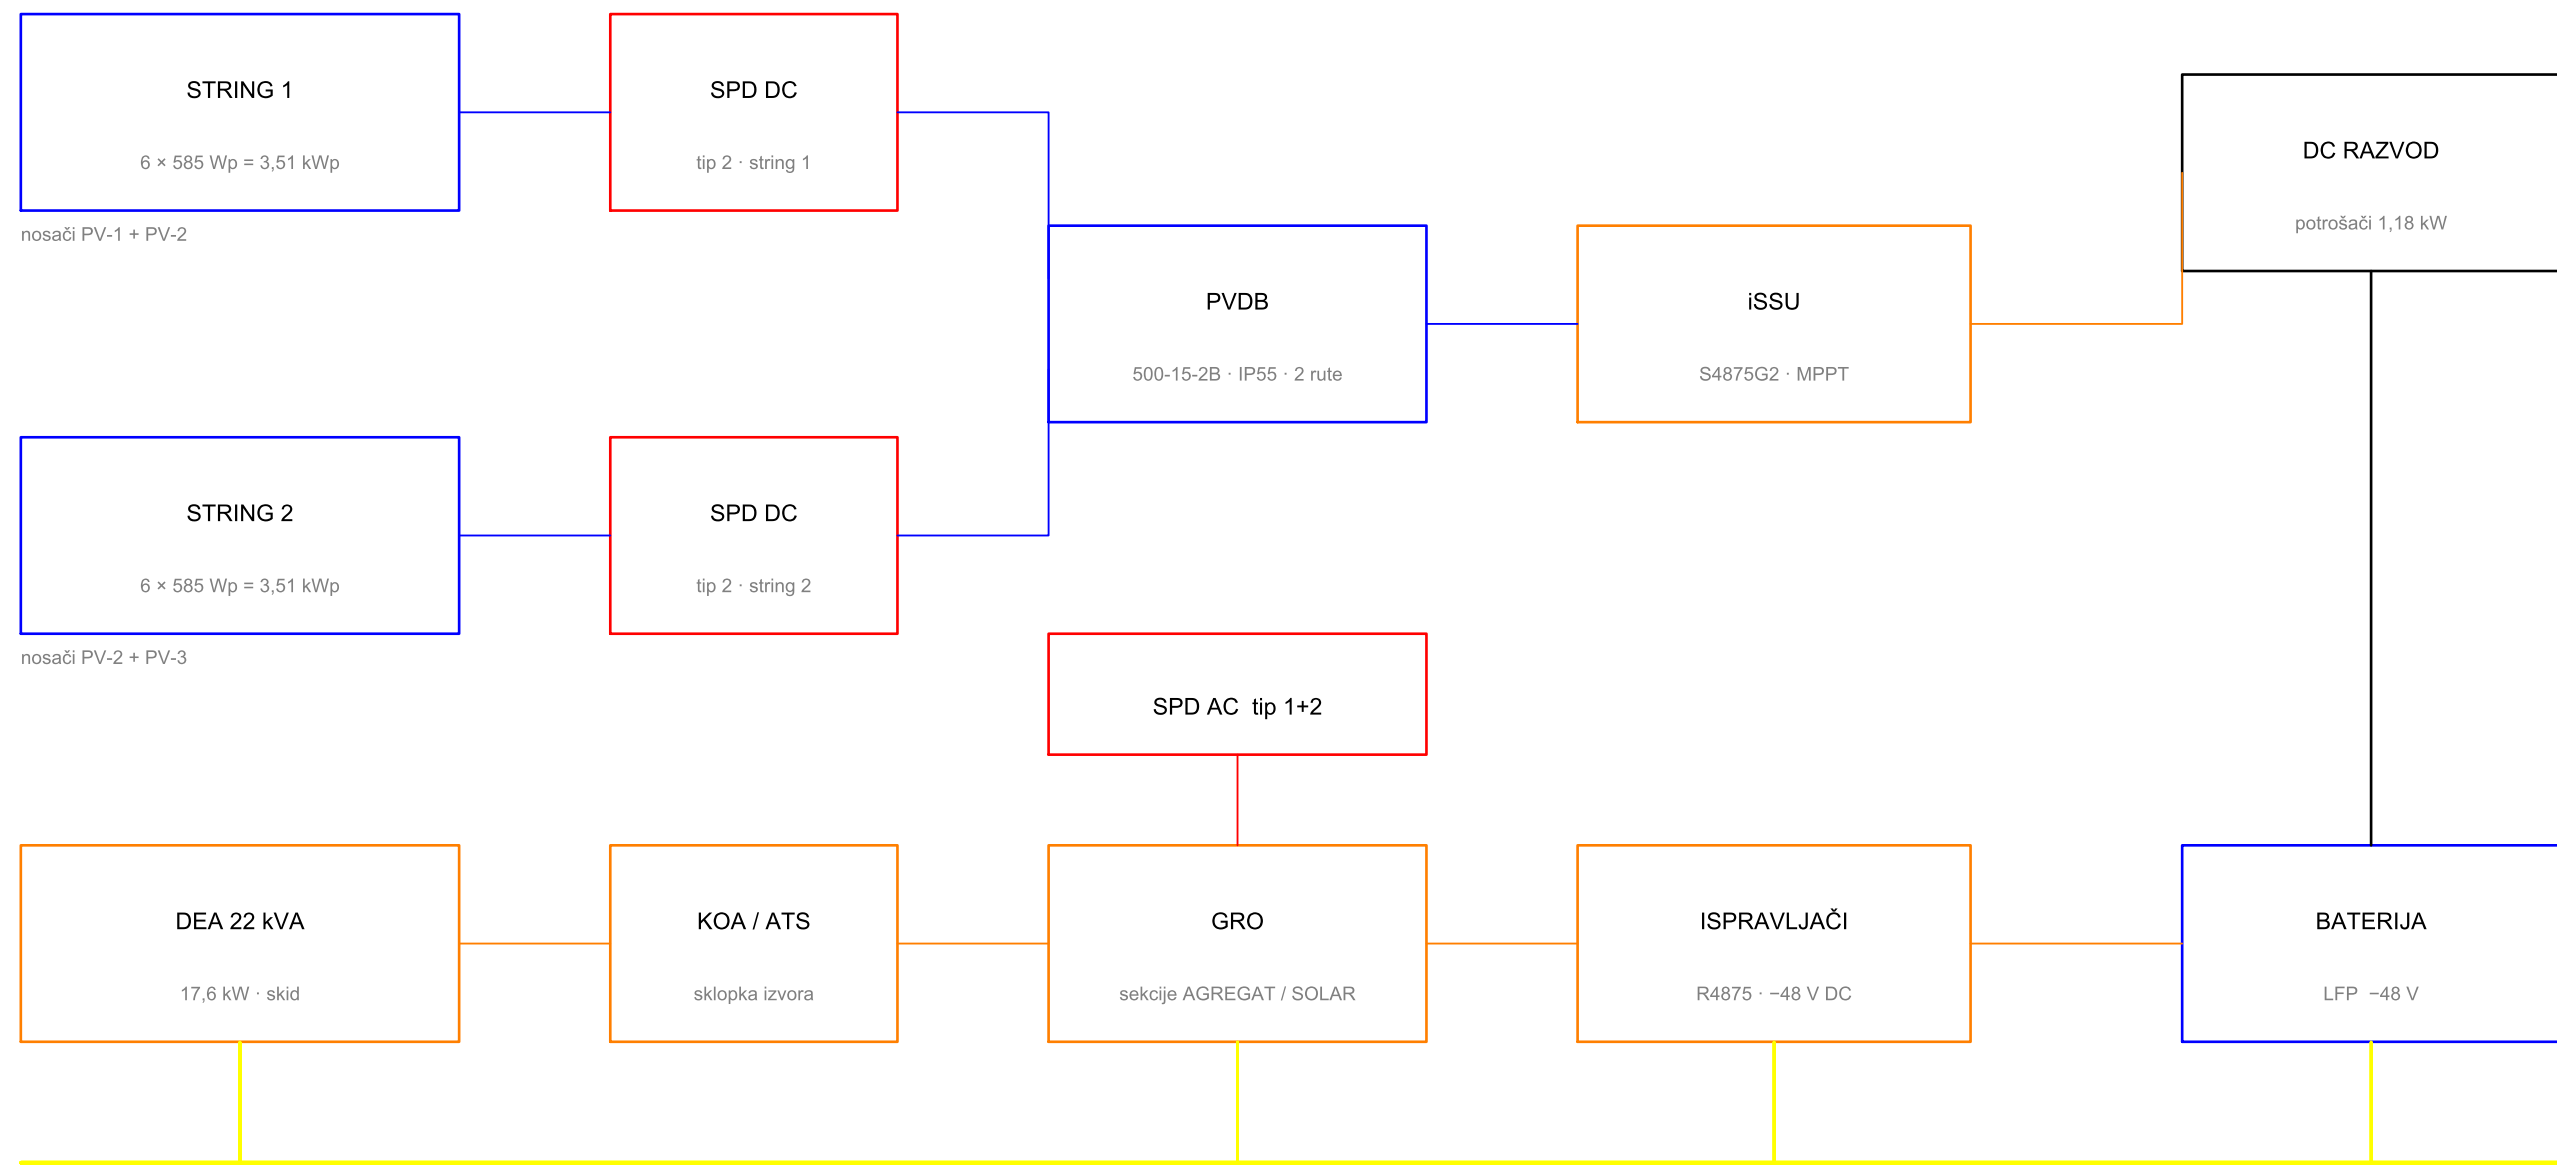

postojeći prstenasti uzemljivač Fe/Zn 25×4 · R ≤ 10 Ω · nosači FN vezani bakrenim užetom 50 mm² preko bimetalnih spojeva

NAPOMENE:

- 1 Lokacija NIJE na mreži — DEA je jedini AC izvor; KOA/ATS je sklopka izvora, ne prebacivanje sa mreže.
- 2 Uzemljenje o točnog izvora TN-S: tačka spajanja N-PE u novom GRO, ne u postojećem PMO.
- 3 Prenaponska zaštita: AC tip 1+2 (objekat ima LPS), DC tip 2 po stringu, signalni vodovi EN 61643-21.
- 4 Zaštita u GRO mora isključiti prema IEC 60364-4-41 pri struji kvara ograničenoj pobudom generatora.
- 5 FN polja su unutar zone zaštite antenskog stuba $h=38$ m (EN 62305).
- 6 12 modula = 2 stringa $\times$ 6 (na 3 nosača $\times$ 4); PVDB ima 2 rute, po jedan DC odvodnik po stringu.

 BH TELECOM d.d. SARAJEVO Izvršna direkcija za tehnologiju i razvoj servisa	
Investitor: BH Telecom d.d. Sarajevo, Franca Lehara 7, Sarajevo	
Objekat: BS SJEDNICA (Bileća) — autonomni hibridni sistem napajanja	
Faza: Tenderska dokumentacija — Prilog III	šifra projekta: BHT-SJEDNICA-2026
Naziv crteža: Jednopolna shema — hibridni sistem napajanja	razmjera: —
Projektant: Rusmir Skopliak, dipl. inq. el.	ovjeno: Rusmir Skopliak, dipl. inq. el.
godina / broj crteža: 2026. E-01	