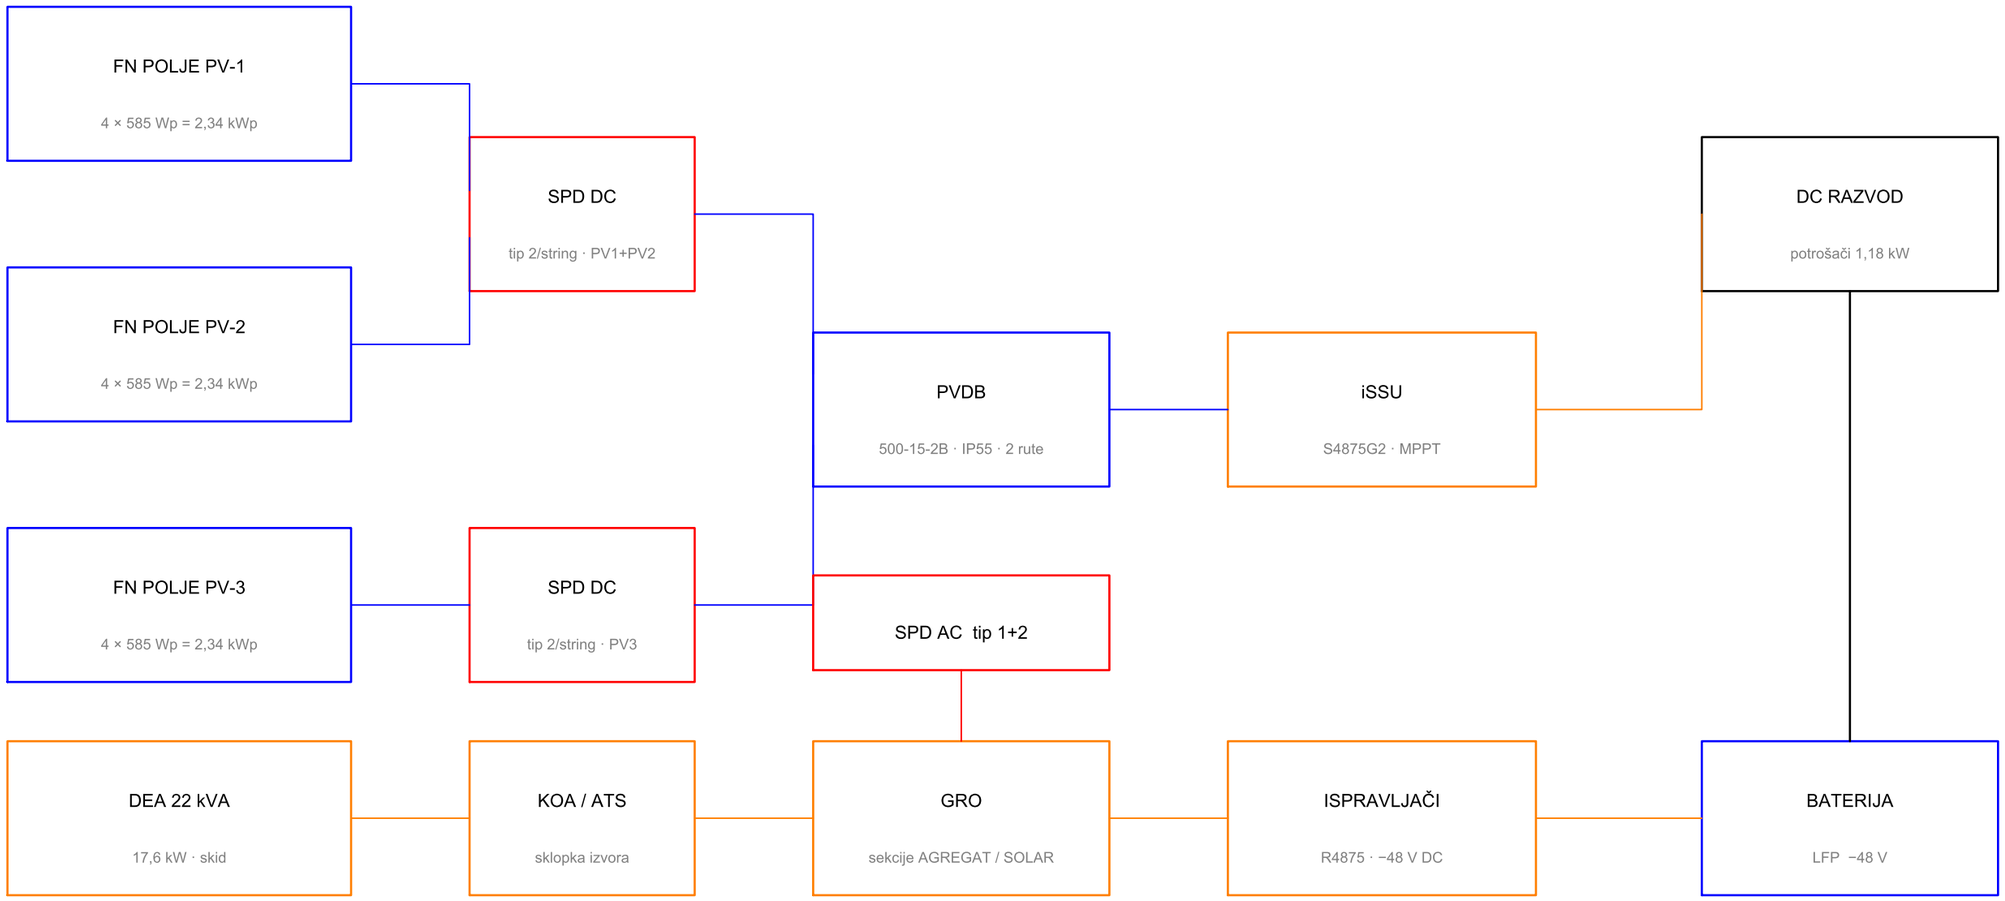

postojeći prstenasti uzemljivač Fe/Zn 25×4 · R ≤ 10 Ω · nosači FN vezani bakrenim užetom 50 mm² preko bimetalnih spojeva

NAPOMENE:

1 Lokacija NIJE priključena na elektroenergetsku mrežu — DEA je jedini AC izvor, te KOA/ATS radi kao sklopka izvora, a ne kao prebacivanje sa mreže.
2 Sistem uzemljenja otočnog izvora (TN-S) definisati projektom: tačka spajanja N-PE je u novom GRO, a ne u postojećem PMO koji više nema izvor napajanja.
3 Prenaponska zaštita: tip 1+2 na AC strani (objekat ima vanjski LPS), tip 2 po stringu na DC strani, te zaštita signalnih vodova prema EN 62305-4.
4 Zaštitni uređaj u GRO mora obezbijediti automatsko isključenje prema IEC 60364-4-41 pri struji kvara ograničenoj SHUNT pobudom generatora.
5 FN polja su unutar zone zaštite antenskog stuba h=38 m prema EN 62305.
6 3 nosača × 4 modula (v. S-02/S-03, F.6): svaki string kompletan po nosaču (bez dijeljenja stringa preko dva nosača). PVDB ima 2 rute — PV-1+PV-2 paralelno na rutu 1, PV-3 samostalno na rutu 2.

BH TELECOM d.d. SARAJEVO
Izvršna direkcija za tehnologiju i razvoj servisa

Investitor:
BH Telecom d.d. Sarajevo, Franca Lehara 7, Sarajevo

Objekat:
BS SJEDNICA (Bileća) — autonomni hibridni sistem napajanja

Faza:	šifra projekta:
Tenderska dokumentacija — Prilog III	BHT-SJEDNICA-2026

Naziv crteža:	razmjera:
Jednopolna shema — hibridni sistem napajanja	—

Projektant:	ovjerio:	godina / broj crteža:
Rusmir Skopljak, dipl. ing. el.	Rusmir Skopljak, dipl. ing. el.	2026. E-01