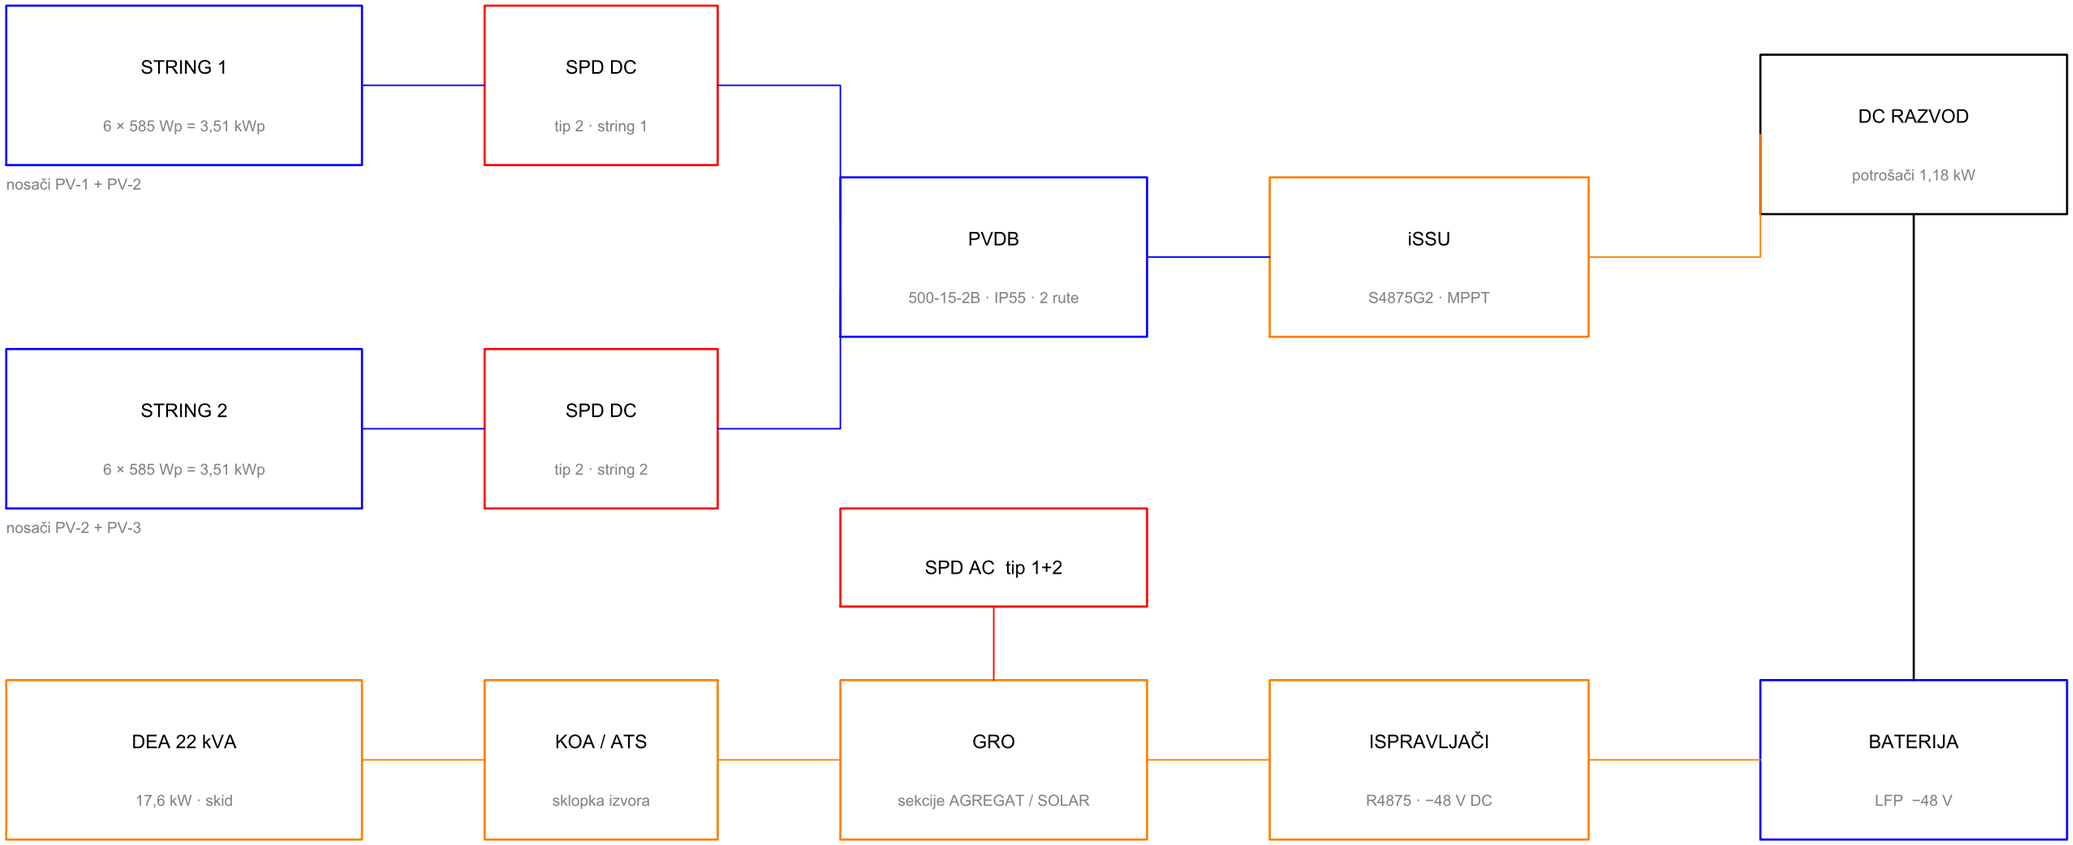



postojeći prstenasti uzemljivač Fe/Zn 25×4 · R ≤ 10 Ω · nosači FN vezani bakrenim užetom 50 mm² preko bimetalnih spojeva

NAPOMENE:
1 Lokacija NIJE na mreži — DEA je jedini AC izvor; KOA/ATS je sklopka izvora, ne prebacivanje sa mreže.
2 Uzemljenje otočnog izvora TN-S: tačka spajanja N-PE u novom GRO, ne u postojećem PMO.
3 Prenaponska zaštita: AC tip 1+2 (objekat ima LPS), DC tip 2 po stringu, signalni vodovi EN 61643-21.
4 Zaštita u GRO mora isključiti prema IEC 60364-4-41 pri struji kvara ograničenoj pobudom generatora.
5 FN polja su unutar zone zaštite antenskog stuba h=38 m (EN 62305).
6 12 modula = 2 stringa × 6 (na 3 nosača × 4); PVDB ima 2 rute, po jedan DC odvodnik po stringu.

BH TELECOM d.d. SARAJEVO
Izvršna direkcija za tehnologiju i razvoj servisa

Investitor:
BH Telecom d.d. Sarajevo, Franca Lehara 7, Sarajevo

Objekat:
BS SJEDNICA (Bileća) — autonomni hibridni sistem napajanja

Faza:
Tenderska dokumentacija — Prilog III

šifra projekta:
BHT-SJEDNICA-2026

Naziv crteža:
Jednopolna shema — hibridni sistem napajanja

razmjera:
—

Projektant:
Rusmir Skopljak, dipl. ing. el.

ovjerio:
Rusmir Skopljak, dipl. ing. el.

godina / broj crteža:
2026. E-01