


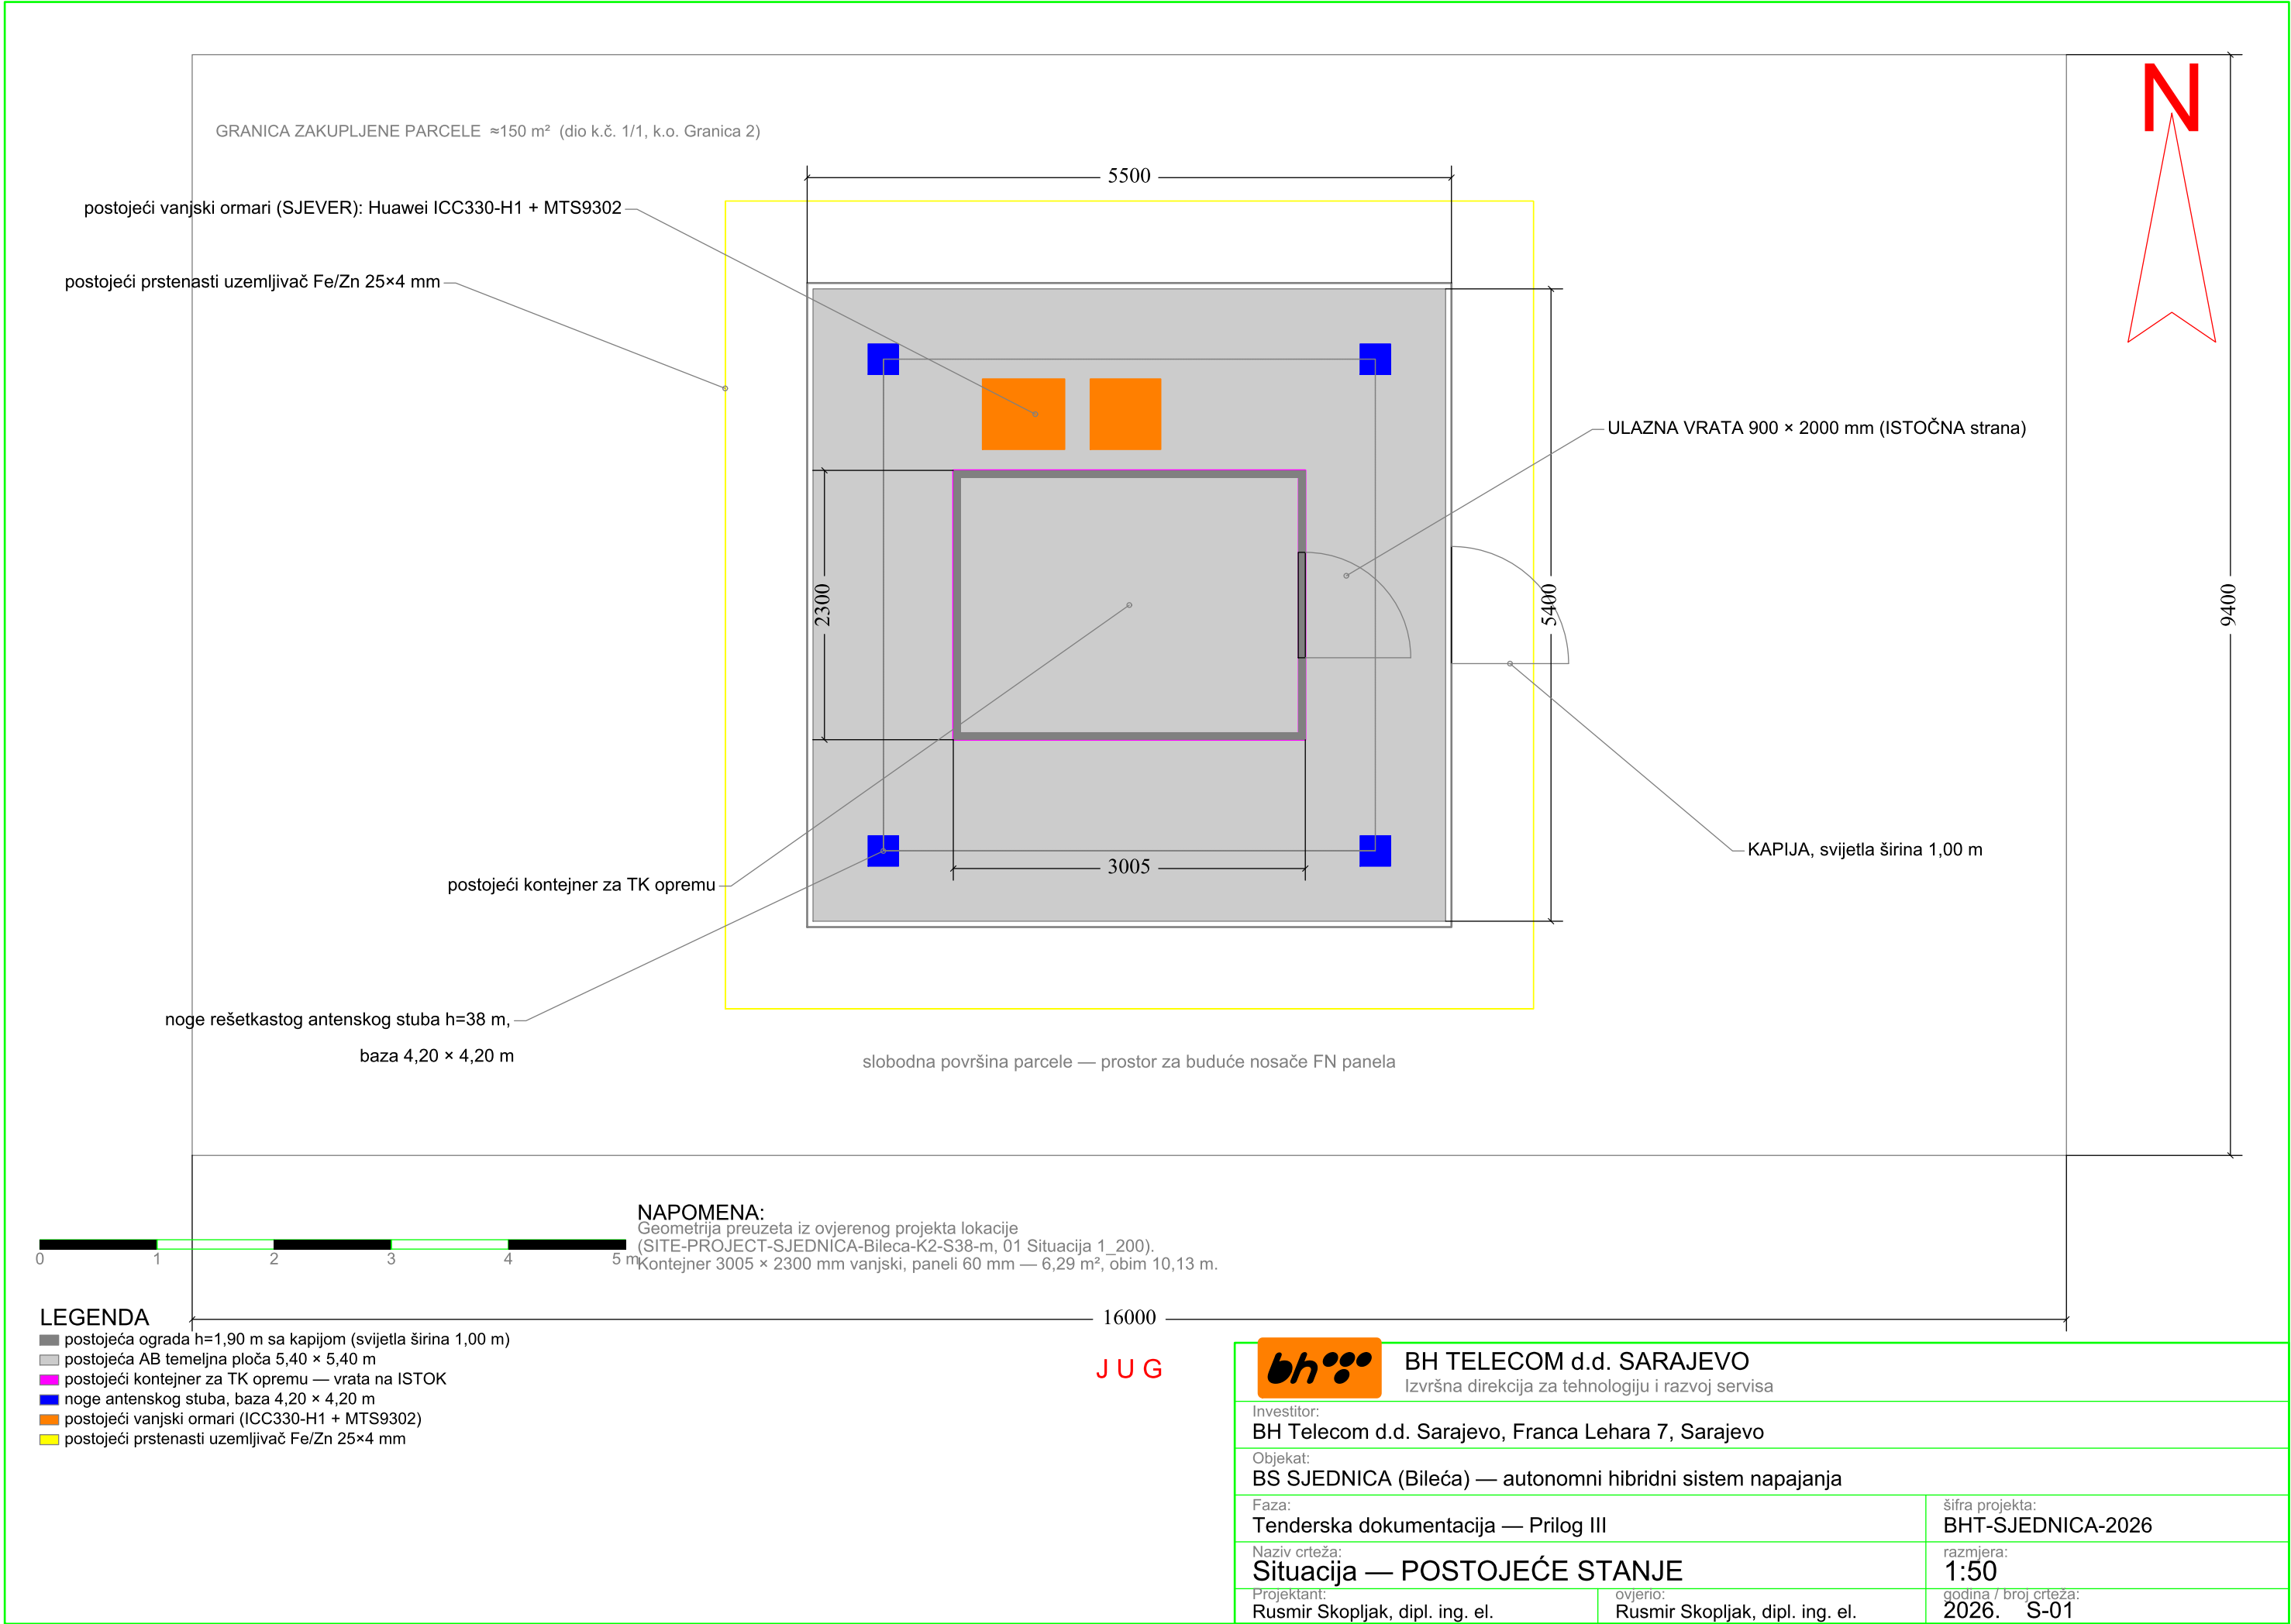


BH TELECOM d.d. SARAJEVO Izvršna direkcija za tehnologiju i razvoj servisa		
Investitor: BH Telecom d.d. Sarajevo, Franca Lehara 7, Sarajevo		
Objekat: BS SJEDNICA (Bileća) — autonomni hibridni sistem napajanja		
Faza: Tenderska dokumentacija — Prilog III		šifra projekta: BHT-SJEDNICA-2026
Naziv crteža: Situacija — POSTOJEĆE STANJE		razmjera: 1:50
Projektant: Rusmir Skopljak, dipl. ing. el.	ovjerio: Rusmir Skopljak, dipl. ing. el.	godina / broj crteža: 2026. S-01

GRANICA ZAKUPLJENE PARCELE ≈150 m² (dio k.č. 1/1, k.o. Granica 2)

kanal + žaluzina 600 × 600, izduv DN 65 iznad krova — ZAPADNI zid; ventilator 1200 m³/h — ISTOČNI zid



9400

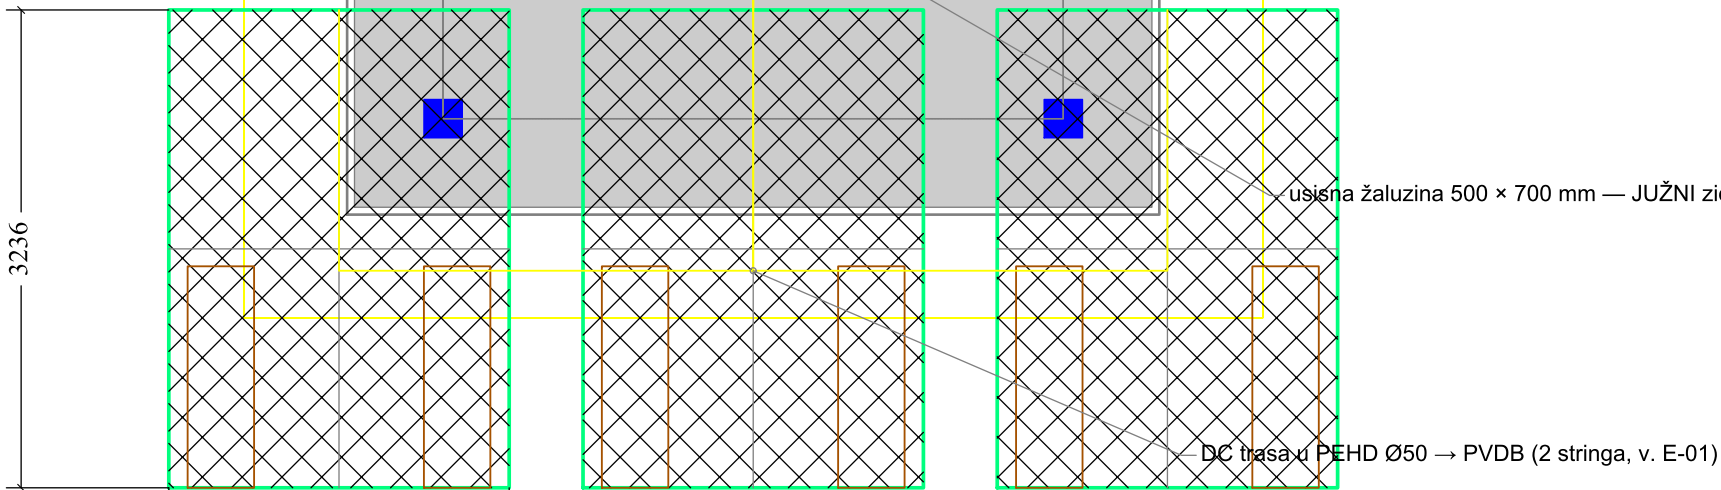

usisna žaluzina 500 × 700 mm — JUŽNI zid

DC trasa u PEHD Ø50 → PVDB (2 stringa, v. E-01)

PV-1 · 4 × 585 Wp · 45° JUG

PV-2 · 4 × 585 Wp · 45° JUG

PV-3 · 4 × 585 Wp · 45° JUG

2 temeljne trake po nosaču (×3), 450 × 3300, razmak 1600 — IZVAN ograde

4 5 m

2305

16000

LEGENDA

- LOT 1 — nosači FN panela PV-1..PV-3 (po 4 × 585 Wp, 45°, JUG) — 2 stringa × 6
- LOT 1 — AB temeljne trake 450 × 3300 mm, razmak 1600 mm
- LOT 1 — DC trasa u PEHD Ø50 do PVDB
- LOT 2 — DEA 22 kVA u skid izvedbi i spremnik 500 l
- LOT 2 — usisna žaluzina (JUG); kanal, žaluzina i izduv (ZAPAD); ventilator (ISTOK)

NAPOMENA — PRORAČUNSKO OPTEREĆENJE:

Vjetar $q_p \geq 1,20 \text{ kN/m}^2$ (udar 3 s ≈ 45 m/s) — iznad kapaciteta kataloškog nosača tipa A, stoga CUSTOM IZRADA: sail 10,55 m²/nosaču, ULS uzgon 18,1 kN, moment prevrtanja 62,8 kNm; ovjerava ponuđač (Prilog II, 1.3).
Temelji IZVAN ograde (400 mm od kote ograde); gornja ivica panela +4,23 m, 2836 mm iznad ograde. Kontejner je PRAZAN.



BH TELECOM d.d. SARAJEVO

Izvršna direkcija za tehnologiju i razvoj servisa

Investitor:

BH Telecom d.d. Sarajevo, Franca Lehara 7, Sarajevo

Objekat:

BS SJEDNICA (Bileća) — autonomni hibridni sistem napajanja

Faza:

Tenderska dokumentacija — Prilog III

Naziv crteža:

Situacija — BUDUĆE STANJE (LOT 1 + LOT 2)

Projektant:

Rusmir Skopljak, dipl. ing. el.

ovjerio:

Rusmir Skopljak, dipl. ing. el.

šifra projekta:


BHT-SJEDNICA-2026

razmjera:

1:50

godina / broj crteža:

2026. S-02

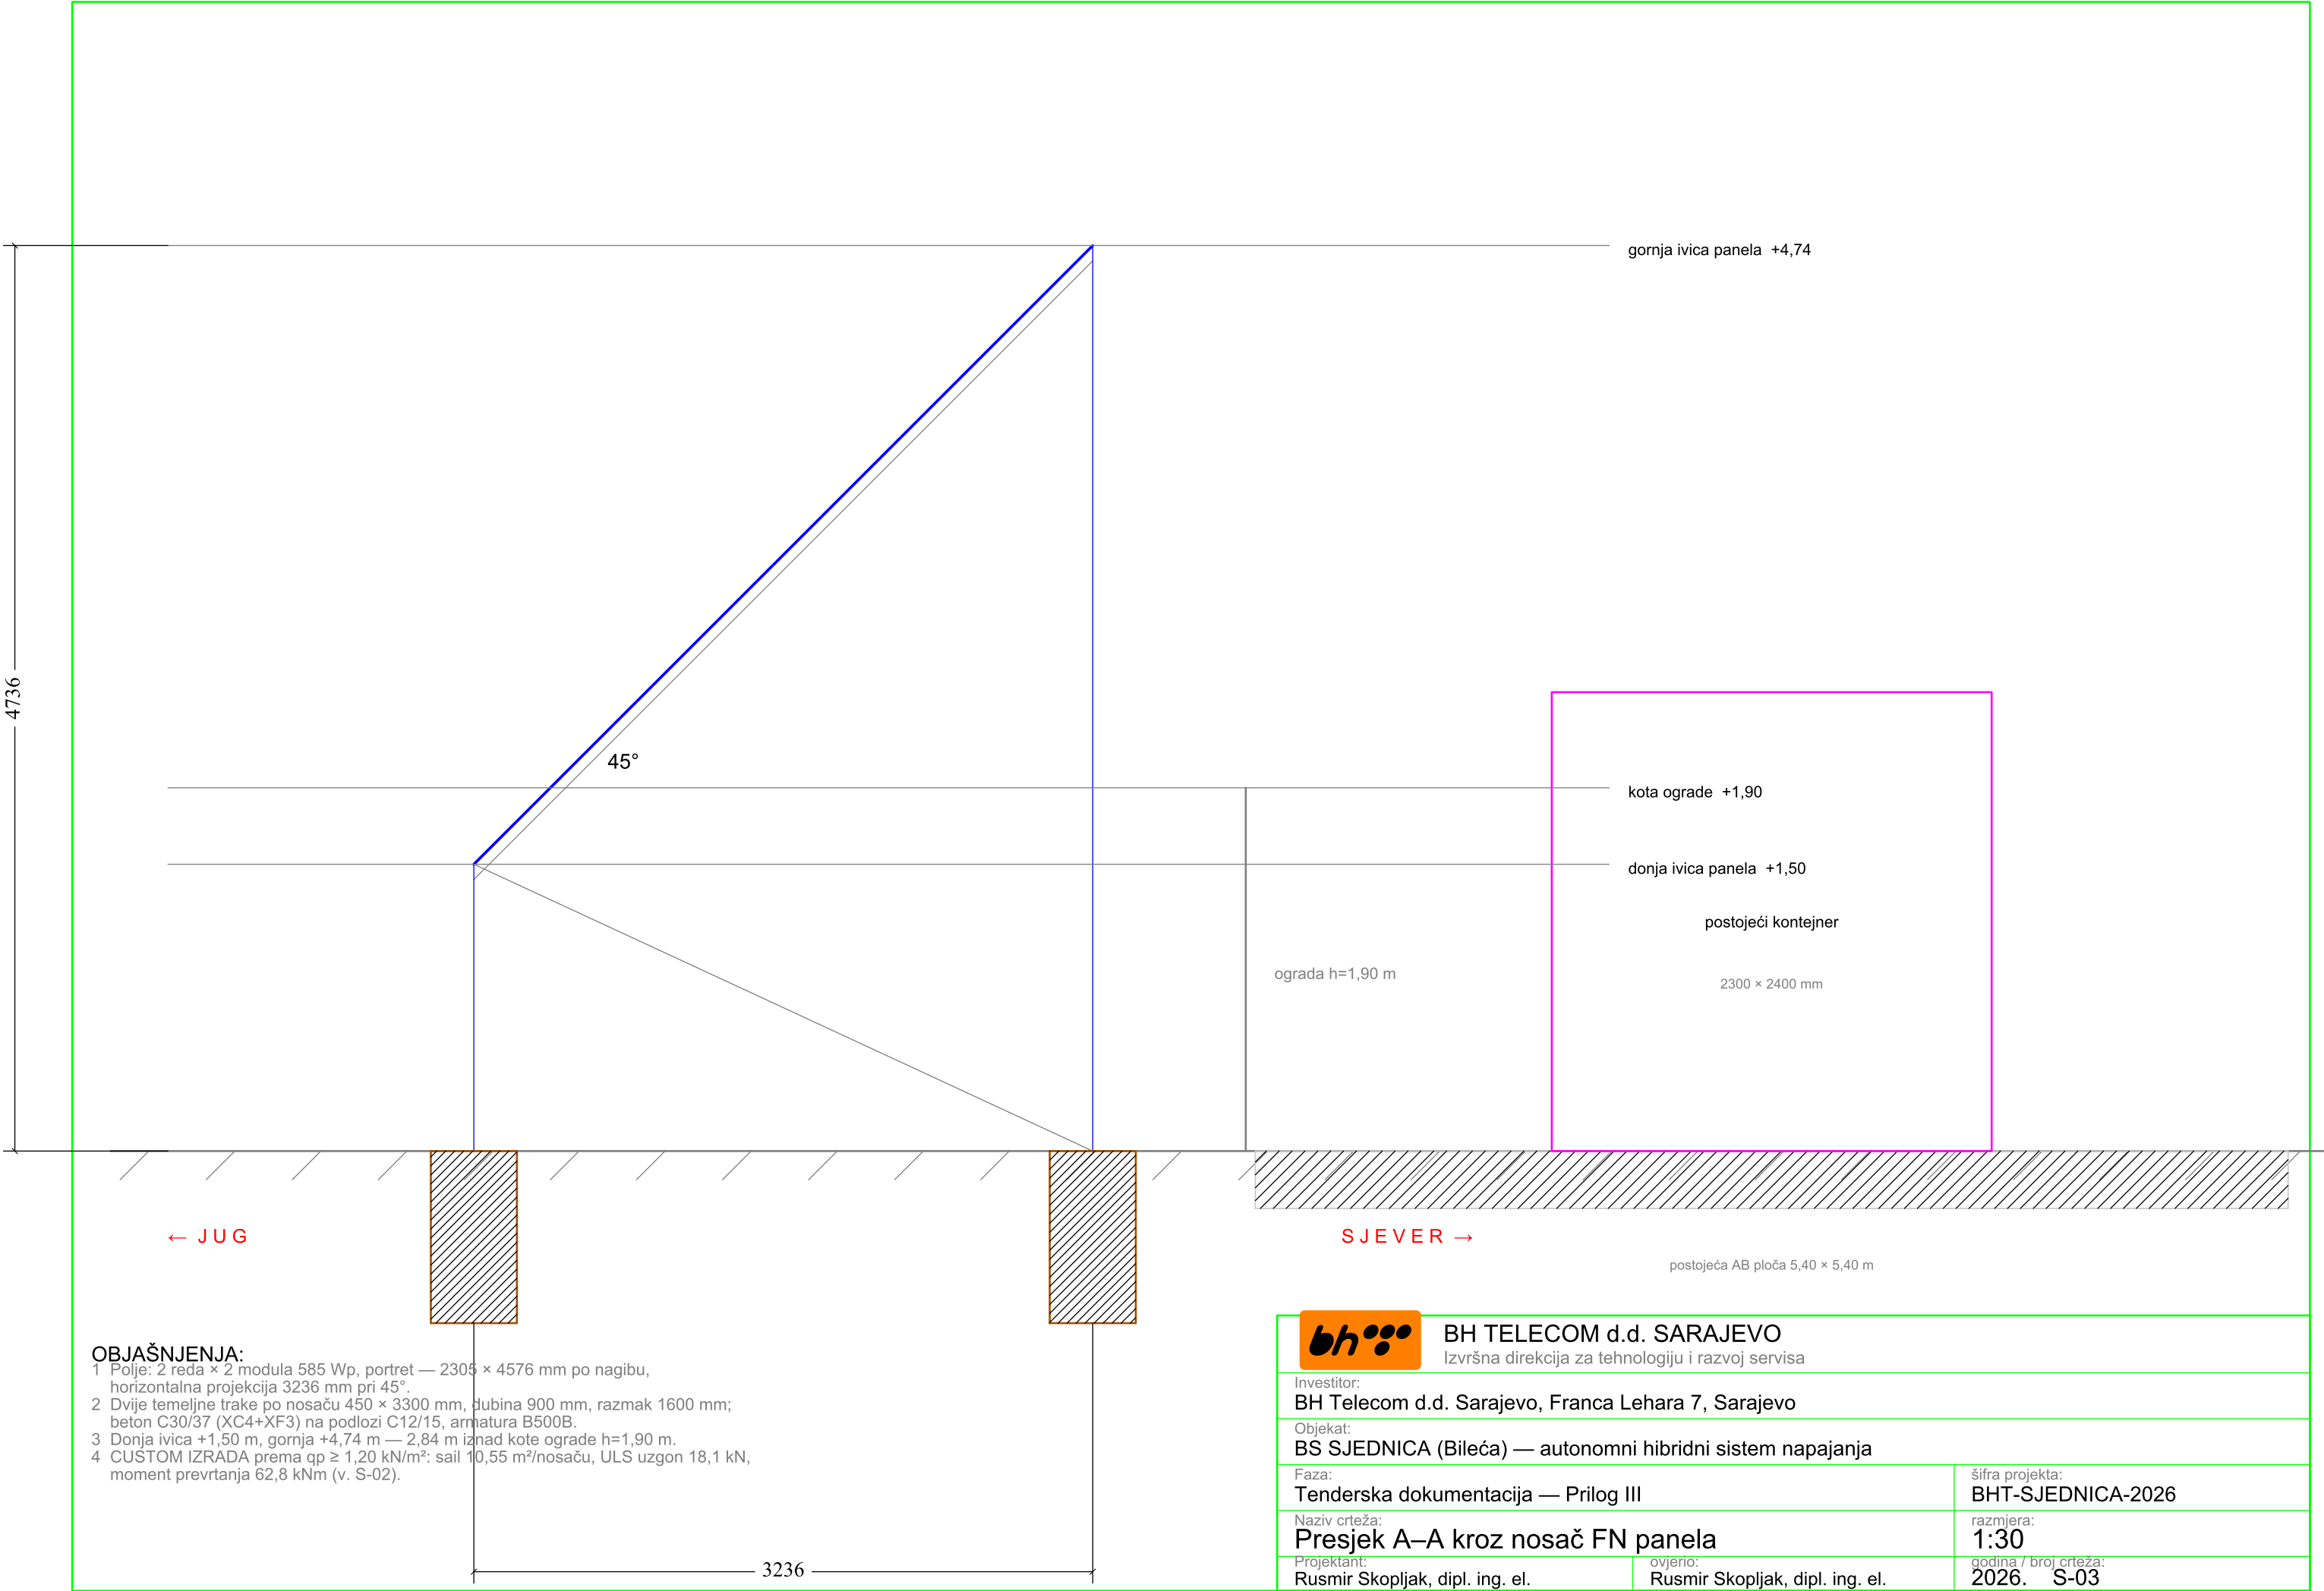

OBJAŠNJENJA:

- Polje: 2 reda x 2 modula 585 Wp, portret — 2303 x 4576 mm po nagibu, horizontalna projekcija 3236 mm pri 45°.
- Dvije temeljne trake po nosaču 450 x 3300 mm, dubina 900 mm, razmak 1600 mm; beton C30/37 (XC4+XF3) na podlozi C12/15, armatura B500B.
- Donja ivica +1,50 m, gornja +4,74 m — 2,84 m iznad kote ograde h=1,90 m.
- CUSTOM IZRADA prema qp ≥ 1,20 kN/m²: sail 10,55 m²/nosaču, ULS uzgon 18,1 kN, moment prevrtanja 62,8 kNm (v. S-02).



BH TELECOM d.d. SARAJEVO

Izvršna direkcija za tehnologiju i razvoj servisa

Investitor:

BH Telecom d.d. Sarajevo, Franca Lehara 7, Sarajevo

Objekat:

BS SJEDNICA (Bileća) — autonomni hibridni sistem napajanja

Faza:

Tenderska dokumentacija — Prilog III

Naziv crteža:

Presjek A–A kroz nosač FN panela

Projektant:

Rusmir Skopljak, dipl. ing. el.

ovjerio:

Rusmir Skopljak, dipl. ing. el.

šifra projekta:

BHT-SJEDNICA-2026

razmjera:

1:30

godina / broj crteža:

2026. S-03



- OPOMENE:**
- 1 FG Wilson P22-6 (Skid), TL 2019-08-14: hladnjak 1980 m³/h, sagorijevanje 90 m³/h, toplota u prostor 7,1 kW, maks. vanjski otpor 125 Pa.
 - 2 Žaluzine zadovoljavaju: usis 500 × 700 (Δp≈16 Pa) + izlaz 600 × 600 (≈15 Pa) + kanal < 125 Pa.
 - 3 Ventilator 1200 m³/h je DOPUNSKA ventilacija (min. 120 m³/h); protok hlađenja daje ventilator hladnjaka.
 - 4 Izduv DN 65 usvojen (NO 50 zadovoljava protutlak, ali radi pri 33 m/s).
 - 5 Pod je dimensionisan na 10,00 kN/m² ravnomjerno raspodijeljeno (projekat lokacije, 4.4.2.3). Agregat 3,93 i pun spremnik 9,2 kN/m² su KONCENTRISANI — roštilj za raznošenje je OBAVEZAN.
 - 6 RASPORED: usis JUG (+0,30), kanal/izlaz i izduv ZAPAD, oduška SJEVER, ventilator ISTOK; ≥3 m između usisa, izduva i oduška. Ništa ne izbacuje prema omarima na SJEVERU.
 - 7 UNOS: skid 620 mm kroz vrata 900 mm. Kontejner je PRAZAN.

