



BH TELECOM d.d. SARAJEVO

Izvršna direkcija za tehnologiju i razvoj servisa

TENDERSKA DOKUMENTACIJA ZA NABAVKU

INFRASTRUKTURA I INSTALACIJA OPREME ZA AUTONOMNI HIBRIDNI SISTEM NAPAJANJA SJEDNICA, BILEĆA (LOT 1 i 2)

PROVOĐENJEM NABAVKE PUTEM PREGOVARAČKOG POSTUPKA NABAVKE SA OBJAVOM
OBAVJEŠTENJA

PRILOG III

SITUACIJA, DISPOZICIJA OPREME I GRAFIČKI PRILOZI (NACRTI)

Lokacija: BS Sjednica, Bileća, BiH

Koordinate: 42,9448° N · 18,3236° E · 1076 m n.v.

Sarajevo, august 2026. godine



BH TELECOM d.d. SARAJEVO | BS SJEDNICA (BILEĆA) | PRILOG III

Fotografija postojećeg stanja lokacije


Antenski stub, kontejner, ograda — stanje prije izvođenja radova


**Crtež br.
INFO-01**


1. OPŠTI PODACI O LOKACIJI

Investitor	BH Telecom d.d. Sarajevo, Franca Lehara 7, 71000 Sarajevo
Objekat	Bazna stanica SJEDNICA
Općina	Bileća
Koordinate	42,9448° N, 18,3236° E
Nadmorska visina	1076 m
Zakupljena površina	≈150 m² (dio k.č. 1/1, k.o. Granica 2)
Betonski temelj	5,40 × 5,40 m, sa metalnom ogradom visine 2,10 m
Antenski stub	Rešetkasta izvedba, visina 38 m; baza 4,20 m (dno) / 1,20 m (vrh)
Kontejner	Vanjske dimenzije 3,005 × 2,30 m, zidni paneli 60 mm; IP55, prema ovjerenom projektu lokacije; PRAZAN
Priključak na EES	NE — lokacija nije priključena na elektroenergetsku mrežu
TK oprema	Huawei RRU (3 kom) + BBU/MPLS, -48 VDC
Snaga potrošača	1.180 W nazivno / 1.330 W maksimalno (sa hlađenjem)
Sistem napajanja	Hibridni: FN moduli (primarni) + LFP baterije + DEA (rezervni)
FN konfiguracija	12 × iPV585-M2A (7,02 kWp), fiksni nagib 45°, azimut 180° (jug); monofacijalni iPV moduli sa optimizatorima
DEA	18 kVA / 14,4 kW stand-by (ISO 8528-3), rad u prime režimu, ulaz ispravljača ograničen na 9,5 kW; skid izvedba u kontejneru
Spremnik goriva	Dvoplašni, 500 l, sa nivo sondom i detekcijom curenja
Očekivani rad DEA	≈250 h/god (9 od 10 godina ≤310 h), gorivo ≈820 l/god — simulacija pvsim, uz parametrisiranje SMU iz Priloga I, Tačka 4.6

Napomena: podaci preuzeti iz RFI dokumenta „Autonomno napajanje za BS“ od 27.04.2026. godine i Projektnog zadatka za hibridno napajanje BS Sjednica. Konstruktivni podaci kontejnera preuzeti iz Projektnog zadatka za tipsku prenosivu kućicu — kontejner (opterećenje poda 10,00 kN/m², snijeg 3,00 kN/m², vjetar 1,10 kN/m²). DEA kao FG Wilson P18-6 (Skid) (motor Perkins 404D-22G1) ili ekvivalent.

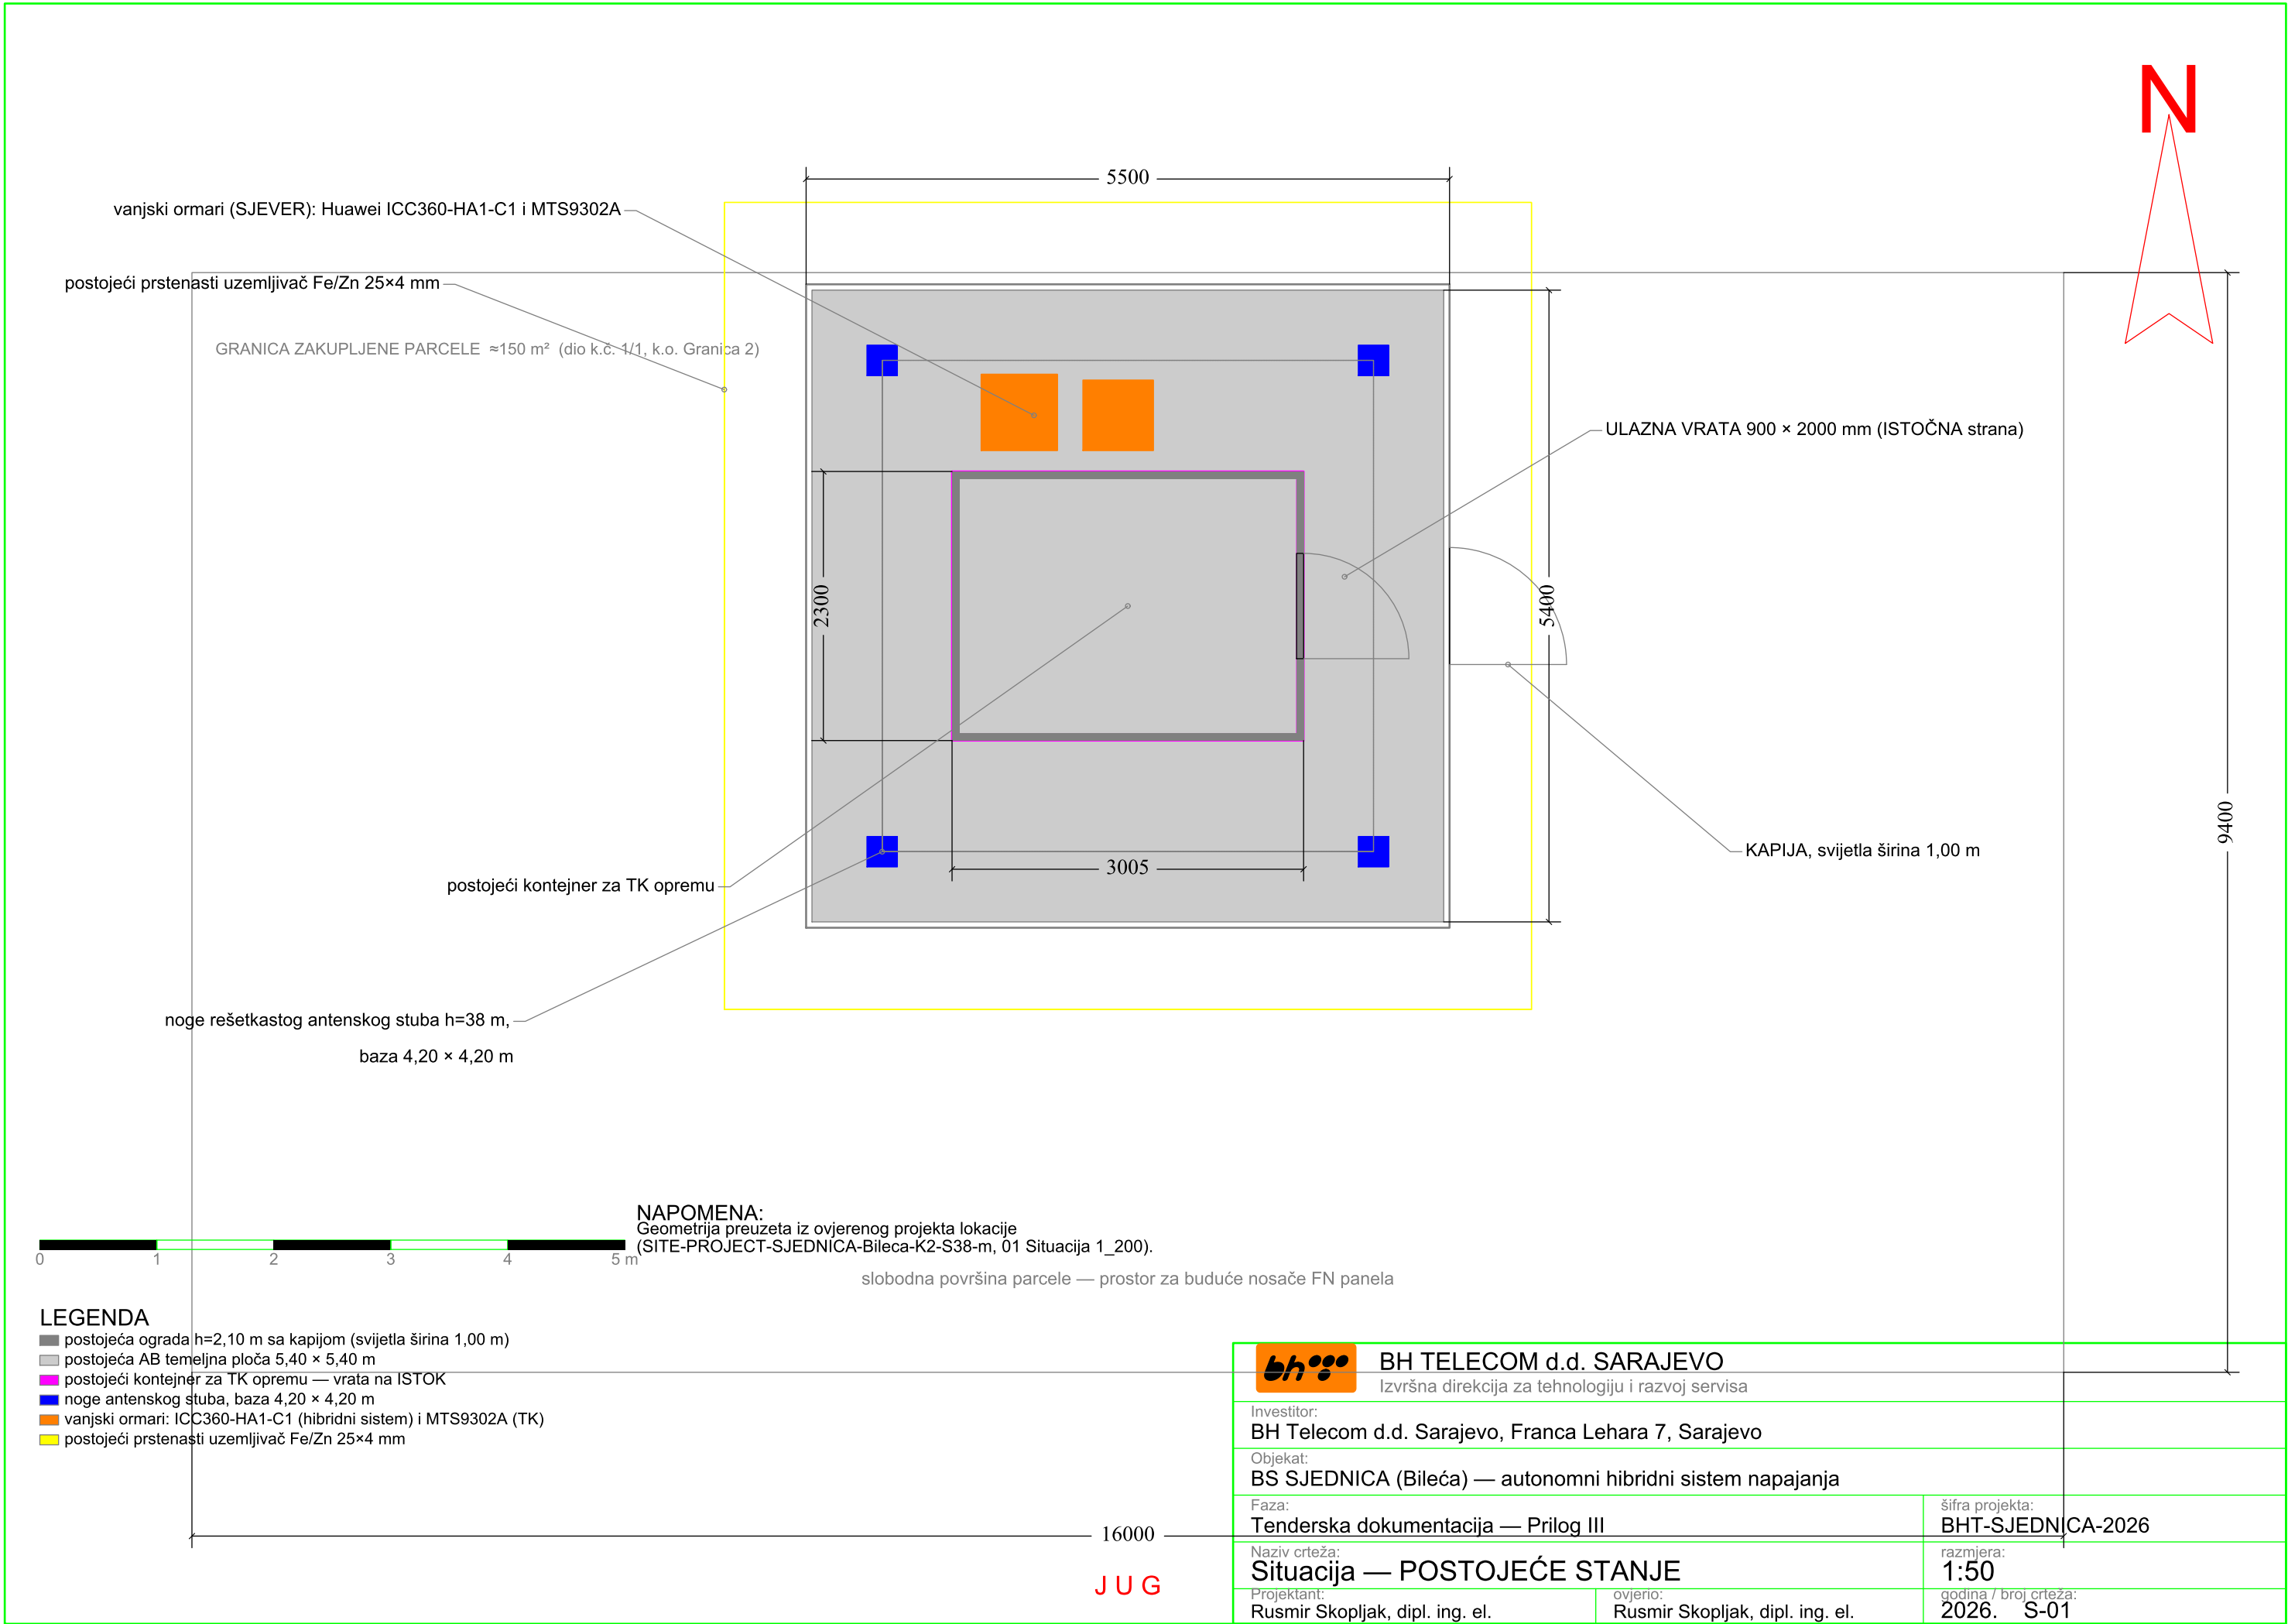

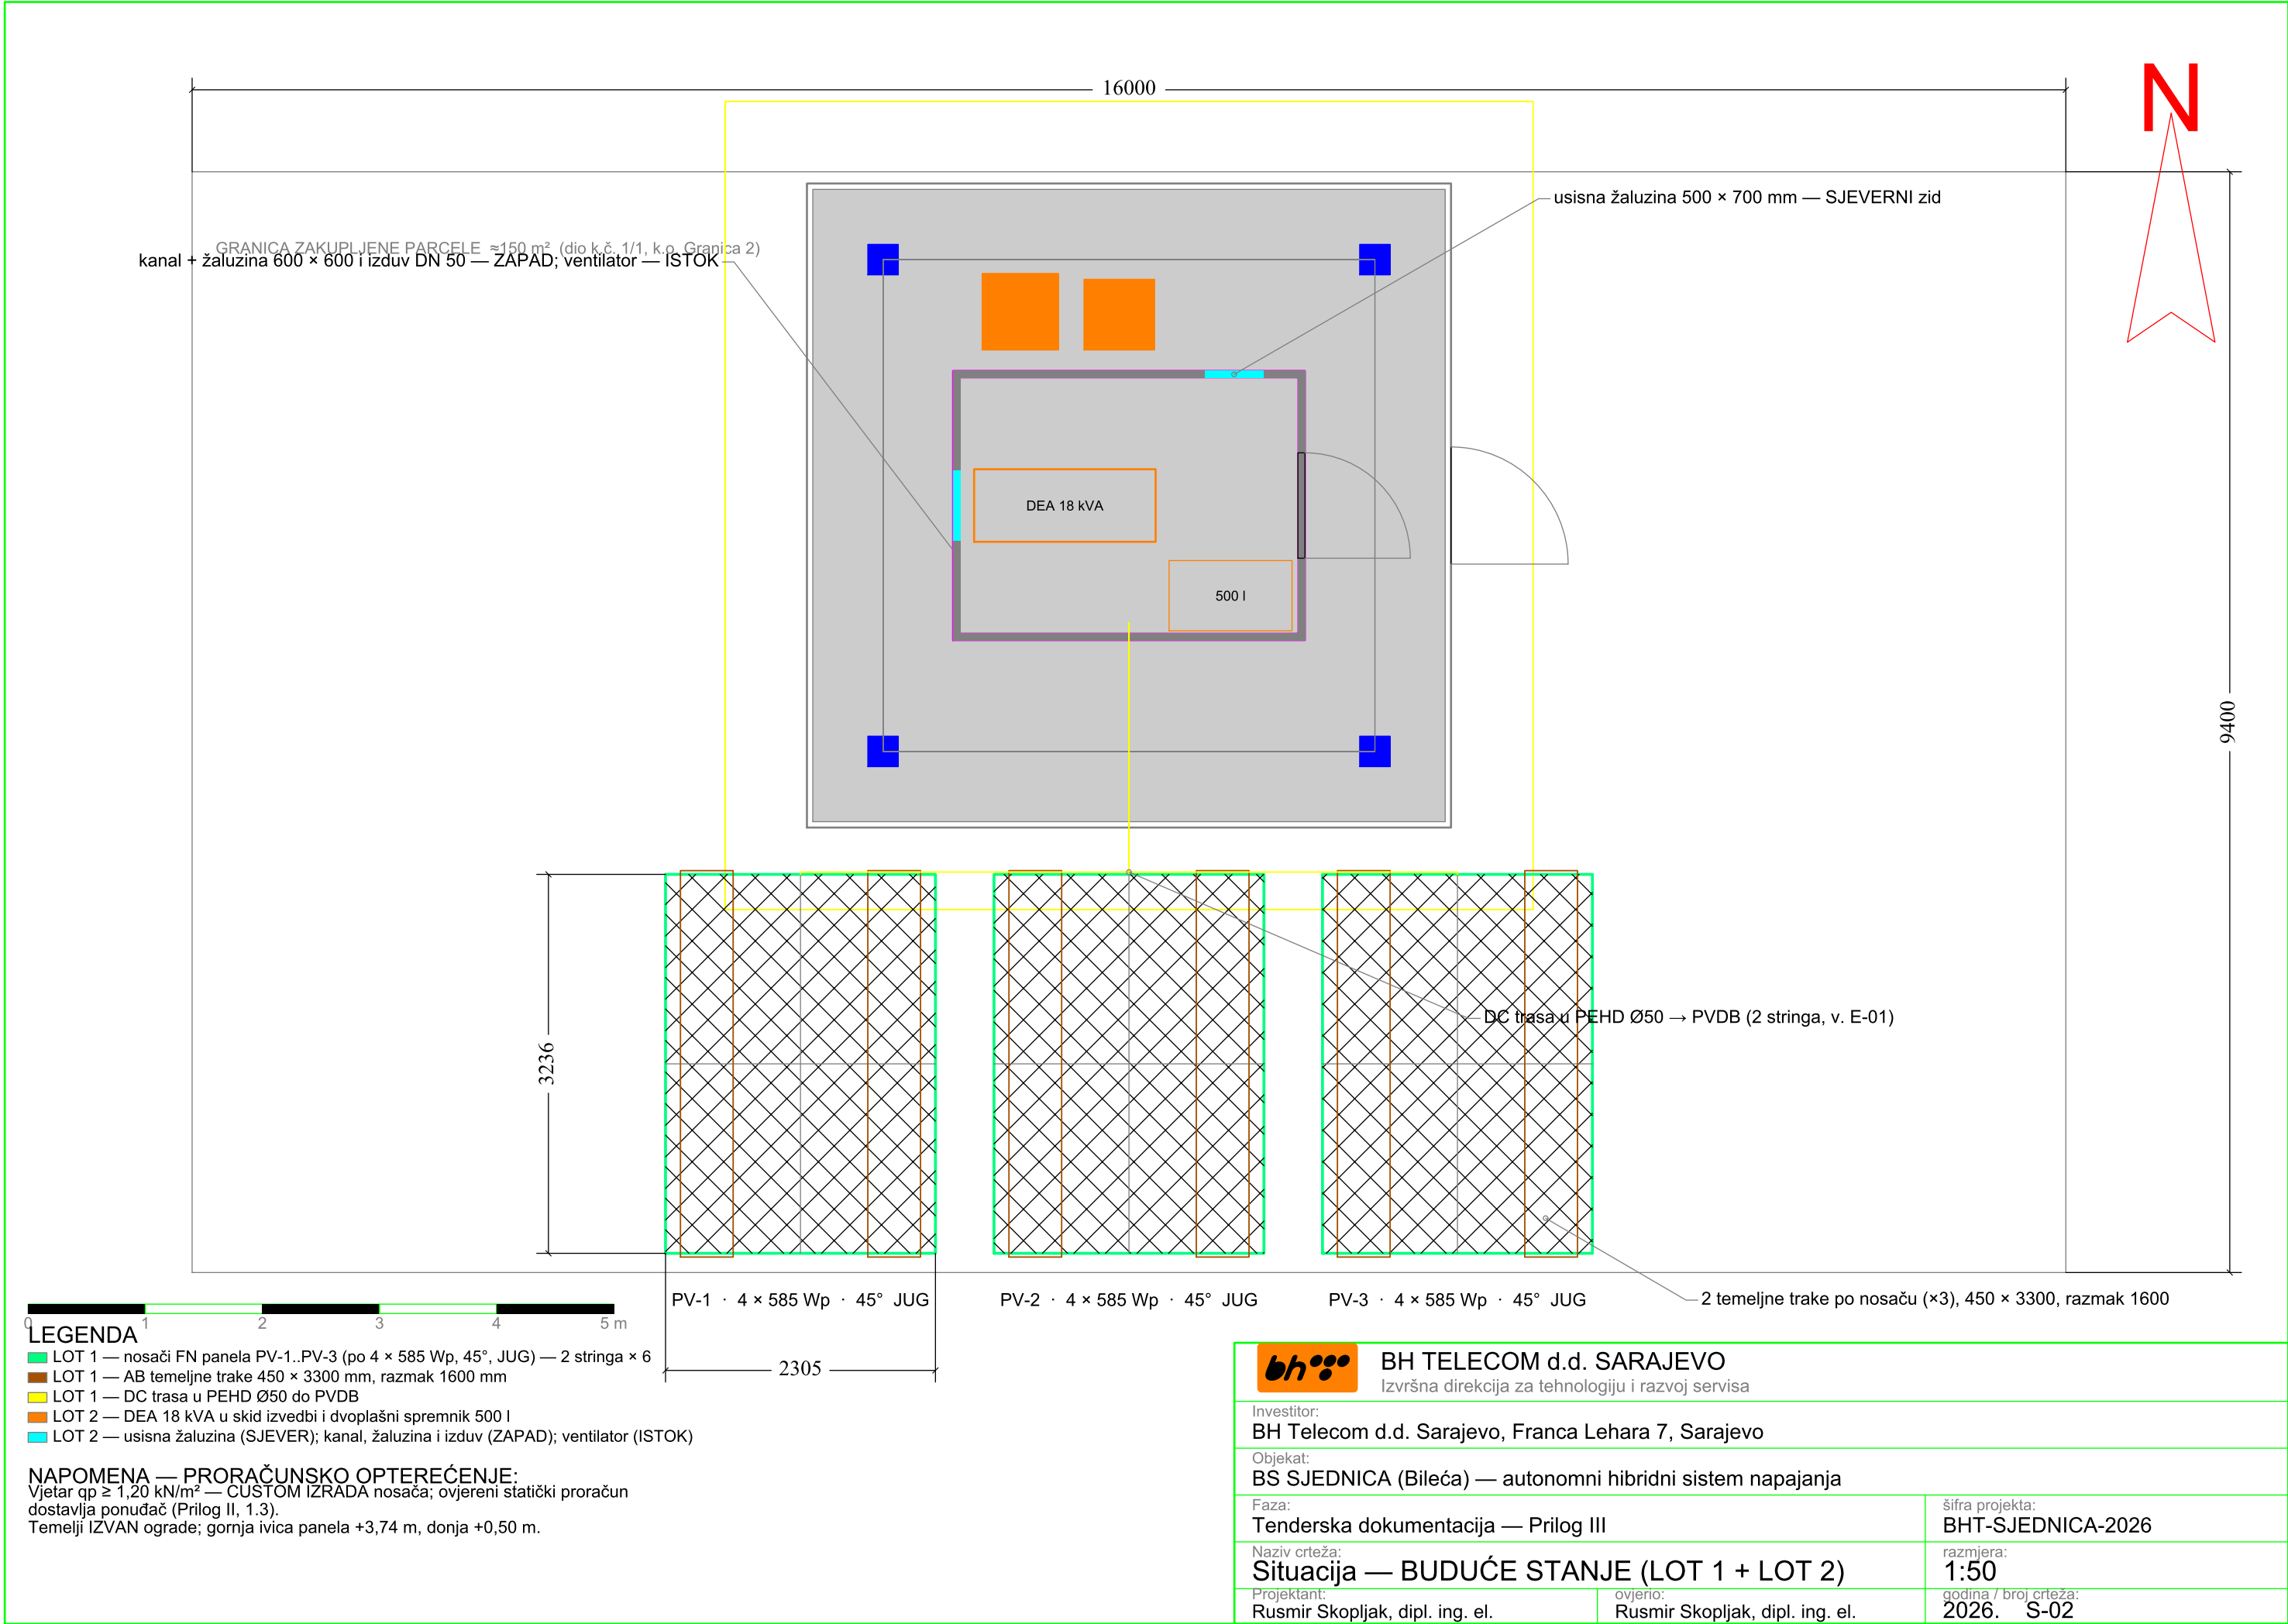

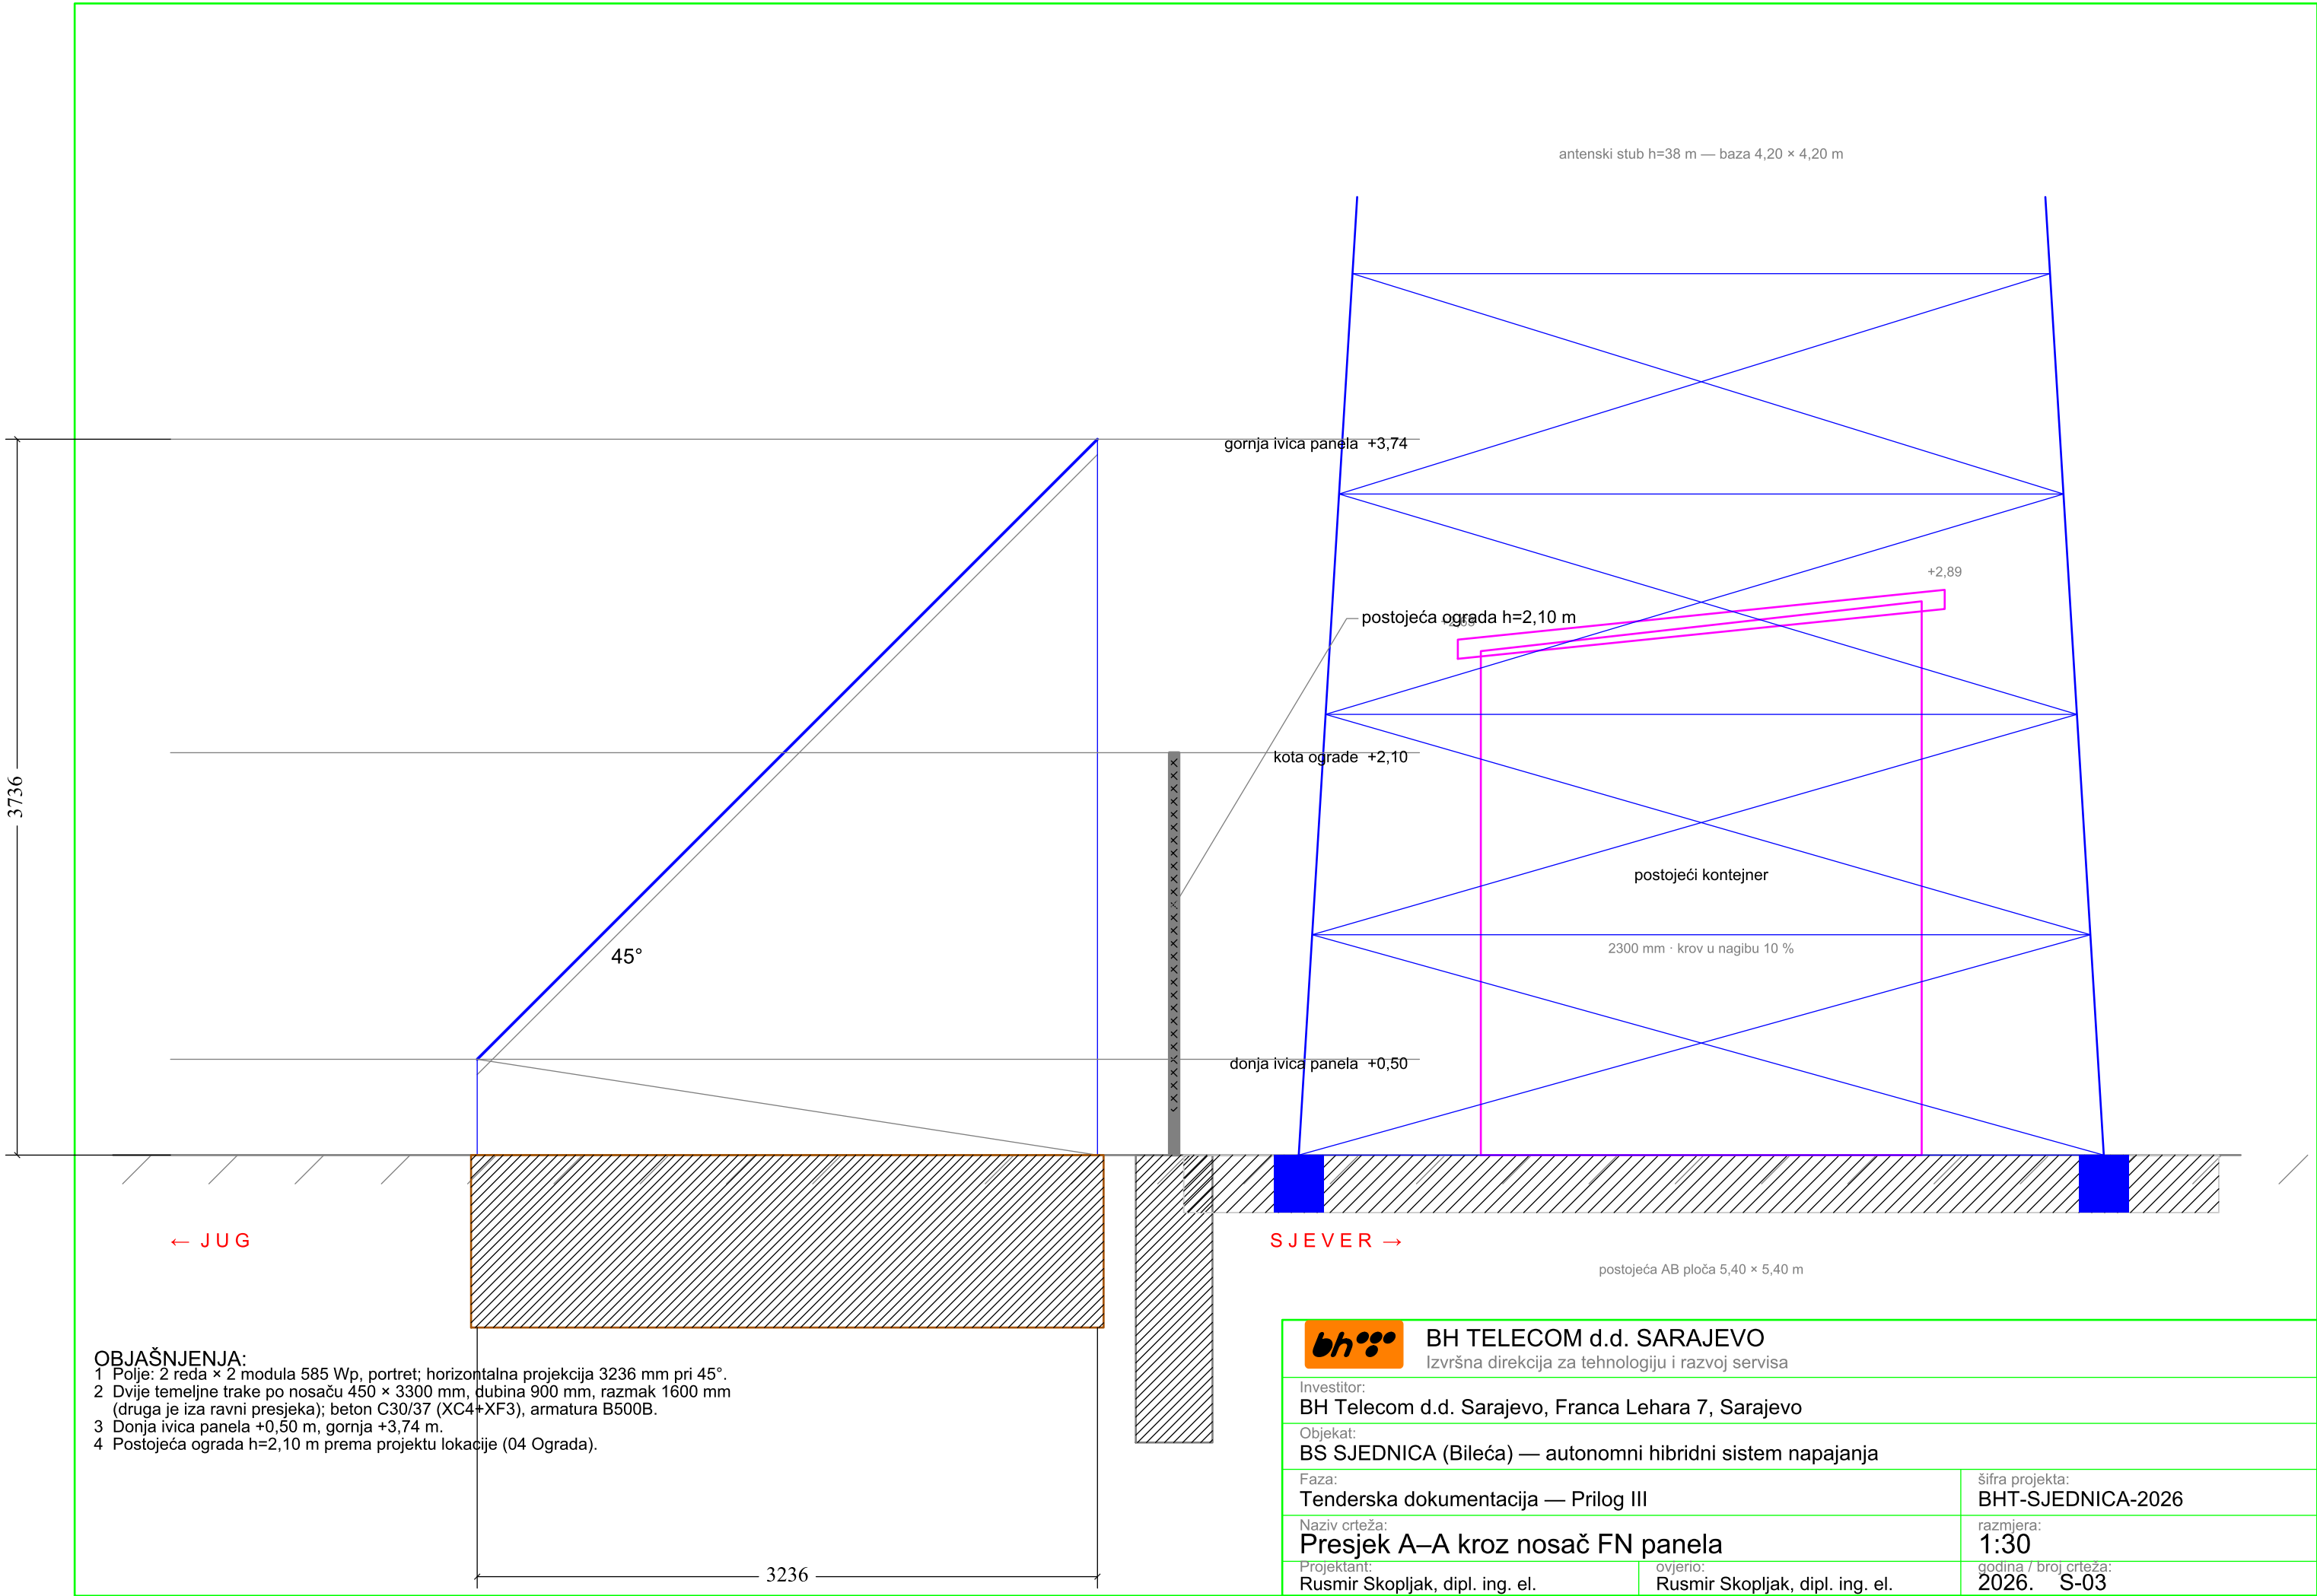

OBJAŠNJENJA:

- 1 Polje: 2 reda × 2 modula 585 Wp, portret; horizontalna projekcija 3236 mm pri 45°.
- 2 Dvije temeljne trake po nosaču 450 × 3300 mm, dubina 900 mm, razmak 1600 mm (druga je iza ravni presjeka); beton C30/37 (XC4+XF3), armatura B500B.
- 3 Donja ivica panela +0,50 m, gornja +3,74 m.
- 4 Postojeća ograda h=2,10 m prema projektu lokacije (04 Ograda).



BH TELECOM d.d. SARAJEVO

Izvršna direkcija za tehnologiju i razvoj servisa

Investitor:

BH Telecom d.d. Sarajevo, Franca Lehara 7, Sarajevo

Objekat:

BS SJEDNICA (Bileća) — autonomni hibridni sistem napajanja

Faza:

Tenderska dokumentacija — Prilog III

Naziv crteža:

Presjek A–A kroz nosač FN panela

Projektant:

Rusmir Skopljak, dipl. ing. el.

ovjerio:

Rusmir Skopljak, dipl. ing. el.

šifra projekta:


BHT-SJEDNICA-2026

razmjera:

1:30


godina / broj crteža:

2026. S-03

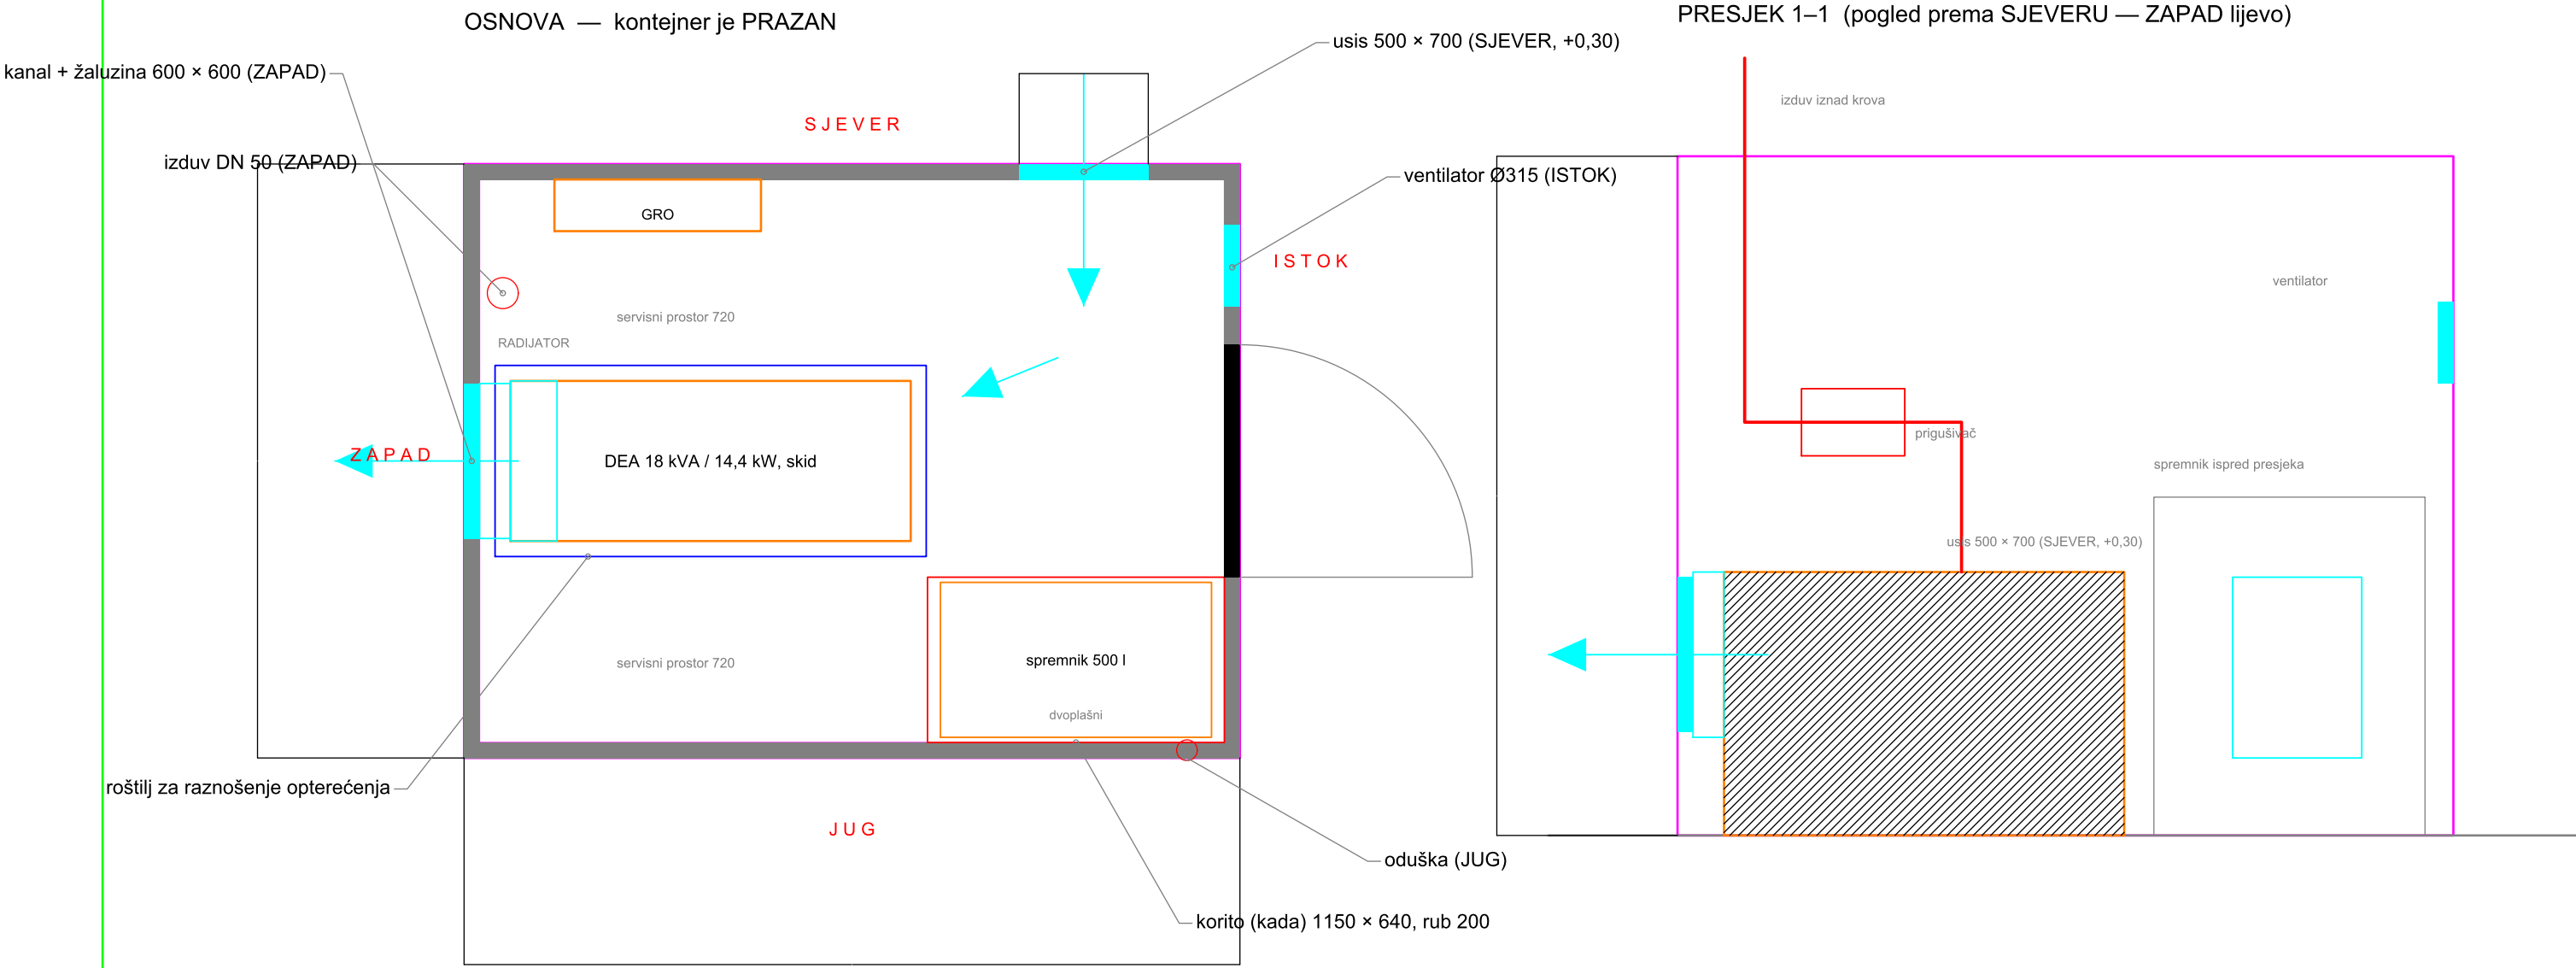

- NAPOMENE:
- 1 Agregat FG Wilson P18-6 (Skid) ili ekvivalent, 18 kVA / 14,4 kW.
 - 2 RASPORED (obavezujući): ušis 500 x 700 SJEVER (+0,30); kanal i žaluzina 600 x 600 te izdub DN 50 ZAPAD; oduška JUG; ventilator ISTOK. ≥3 m između usisa, izduva i oduške.
 - 3 Roštilj za raznošenje opterećenja OBAVEZAN ispod skida i ispod korita.
 - 4 Spremnik je DVOPLAŠNI; ispod njega korito (kada) 1150 x 640, rub 200 mm.
 - 5 SERVISNI PROSTOR (obavezujući): 720 mm JUG, 720 mm SJEVER, 1155 mm ISTOK — ne zauzimati opremom ni skladištenjem.
 - 6 Unos skida 620 mm kroz vrata 900 mm. Kontejner je PRAZAN.

BH TELECOM d.d. SARAJEVO Izvršna direkcija za tehnologiju i razvoj servisa		
Investitor: BH Telecom d.d. Sarajevo, Franca Lehara 7, Sarajevo		
Objekat: BS SJEDNICA (Bileća) — autonomni hibridni sistem napajanja		
Faza: Tenderska dokumentacija — Prilog III		šifra projekta: BHT-SJEDNICA-2026
Naziv crteža: DEA u postojećem kontejneru — osnova i presjek		razmjera: 1:25
Projektnant: Rusmir Skopljak, dipl. ing. el.	ovjerio: Rusmir Skopljak, dipl. ing. el.	godina / broj crteža: 2026. M-01

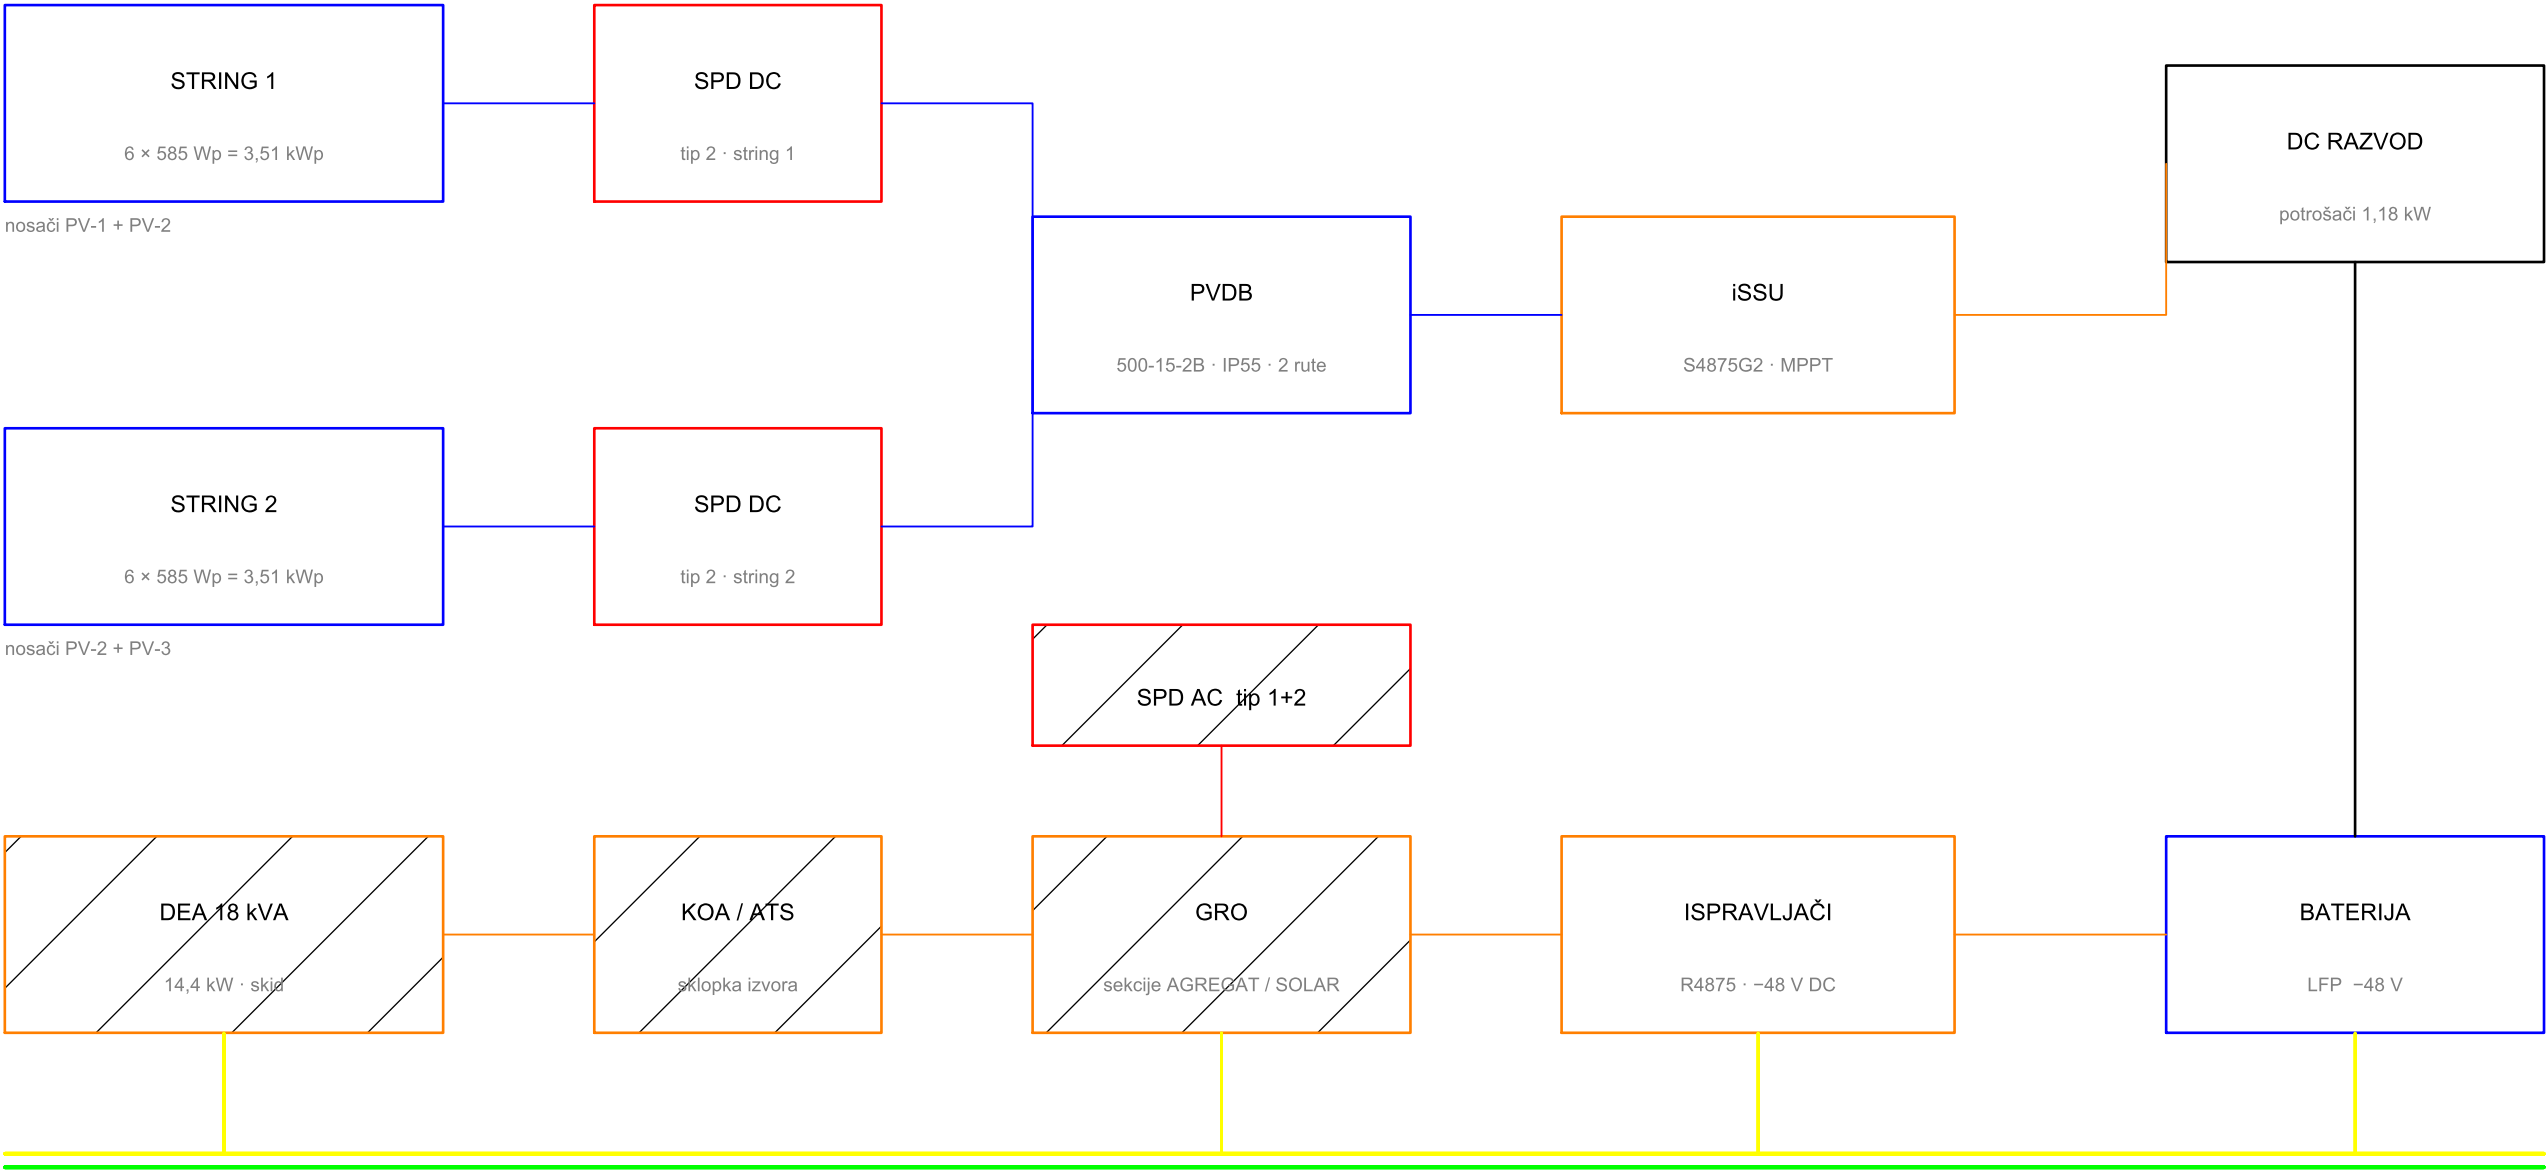

postojeći prstenasti uzemljivač Fe/Zn 25×4 · R ≤ 10 Ω · nosači FN vezani bakrenim užetom 50 mm² preko bimetalnih spojeva

- NAPOMENE:**
- 1 Lokacija NIJE na mreži — DEA je jedini AC izvor; KOA/ATS je sklopka izvora.
 - 2 Uzemljenje TN-S: spoj N-PE samo u novom GRO.
 - 3 Odvodnici: AC tip 1+2, DC tip 2 po stringu, signalni vodovi EN 61643-21.
 - 4 12 modula = 2 stringa × 6; PVDB ima 2 rute.

 isporuka i montaža — LOT 2



BH TELECOM d.d. SARAJEVO
Izvršna direkcija za tehnologiju i razvoj servisa

Investitor:
BH Telecom d.d. Sarajevo, Franca Lehara 7, Sarajevo

Objekat:
BS SJEDNICA (Bileća) — autonomni hibridni sistem napajanja

Faza:
Tenderska dokumentacija — Prilog III

Naziv crteža:
Jednopolna shema — hibridni sistem napajanja


Projektant:
Rusmir Skopljak, dipl. ing. el.

ovjerio:
Rusmir Skopljak, dipl. ing. el.


šifra projekta:
BHT-SJEDNICA-2026

razmjera:
—


godina / broj crteža:
2026. E-01

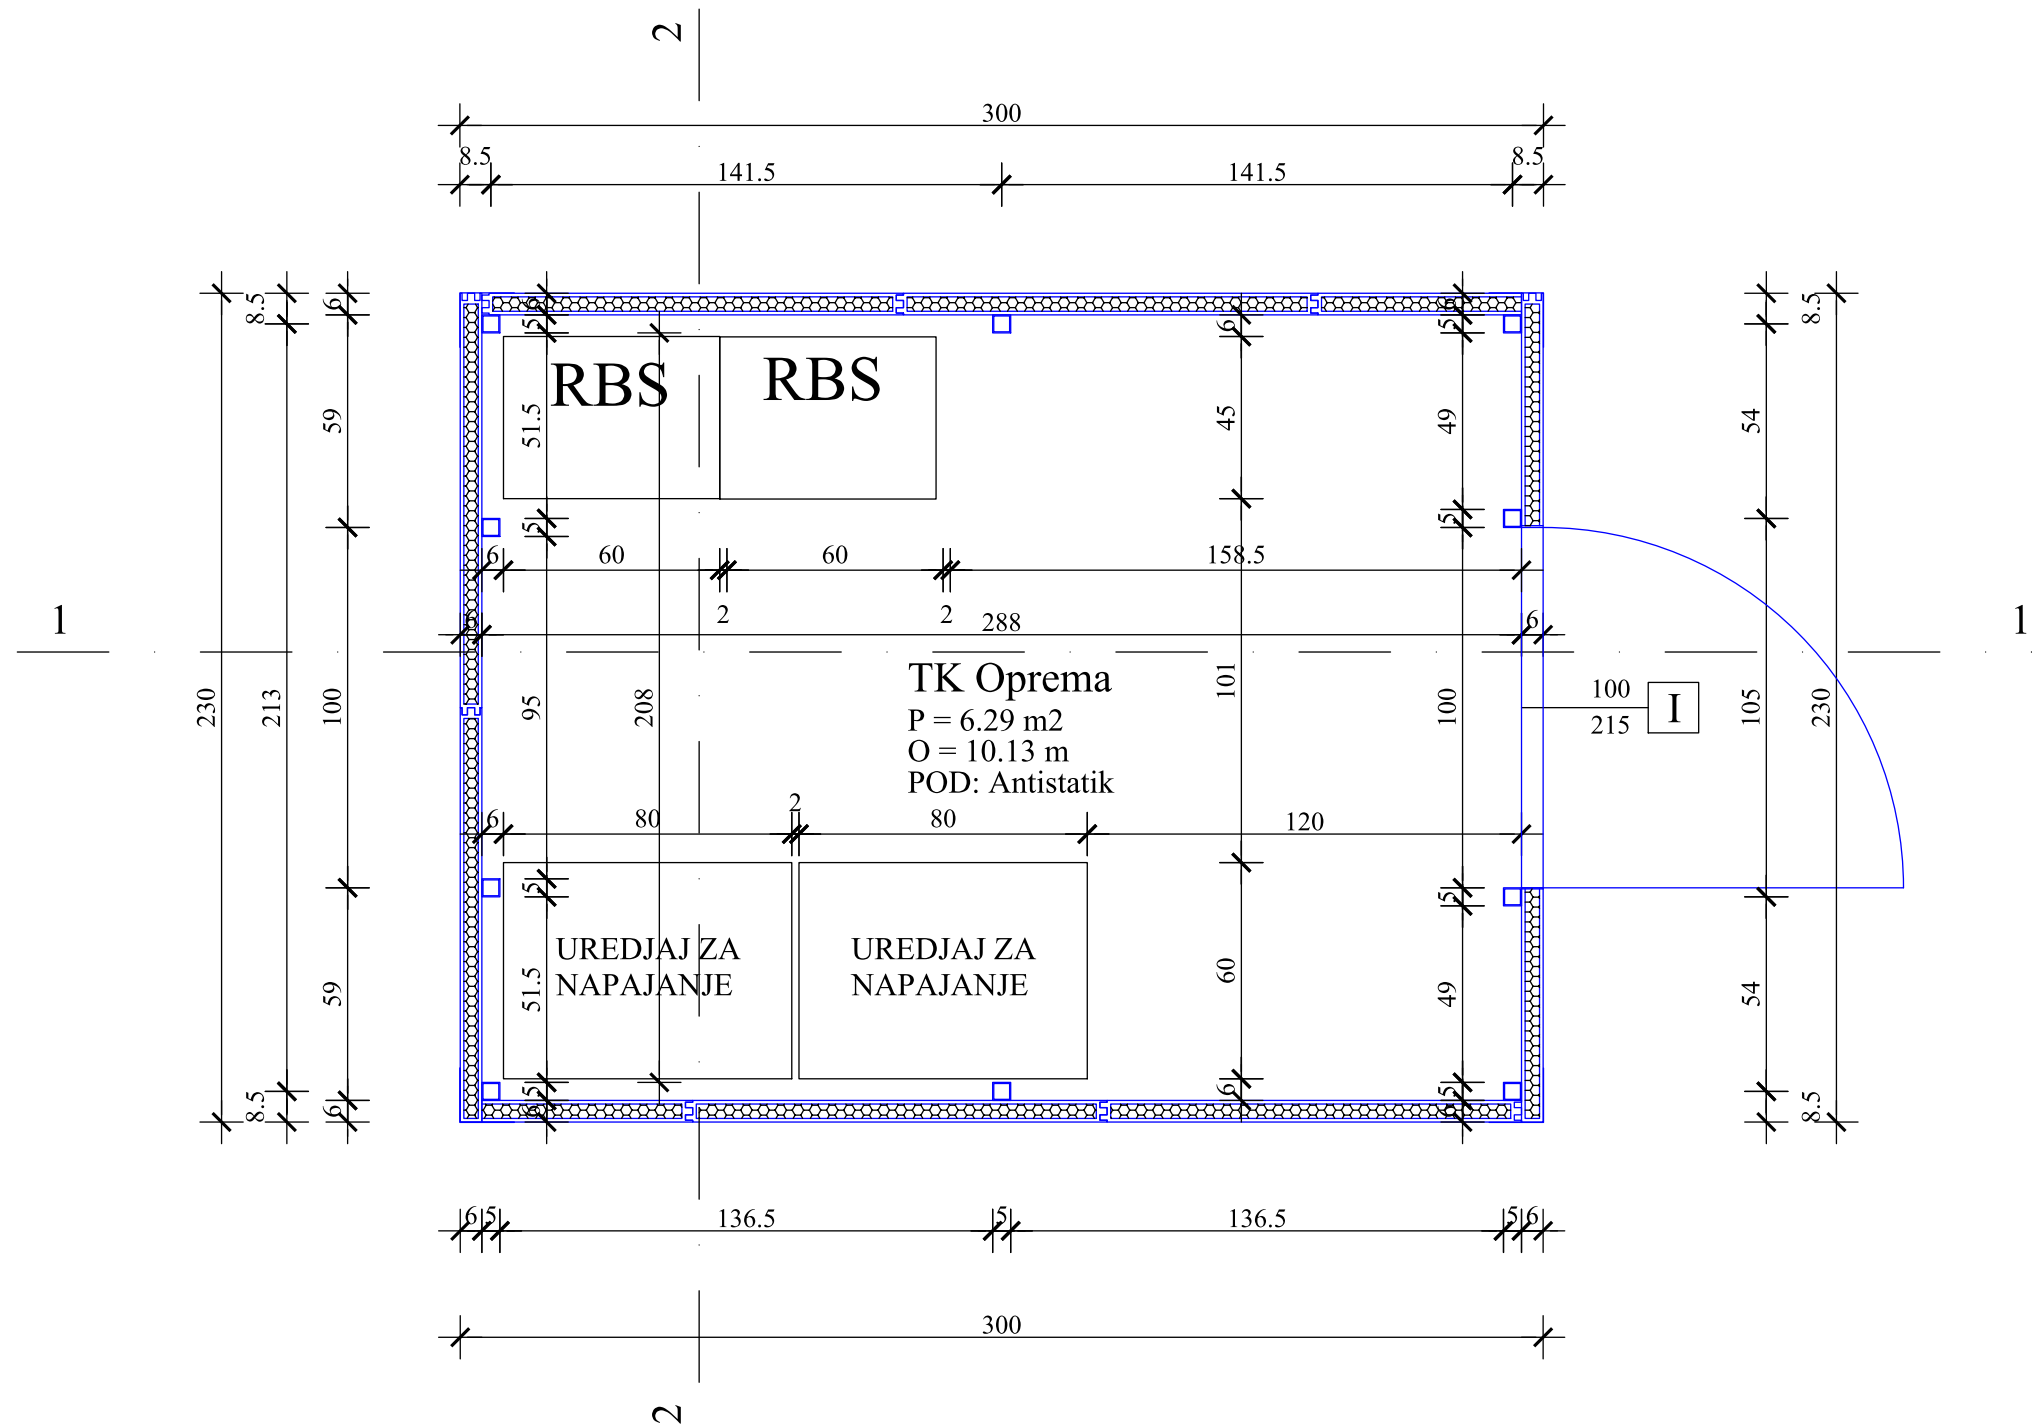





Investitor: BH TELECOM d.d.		Objekat: Infrastruktura bazne stanice mobilne telefonije		bhtelecom Dioničko društvo Sarajevo
Glavni projekat Knjiga 1/1	Faza: A	godina: 2018.	šifra projekta: GP-BS-10472-326	
Naziv crteža: Osnova objekta za smještaj opreme		razmjera: 1:50	broj crteža: 1 - (148/177)	ovjerio: Projektant:Dženadin Mušinović,d.i.g.

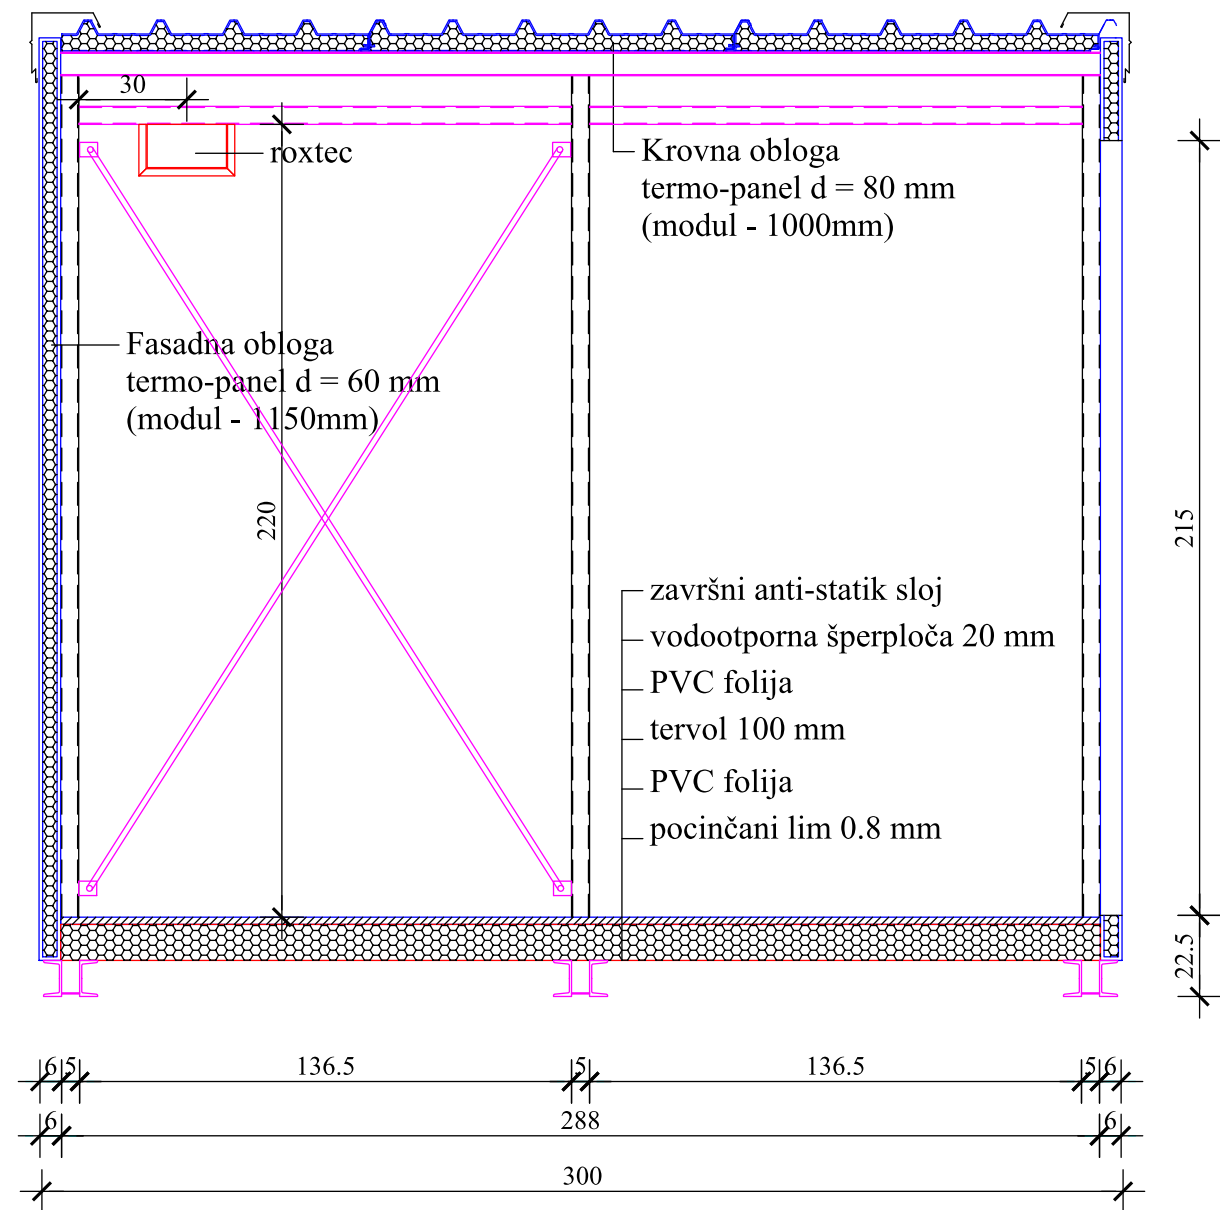

Investitor: BH TELECOM d.d.		Objekat: Infrastruktura bazne stanice mobilne telefonije		 Dioničko društvo Sarajevo	
Glavni projekat Knjiga 1/1	Faza: A	godina: 2018.	šifra projekta: GP-BS-10472-326		
Naziv crteža: Presjek 1-1 objekta za smještaj opreme		razmjera: 1:50	broj crteža: 2 - (149/177)	ovjerio:  Projektant: Dženadin Mušinović, d.i.g.	

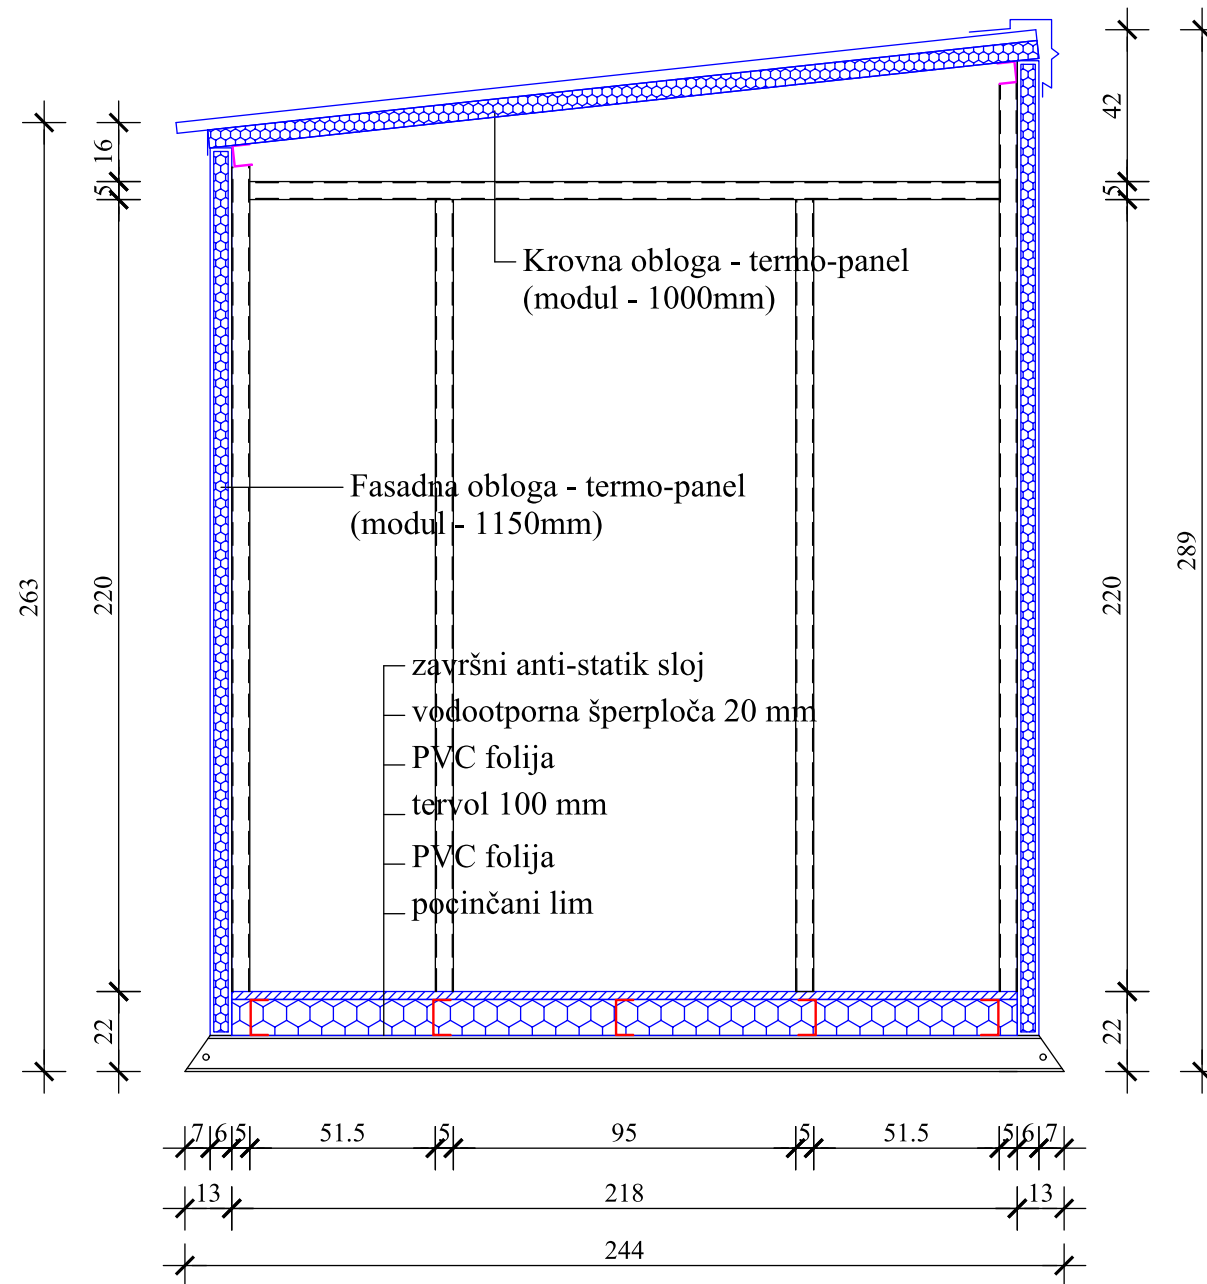


Investitor: BH TELECOM d.d.		Objekat: Infrastruktura bazne stanice mobilne telefonije		 Dioničko društvo Sarajevo	
Glavni projekat Knjiga 1/1	Faza: A	godina: 2018.	šifra projekta: GP-BS-10472-326		
Naziv crteža: Presjek 2-2 objekta za smještaj opreme			razmjera: 1:50	broj crteža: 3 - (150/177)	ovjerio: Projektant: Dženadin Mušinić, d.i.g.

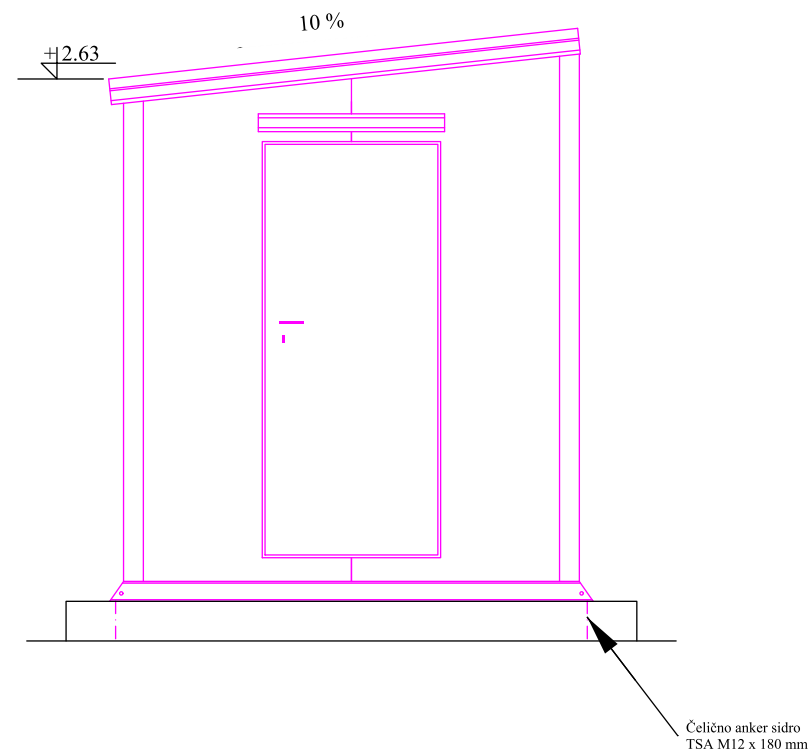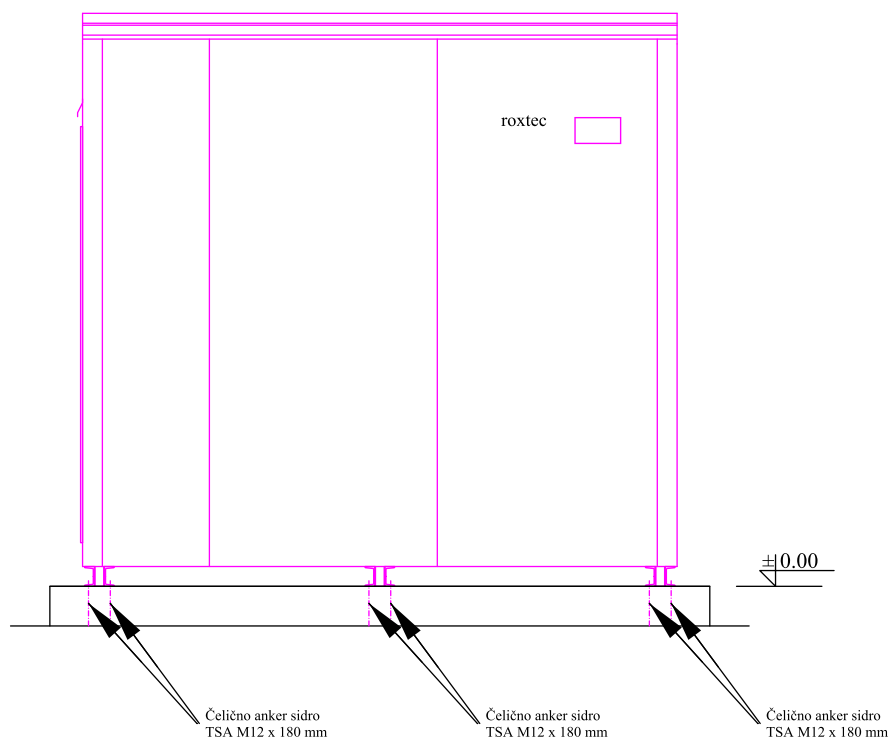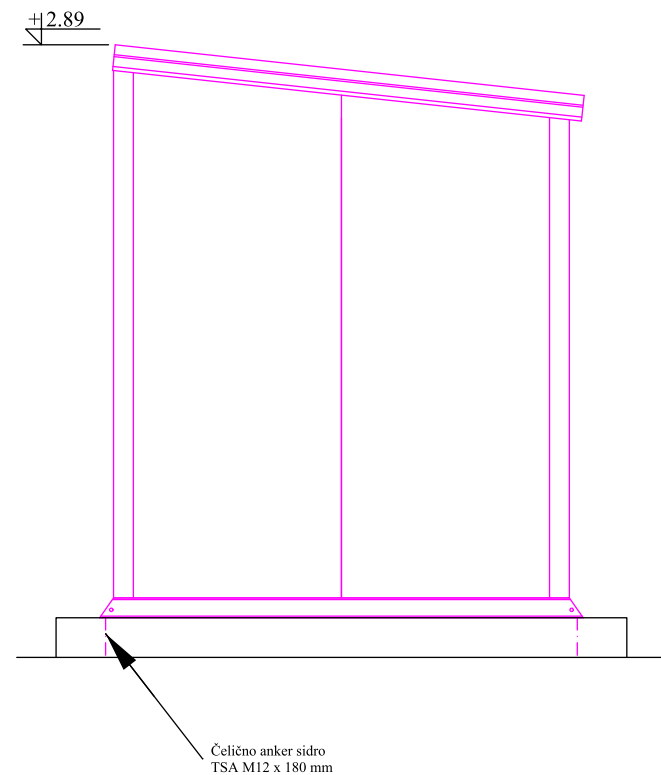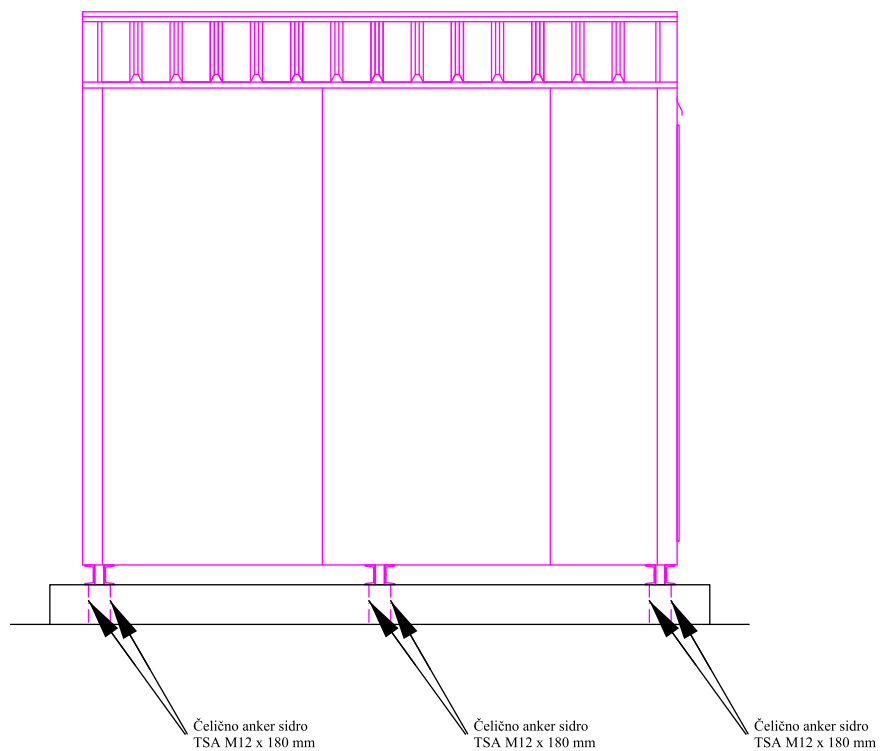


Investitor: BH TELECOM d.d.		Objekat: Infrastruktura bazne stanice mobilne telefonije		 Dioničko društvo Sarajevo	
Glavni projekat Knjiga 1/1	Faza: A	godina: 2018.	šifra projekta: GP-BS-10472-326		
Naziv crteža: Fasade objekta za smještaj opreme				razmjera: 1:50	broj crteža: 4 - (151/177)
				ovjerio: Projektant:Dženadin Mušinović,d.i.g.	


Ugaoni vanjski opšav

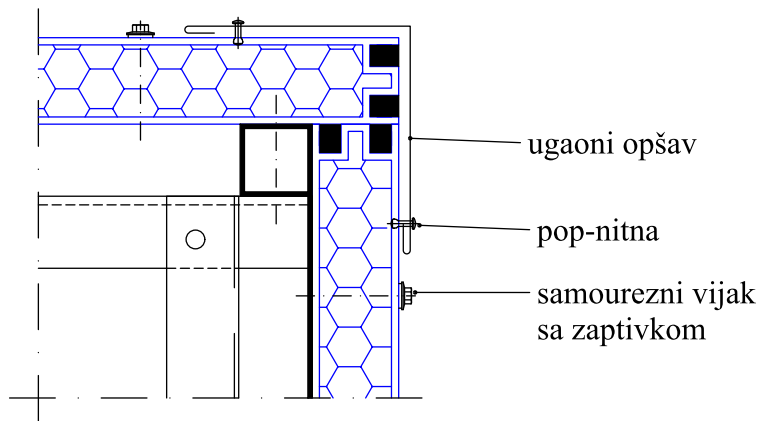


Čeoni lim na višem kraju krova

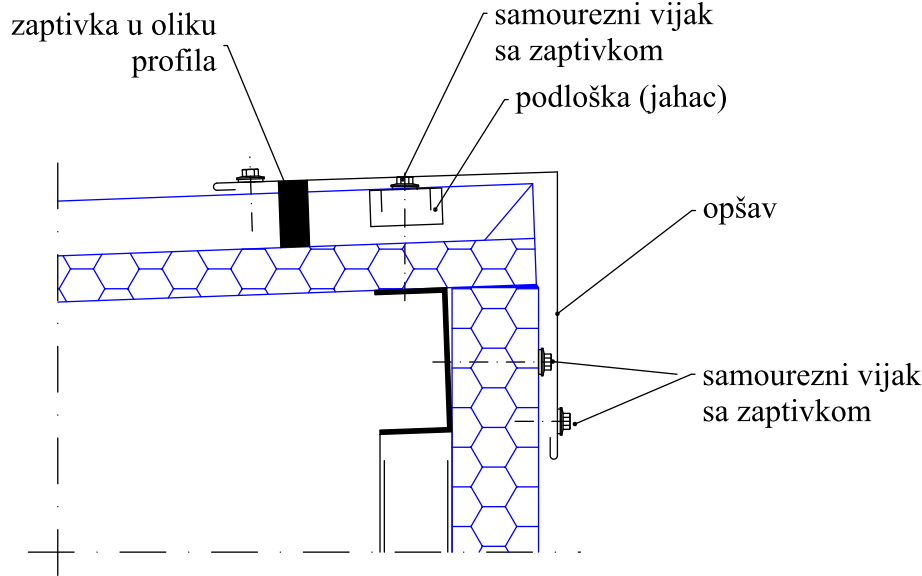

Čeoni lim na nižem kraju krova

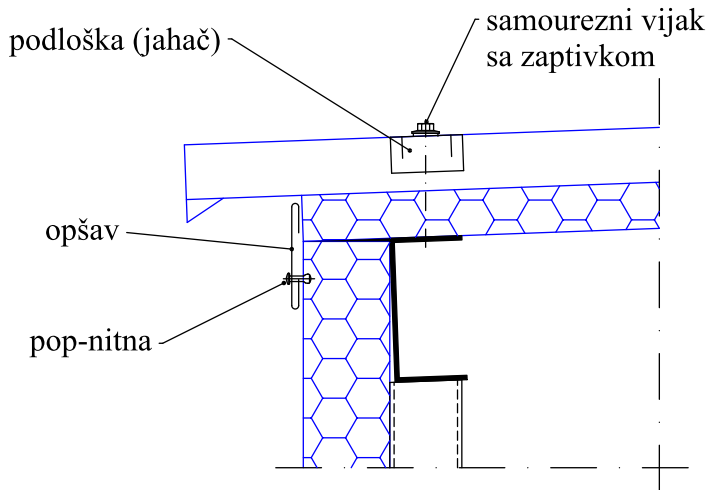


Bočni krovni opšav

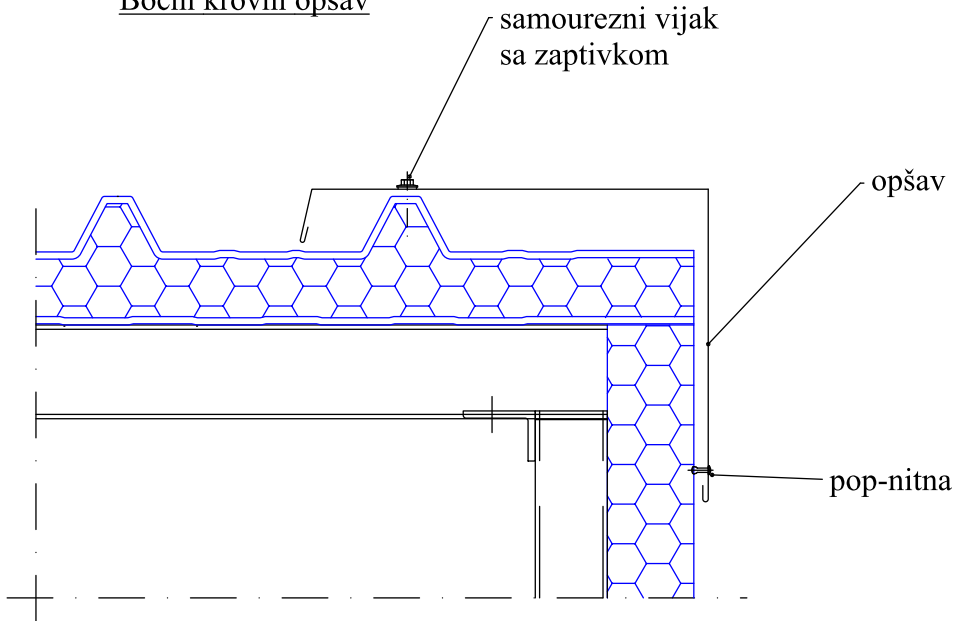


Investitor: BH TELECOM d.d.		Objekat: Infrastruktura bazne stanice mobilne telefonije		bh telecom Dioničko društvo Sarajevo	
Glavni projekat Knjiga 1/1	Faza: A	godina: 2018.	šifra projekta: GP-BS-10472-326	broj crteža: 5 - (152/177)	ovjerio: Projektant: Dženadin Mušinović, d.i.g.
Naziv crteža: DETalji objekta za smještaj opreme				razmjera: 1:50	

PLAN OPLATE TEMELJNOG BLOKA


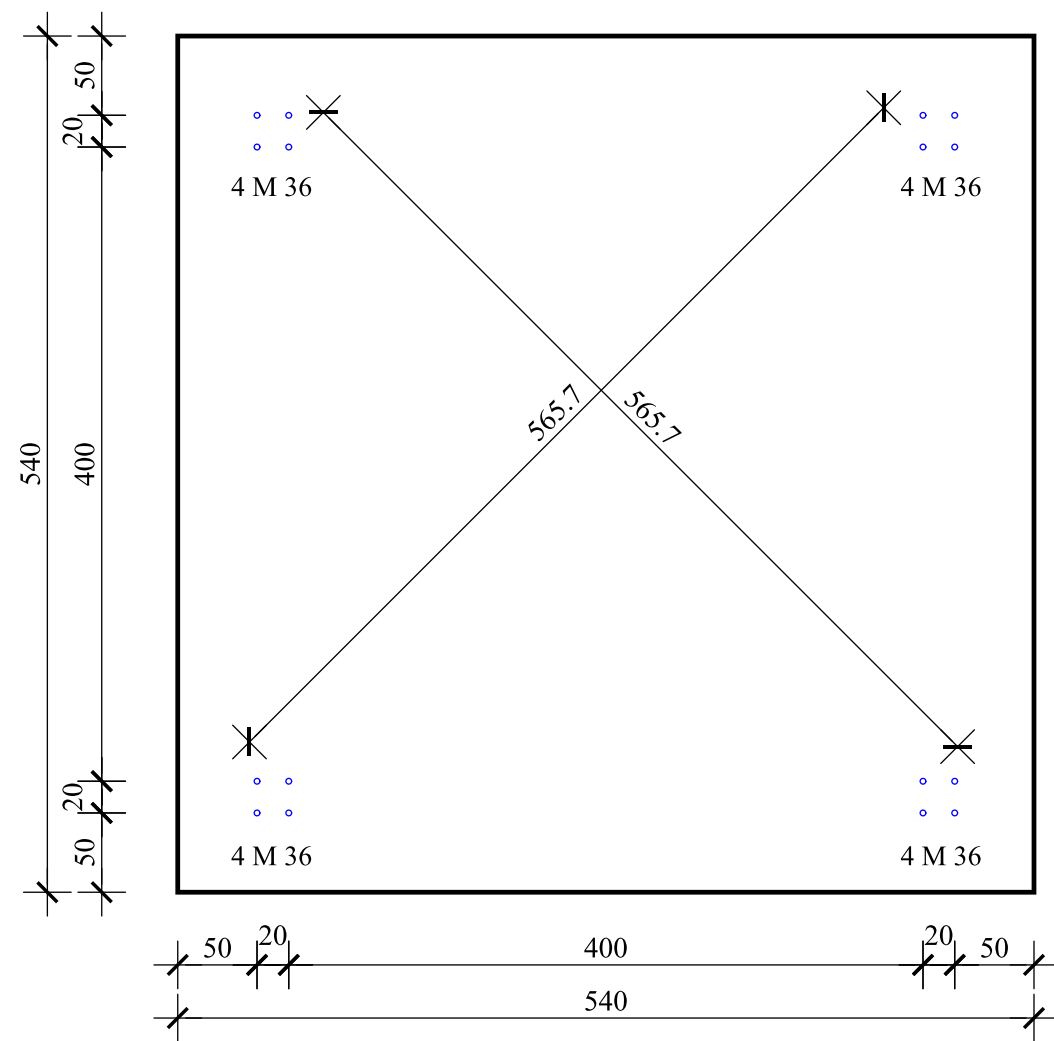


PLAN ARMATURE TEMELJNOG BLOKA

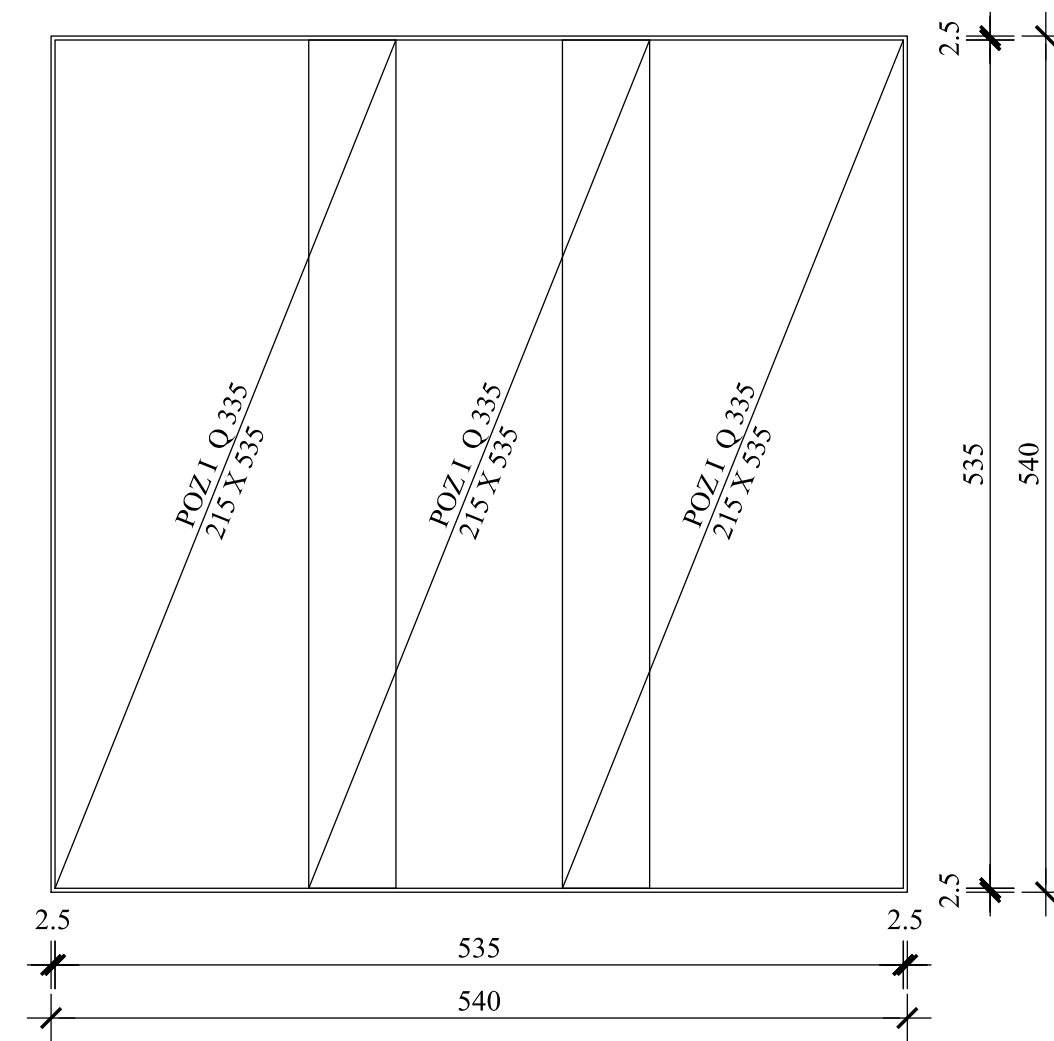


Ankeri Ø 36 mm l = 200 cm komada 4x4=16

Vilice Ø 10 mm/20 cm l = 116 cm komada 4x6=24

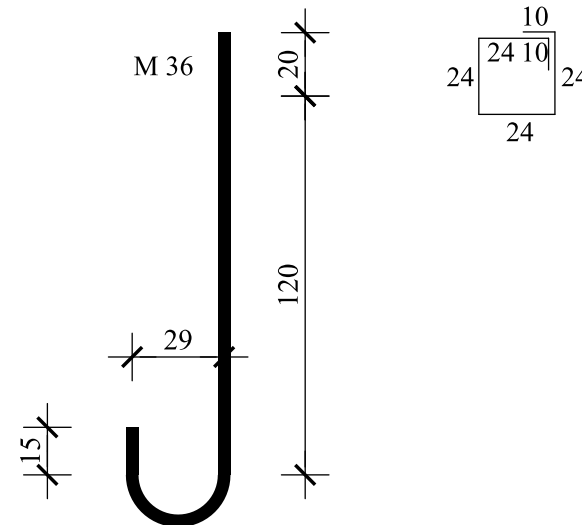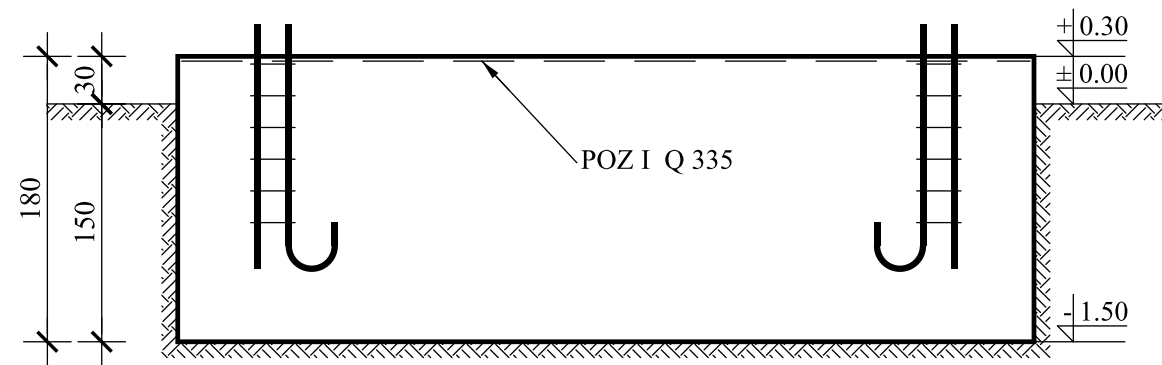



MB 25 (B.I, M-100)
RA 400/500
MA 500/560

Investitor: BH TELECOM d.d.		Objekat: Infrastruktura bazne stanice mobilne telefonije		 Dioničko društvo Sarajevo	
Glavni projekat Knjiga 1/1	Faza: K	godina: 2018.	šifra projekta: GP-BS-10472-326		
Naziv crteža: Plan oplata i armature temelja				razmjera: 1:50	broj crteža: 3 - (121/177)
				ovjerio: Projektant: Dženadin Mušinović, d.i.g.	

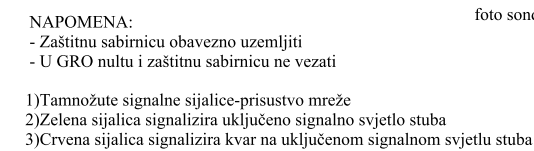

Investitor: BH TELECOM d.d.		Objekat: Infrastruktura bazne stanice mobilne mreže		 Dioničko društvo Sarajevo	
Glavni projekat Knjiga EI	izdanje: I	godina: 2018.	šifra projekta: GP-BS-10472-326		
Naziv crteža: 3.5.2. Jednopolna šema GRO			razmjera:	broj crteža:	Projektant: Močević Džafer, d.e.i.
				48/69	ovjerio: 

FN simulacija — proizvodnja i energetski bilans (informativno)

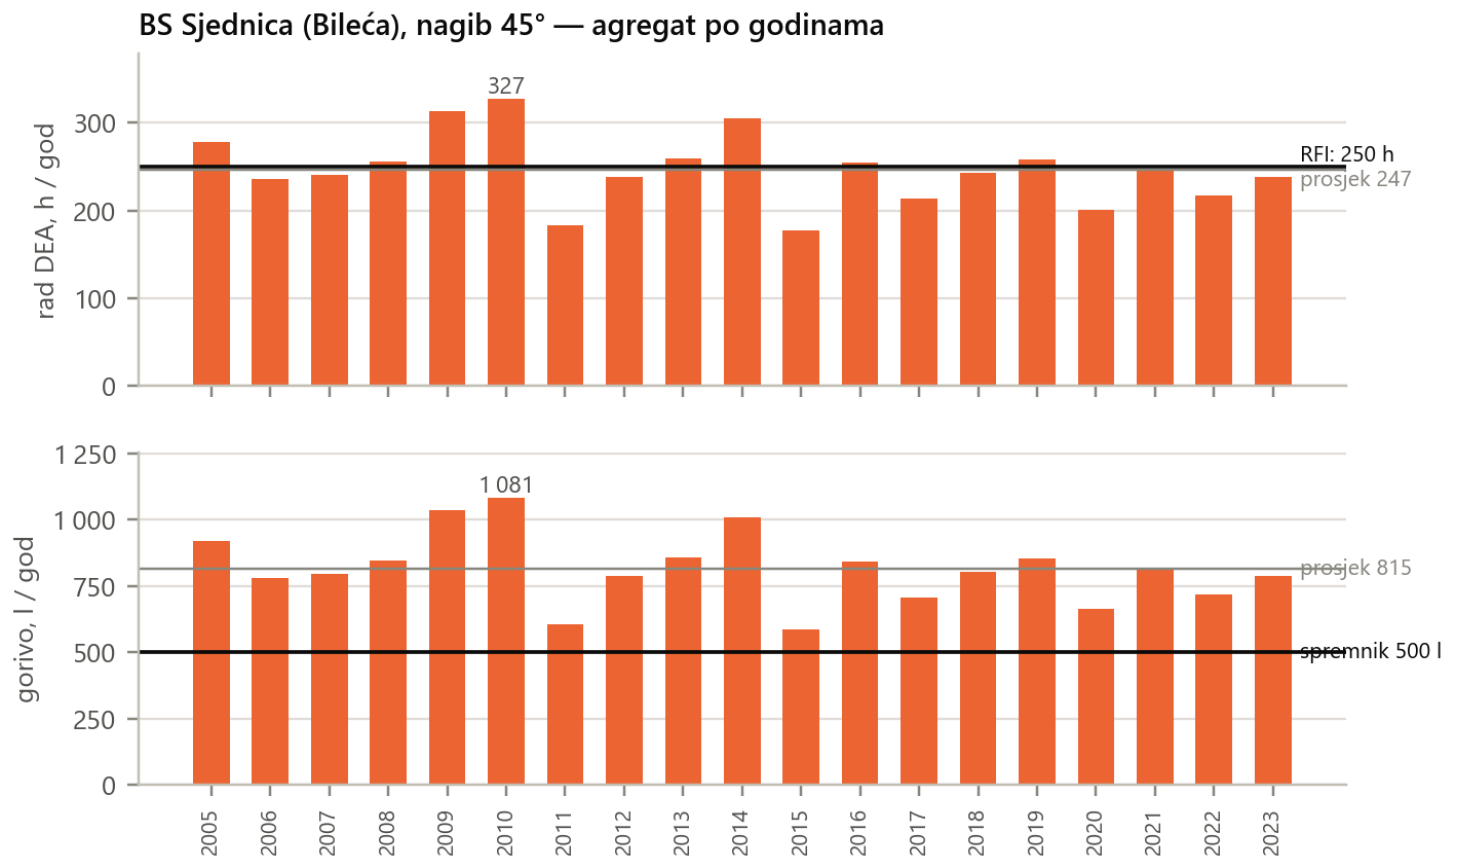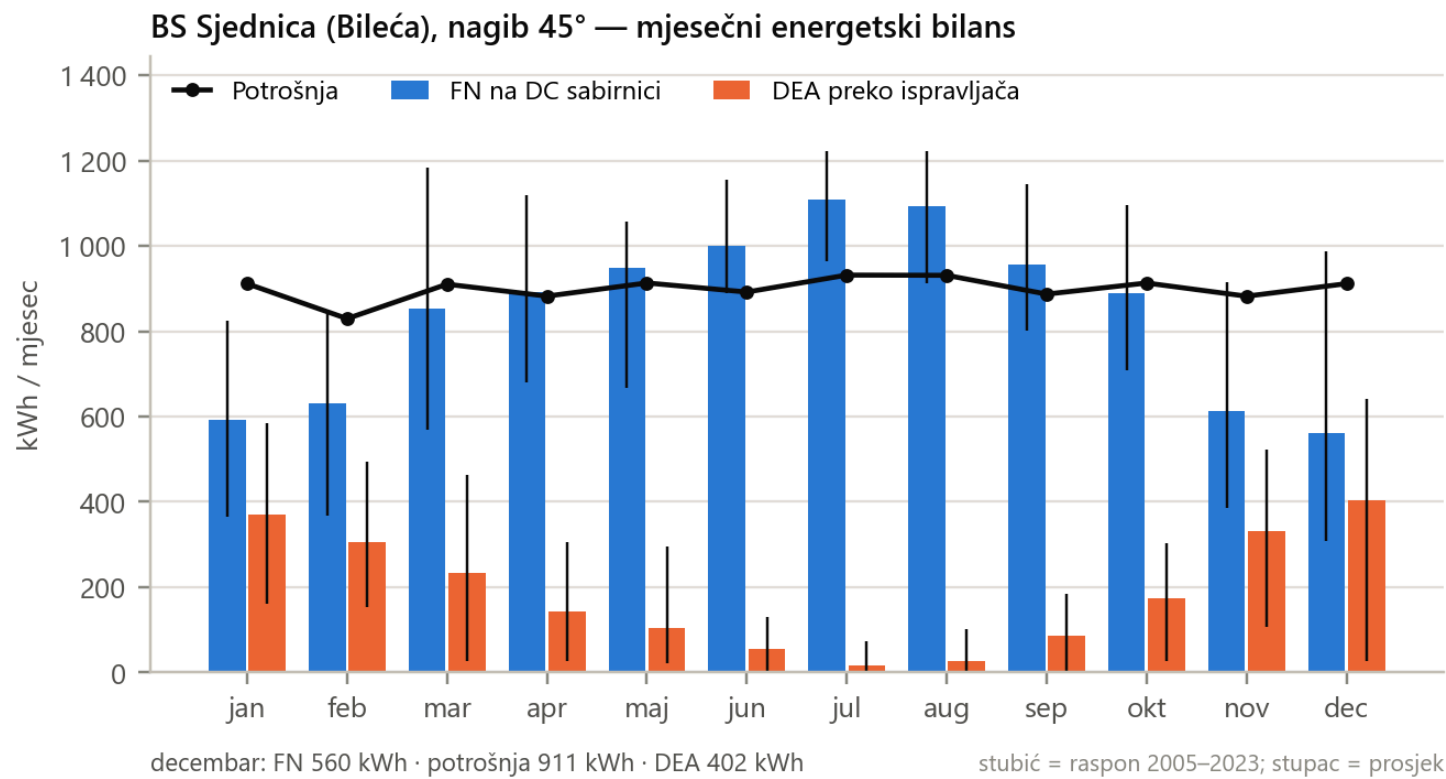

Polje	12 × iPV585-M2A = 7,02 kWp, nagib 45°, azimut 180° (jug)
FN na DC sabirnici (–48 V)	10 137 kWh/god · 1 444 kWh/kWp
Potrošnja	10 794 kWh/god (1180 W + hlađenje ormara i pomoćna potrošnja)
Decembar	FN 560 kWh prema potrošnji 911 kWh
Solarni udio u potrošnji	79,2 %
Rad DEA	prosjek 247 h/god · 9 od 10 godina ≤307 h · najviše 327 h
Gorivo	prosjek 815 l/god · dopuna spremnika 500 l 2,1 puta godišnje
Nepokrivena potrošnja	0 kWh u 19 godina
Provjera prema PVGIS-u	PVcalc 9 692 kWh/god, pvsim sa istim gubicima 9 621 kWh/god; najveće mjesečno odstupanje 2,0 %

Satna simulacija energetskog bilansa na –48 V DC sabirnici za 2005–2023 (pvlib + PVGIS-SARAH3), uz parametrisiranje SMU iz Priloga I, Tačka 4.6: start pri DOD 85 %, zaustavljanje pri SoC 60 %, ograničenje ispravljača 9,5 kW. Metoda, gubici, osjetljivost i pretpostavke: Proračuni, dio A.6. Vrijednosti su informativne i ne mijenjaju zahtjeve Priloga I. Izvor: review/pvsim/kpis.json (sha256 f52ff392ecd6, pvsim commit cd567a2).