


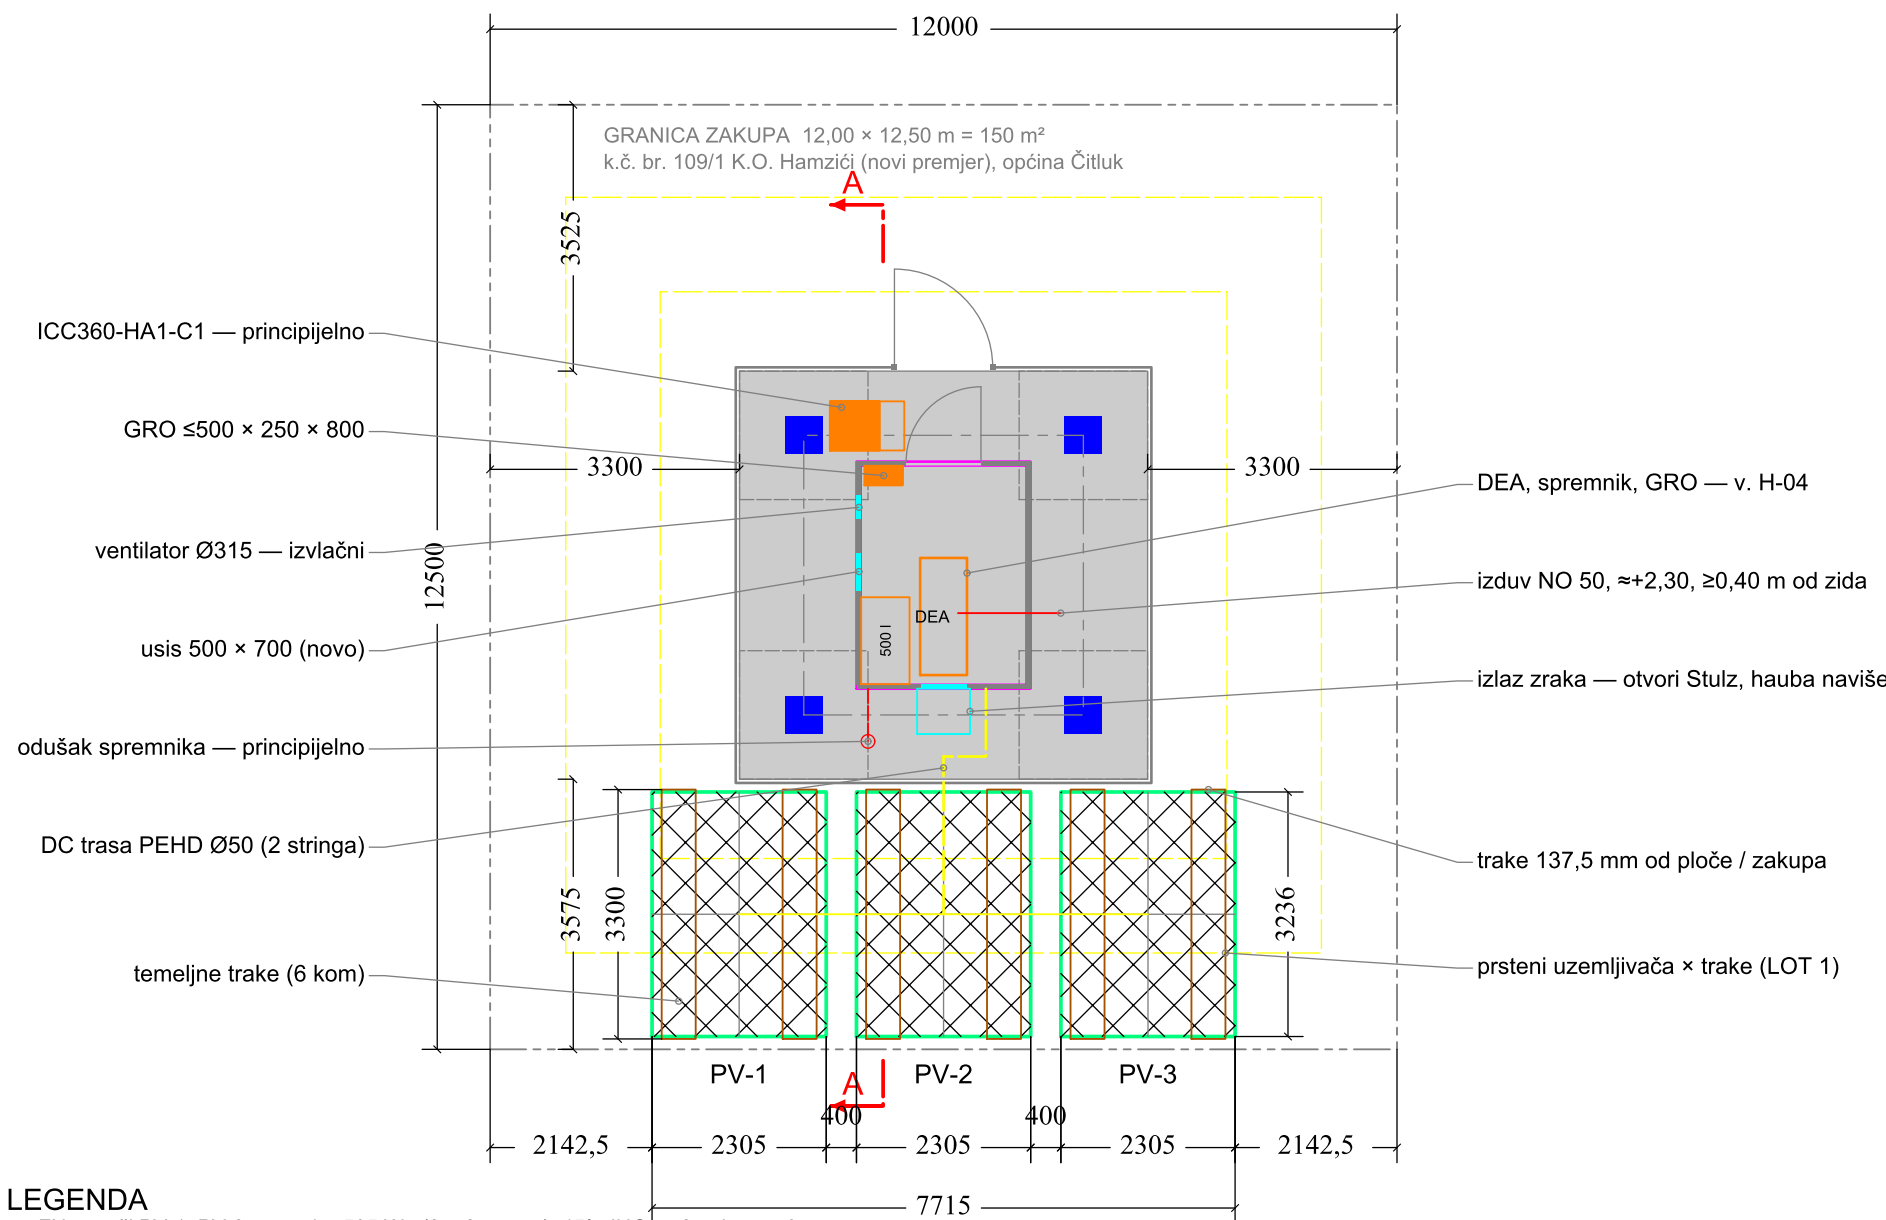

LEGENDA

- FN nosači PV-1..PV-3 — po 4 × 585 Wp (2 × 2 portret), 45°, JUG — 2 stringa × 6
- AB temeljne trake 450/550 × 3300 mm, d = 900 mm, razmak 1600 mm
- DC trasa u PEHD Ø50 (isprekidano) — od polja do kontejnera
- DEA 18 kVA (skid), spremnik 500 l u koritu, novi GRO
- usis 500 × 700 (ZAPAD), izlaz zraka kroz otvore Stulz (JUG) i haubu naviše, ventilator Ø315
- izduv NO 50 (ISTOK, ≈+2,30 m); odušak spremnika (isprekidano); presjek A–A
- Huawei ICC360-HA1-C1 vani na ploči (SJEVER), vrata na ISTOK — principijelno

NAPOMENA — ORIJENTACIJA:

Vrata kontejnera i kapija ograde su na SJEVERU, malo prema sjeverozapadu (fotografije 08.09.2026, Naručilac 11.09.2026). Ovjereni crtež lokacije iz 2017 (GP-BS-10472-291, 01_Situacija 1_200) zakrenut je ≈180° u odnosu na teren; ovdje je okrenut prema terenu i nacrtan pravougaono na sjever. Mali preostali zakret NIJE izmjeren — potvrđuje se obilaskom lokacije.

NAPOMENE:

- Nosači su okrenuti prema JUGU (azimut 180°), nagib 45°; donja ivica panela +0,50 m, gornja +3,74 m — 1,74 m iznad vrha ograde (ograda 1,80 m iznad ploče = 2,00 m iznad terena).
- Polje 3 × 2305 + 2 × 400 = 7715 mm, centrirano istok–zapad; sve je unutar granice zakupa.
- Ako granica zakupa odstupa od pravca istok–zapad, nosači se postavljaju kaskadno unutar južnog pojasa ili upravo na granicu zakupa, uz odstupanje azimuta ≤15°.
- Temeljne trake 450/550 × 3300 mm, d = 900 mm, na podložnom betonu 50 mm, pravac SJEVER–JUG; 137,5 mm od ploče i od granice zakupa.
- Postojeći prsteni uzemljivača (0,8 m; 1,05 i 2,30 m od ploče): ukrštanja sa temeljnim trakama — lociranje, otkopavanje i premještanje ili premoštavanje prstena (LOT 1).
- Vjetar qp ≥ 1,20 kN/m² — nosač CUSTOM izrade; ovjereni statički proračun dostavlja Ponuđač.
- Raspored u kontejneru prema H-04; izlaz zraka kroz otvore Stulz (JUG) i haubu naviše.
- Ormar ICC360-HA1-C1 — principijelno, potvrđuje se na licu mjesta; napaja se iz GRO (izvod F1) kroz sjeverni zid. Odušak spremnika — principijelno, konačno prema elaboratu zaštite od požara (≥3 m od izduva i usisa, ≥1 m od ormara).



BH TELECOM d.d. SARAJEVO

Izvršna direkcija za tehnologiju i razvoj servisa

Investitor:

BH Telecom d.d. Sarajevo, Franca Lehara 7, Sarajevo

Objekat:

BS HAMZIĆI (ČITLUK) — autonomni hibridni sistem napajanja

Faza:

Tenderska dokumentacija — Prilog III

Naziv crteža:

Situacija — BUDUĆE STANJE

Projektant:

Rusmir Skopljak, dipl. ing. el.

ovjerio:

Rusmir Skopljak, dipl. ing. el.

šifra projekta:

BHT-HAMZICI-2026

razmjera:

1:100

godina / broj crteža:

2026. H-02